

-1F原始平面图  
SCALE:1:600

# 是境設計

项目名称 PROJECT	湖山春晓
总负责 PRINCIPAL	
设计 DESIGNER	
绘图 DRAWN BY	
校对 COLLATE	
审核 APPROVE	
比例 SCALE	1 : 60
日期 DATE	2020.07
图名 DRAWING TITLE	

备注  
NOTE

A vertical scale bar with numerical markings. The markings are as follows from top to bottom: 200, 1700, 200, 3300, 200, 2200, 200, and 8000.

备注  
NOTE

在未经同意前，不得复制图纸及其设计  
任何部份。

□所有图纸尺寸标注须在实际工地复核及  
量度。

—本公司承認的圖紙，當向設計師及交  
他有關圖紙一并使用，如發現圖紙內容  
有不符之處，必須立刻通知設計師。

業主  
CLIENT

项目名称  
PROJECT

龙湖督山

PRINCIPAL

DESIGNER

DRAWN BY 

校对 COLLATE

審核 APPROVE

比例 SCALE 1 : 60

日  
DATE  
期  
2020.07

图 名

### -1F墙体拆除图

圖號  
SHEET NO


-1F.P-01


三  
卷之三

卷之三

卷之三

卷之三

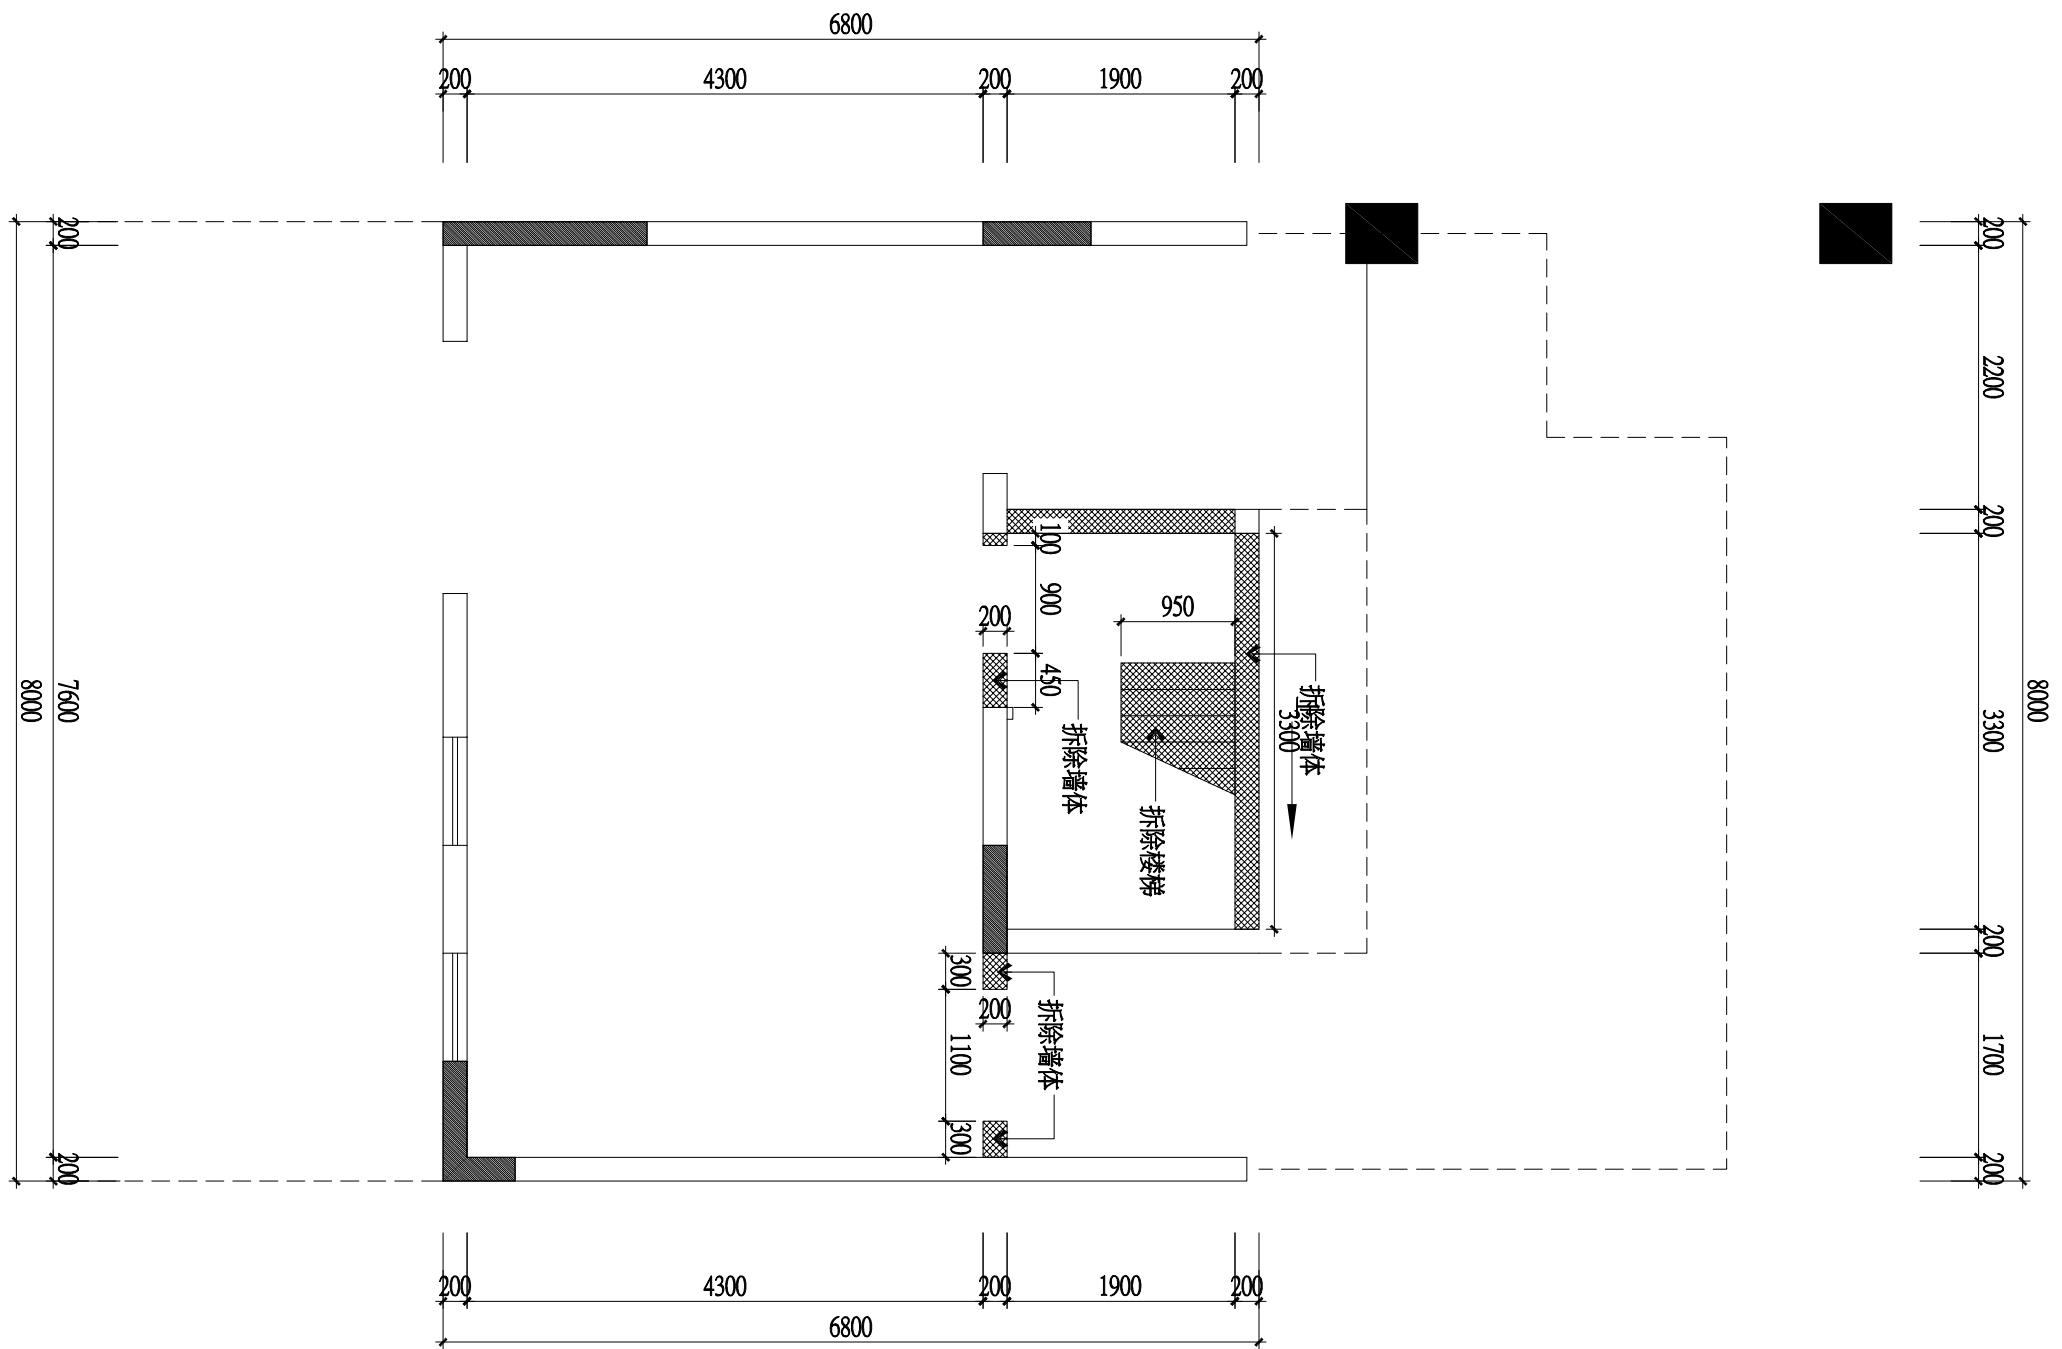

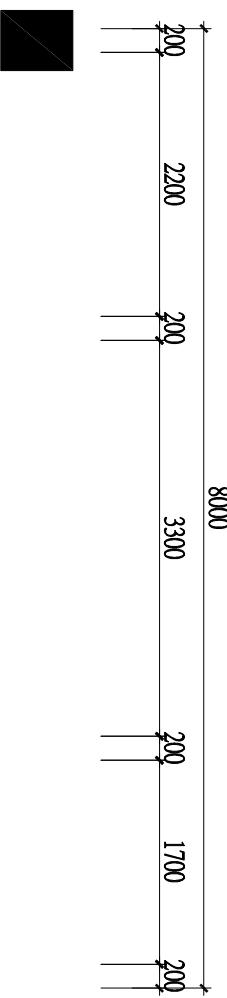

备  
注  
NOTE

□在未经同意前，不得复制图纸及其设计任一部分。  
□所有图纸尺寸标注须在实际工地复核及量度。  
□请勿按比例量度图纸，应采用已标明的尺寸。  
□本图纸必须和招标说明、合同条款及其他有关图纸，并使用，如发现图纸内容有不符之处，必须立刻通知设计者。



02 -1F墙体新建图  
SCALE:1:60

是  
境  
設  
計

-1F墙体新建图  
图号  
SHEET NO  
-1F.P-02

业 主	CLIENT
项 目 名 称	PROJECT
总 负 责	PRINCIPAL
设 计	DESIGNER
绘 图	DRAWN BY
校 对	COLLATE
审 核	APPROVE
比 例	SCALE 1 : 60
日 期	DATE 2020.07
图 名	DRAWING TITLE

NOTE

□在未经同意前，不得复制图纸及其设计任何部分。

□所有图纸尺寸标注须在实际工地上复核及量度。

□请勿按比例量度图纸，应采用已标明的尺寸。

□本图纸必须和规格说明、合同条款及其他有关图纸一并使用。如发现图纸内容有不符之处，必须立刻通知设计师。

业 主  
CLIENT

项 目 名 称  
PROJECT

龙湖椿山

总 负 责  
PRINCIPAL

设 计  
DESIGNER

绘 图  
DRAWN BY

校 对  
COLLATE

审 核  
APPROVE

比 例  
SCALE

1 : 60

日 期  
DATE


2020.07

图 名  
DRAWING TITLE

-1F平面布置图


图 号  
SHEET NO

-1F.P-03

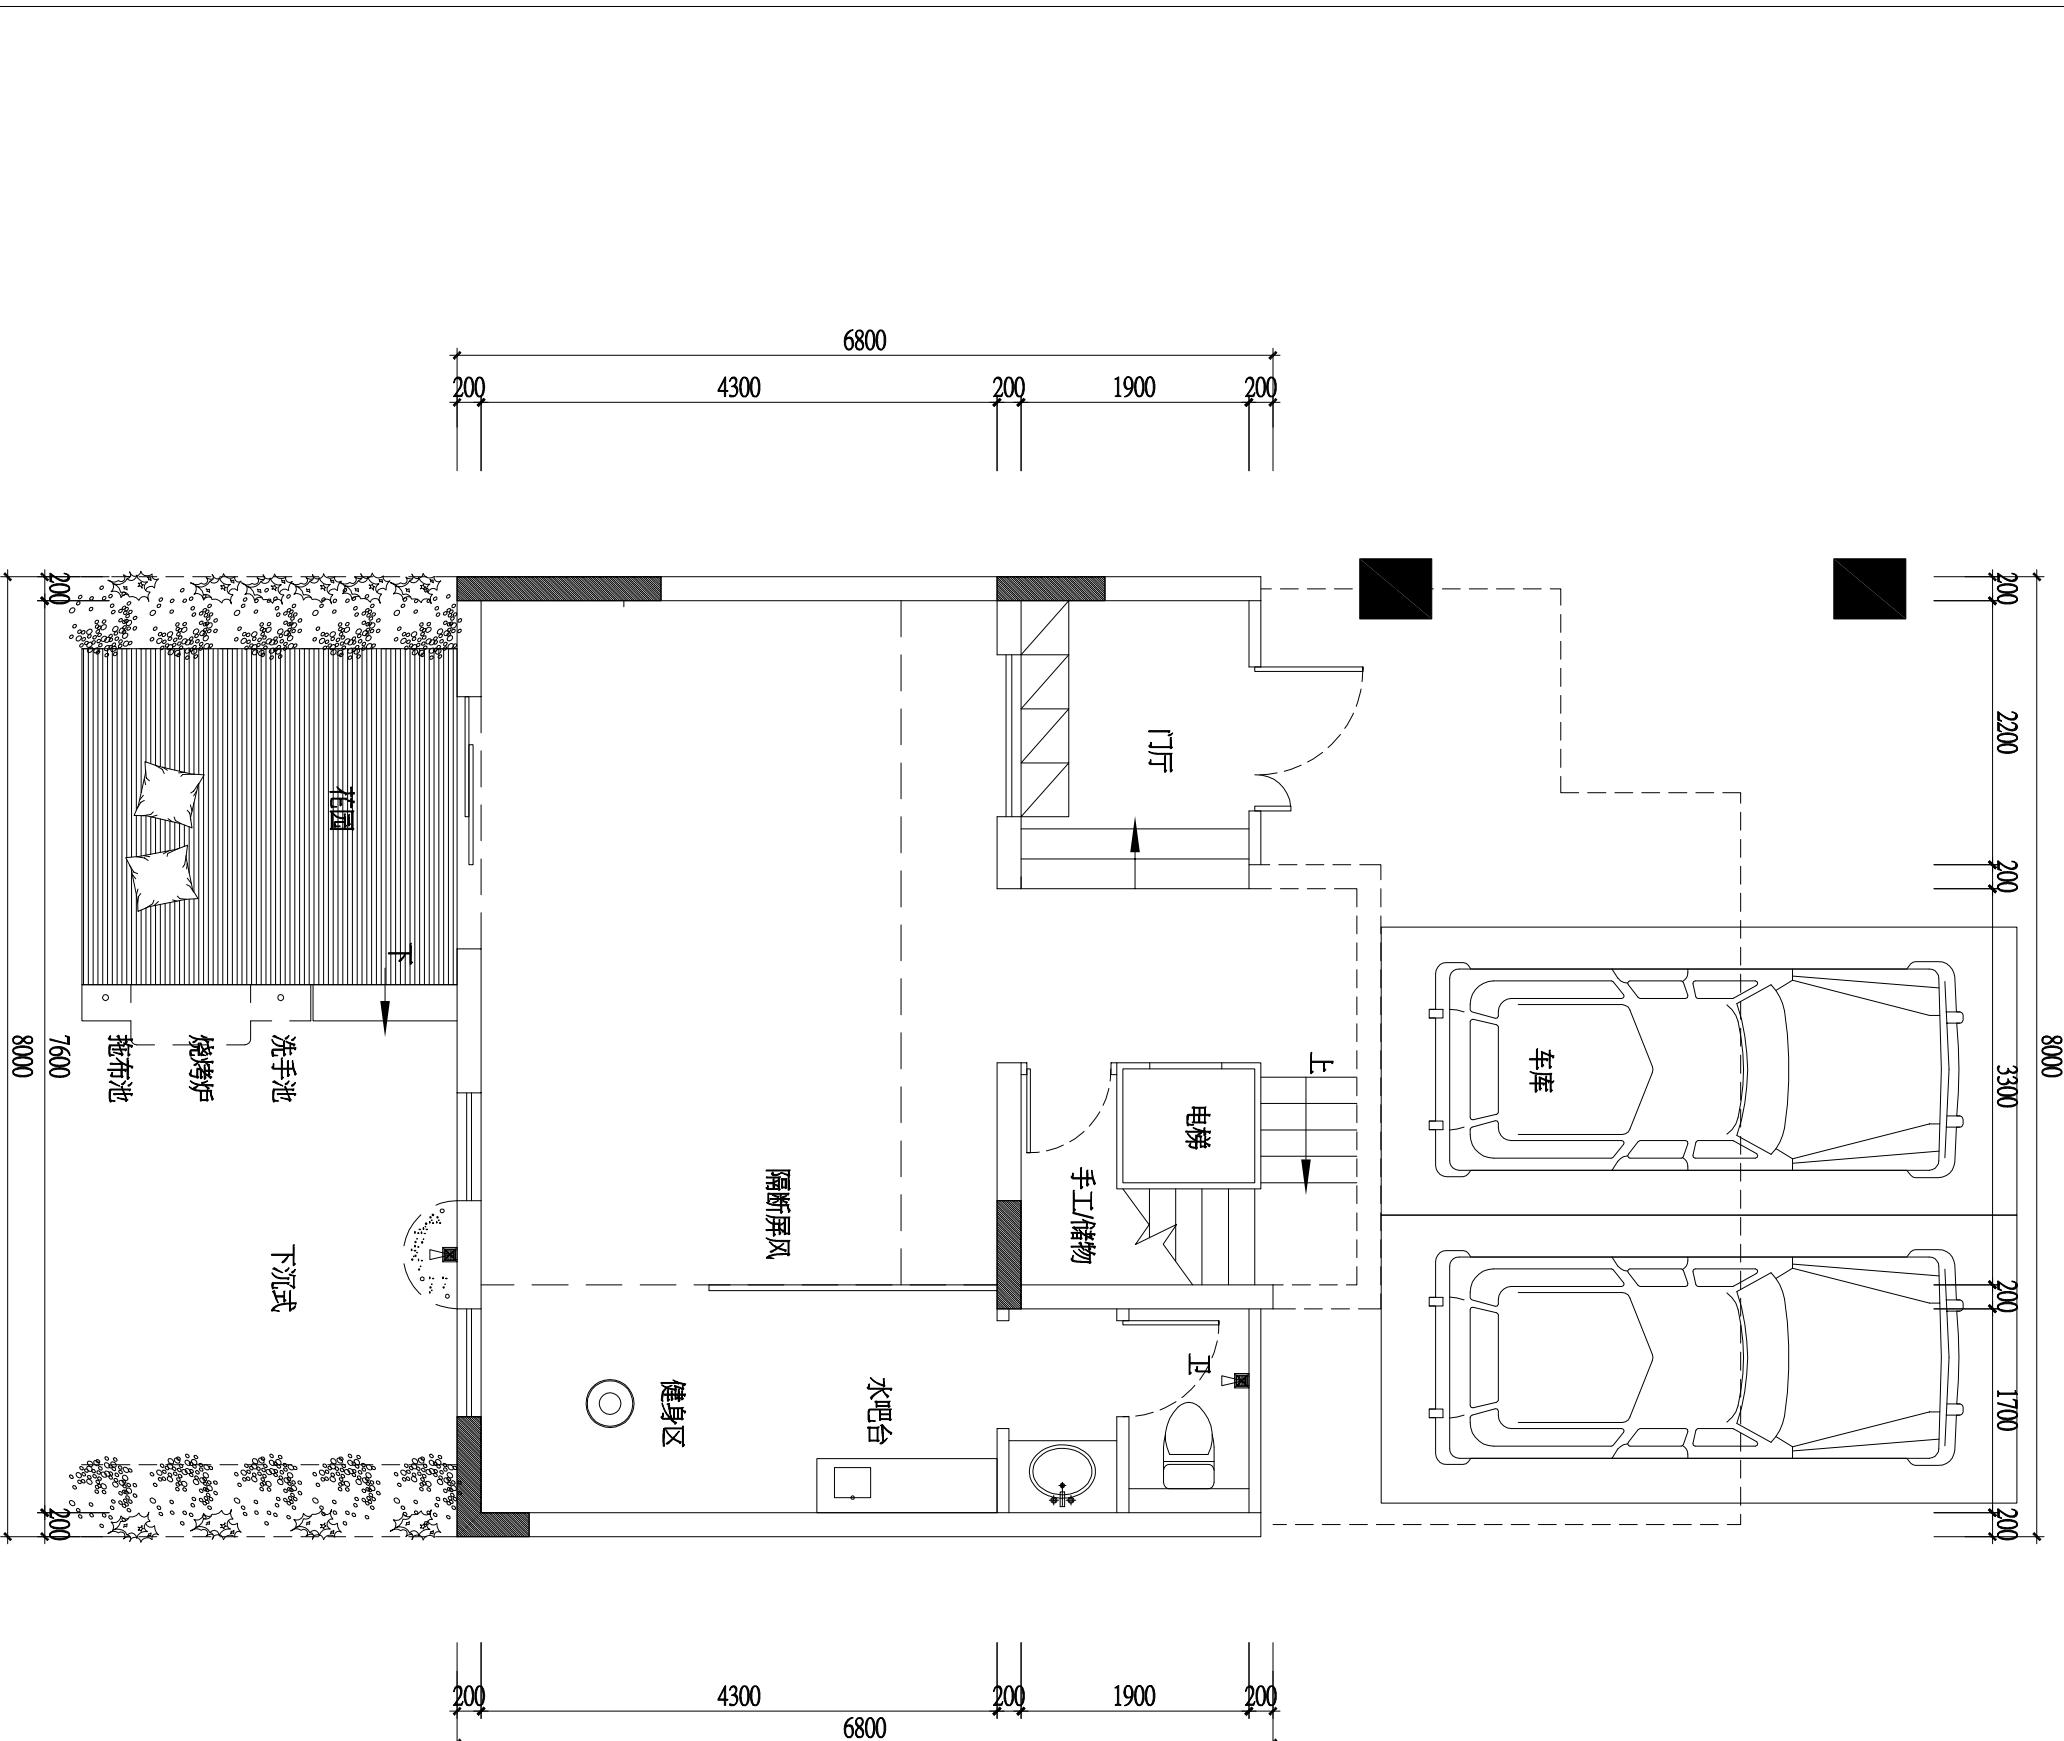

03 -1F平面布置图  
SCALE:1:60


是境  
設計  
設計

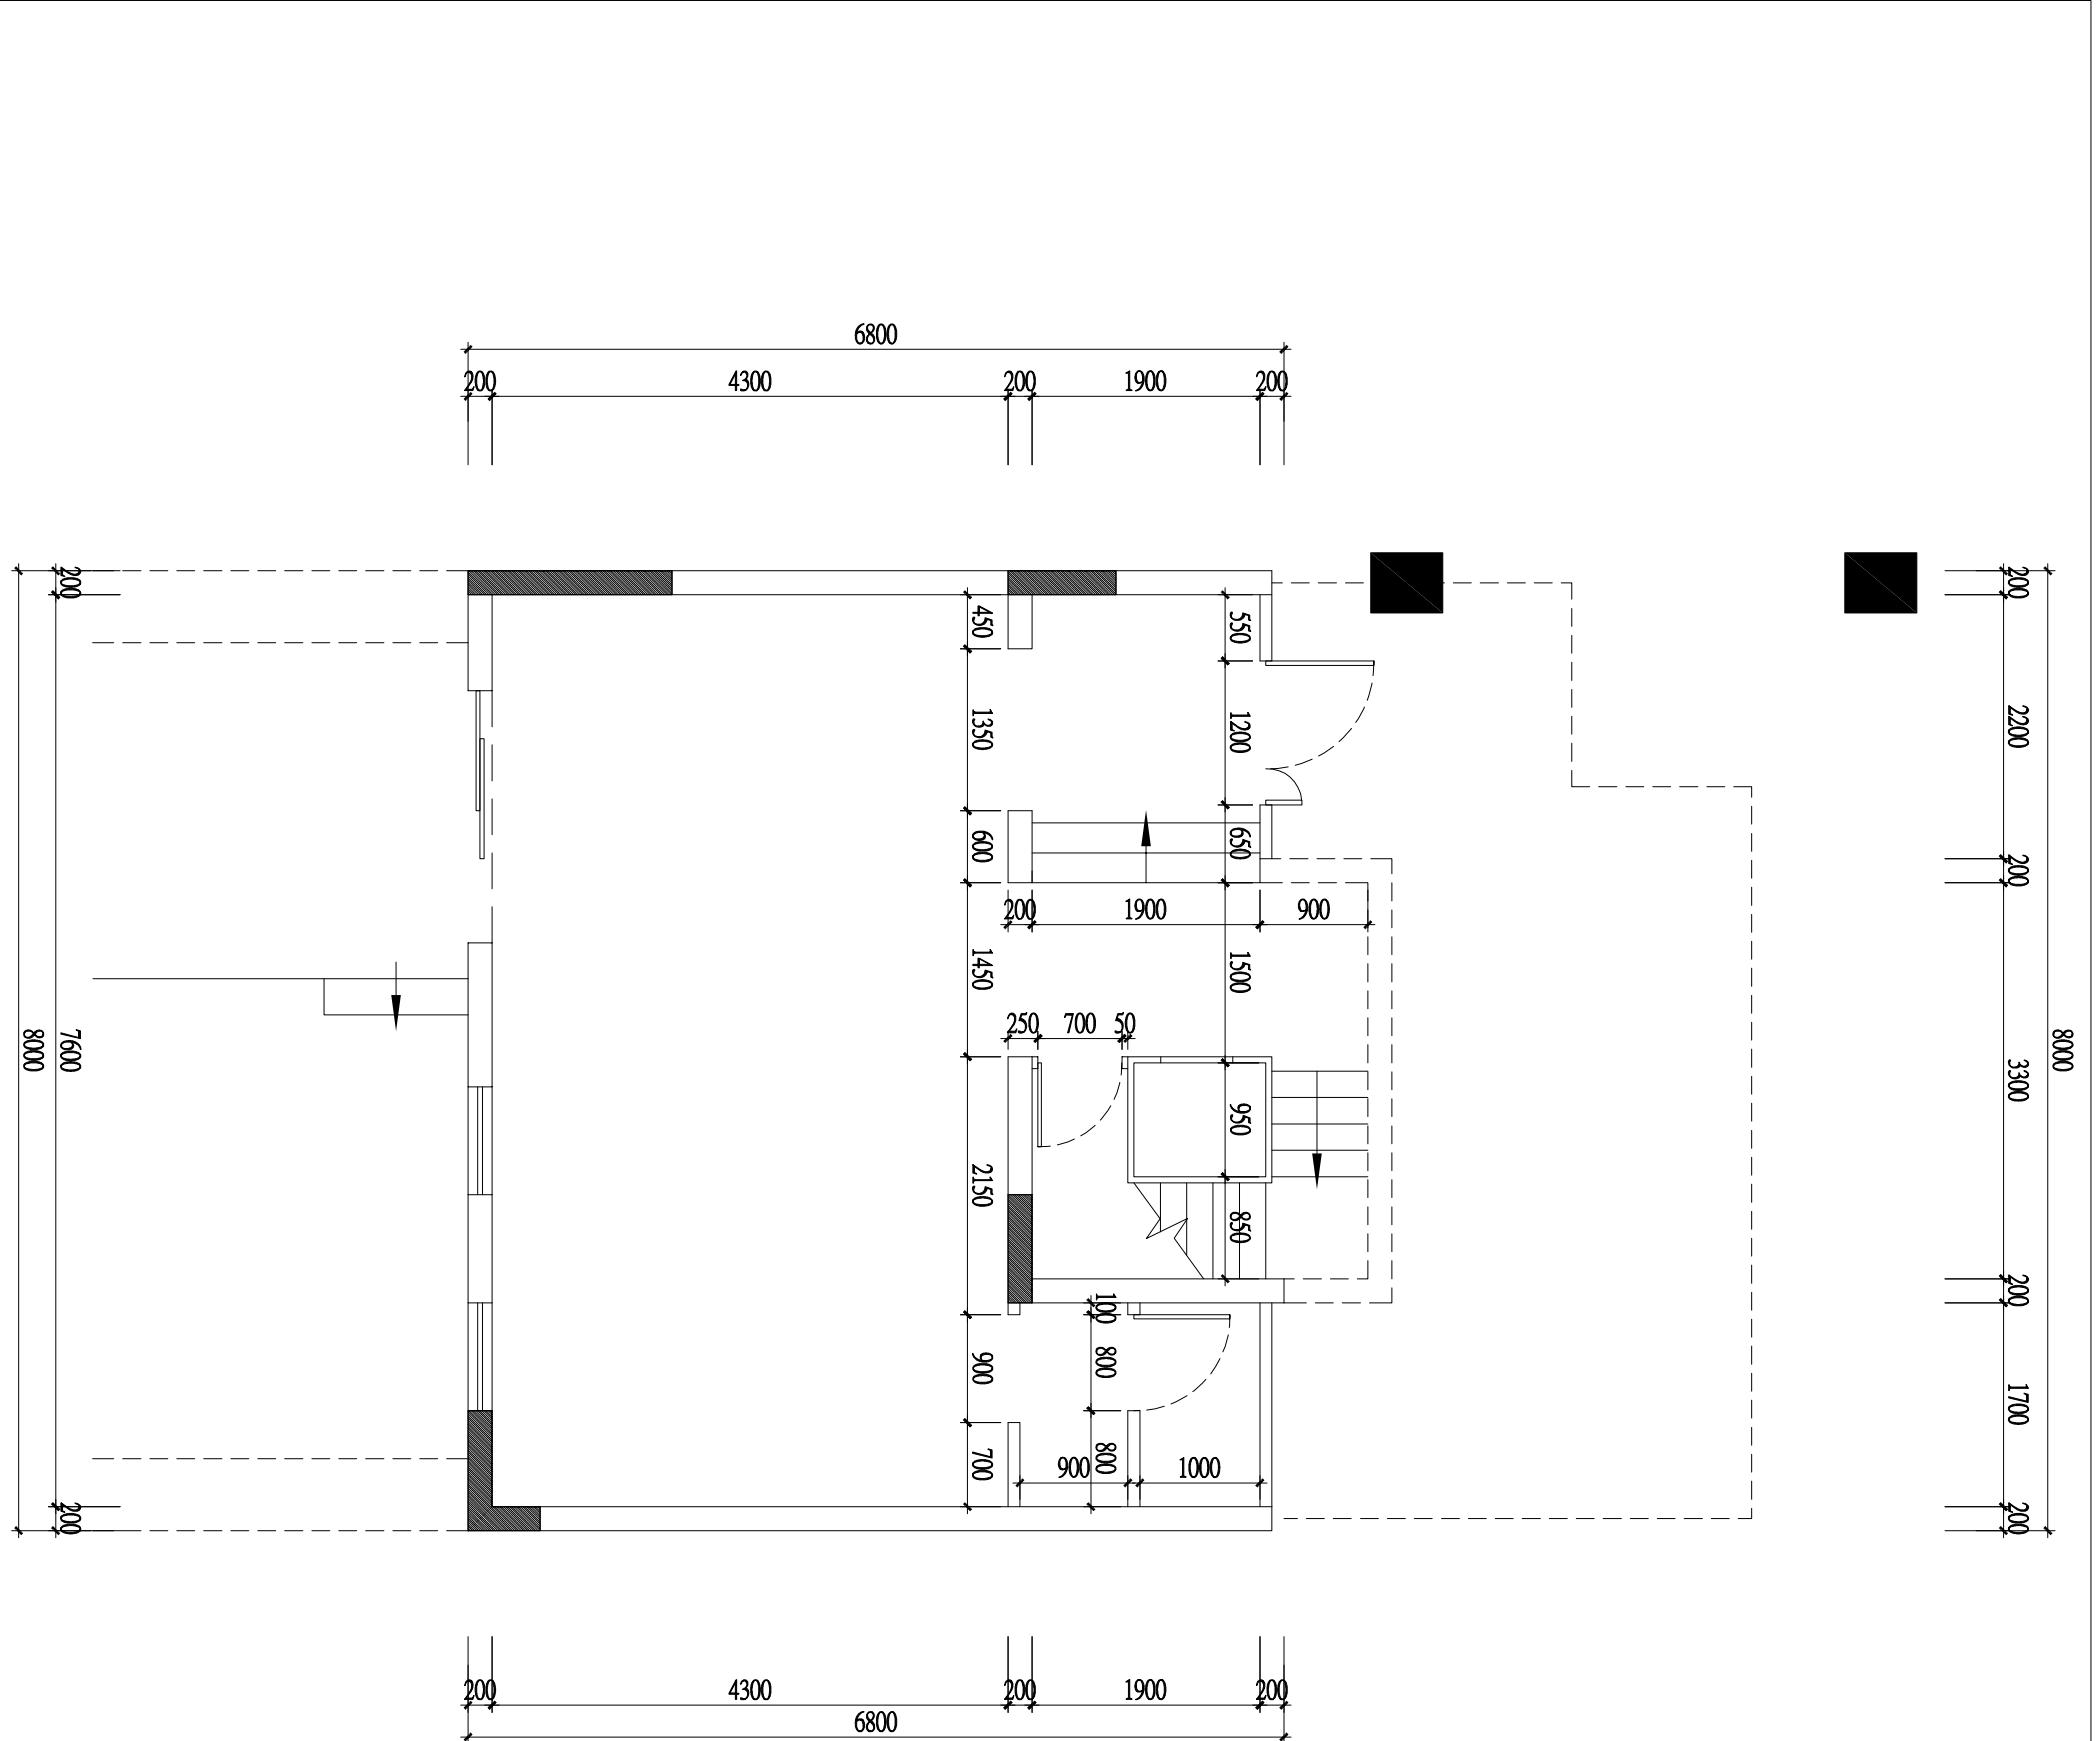

04 -1F隔墙尺寸图  
SCALE:1/60

# 是境設計

□在未经同意前，不得复制图纸及其设计  
备 注  
NOTE

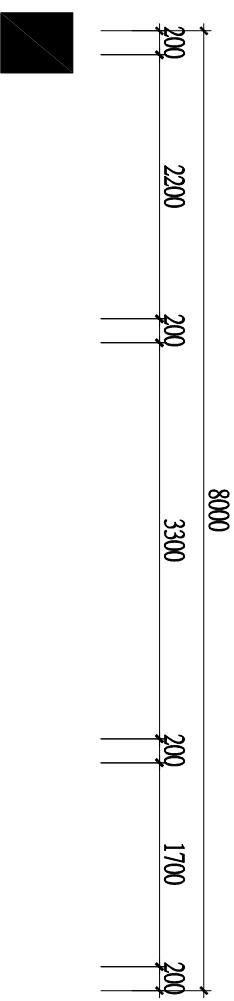

备  
注  
NOTE

□在未经同意前，不得复制图纸及其设计任何部分。

□所有图纸尺寸标注须在实际工地复核及量度。

□请勿按比例量度图纸，应采用已标明的尺寸。

□本图纸必须和现场说明、合同条款及其他有关图纸，并使用，如发现图纸内容有不符之处，必须立刻通知设计师。

业  
主  
CLIENT

项  
目  
名  
称  
PROJECT

总  
负  
责  
PRINCIPAL

设  
计  
DESIGNER

绘  
图  
DRAWN BY

校  
对  
COLLATE

审  
核  
APPROVE

比  
例  
SCALE

日  
期  
DATE

图  
名  
DRAWING TITLE

05  
-1F地面前质图  
SCALE:1:60

是  
境  
設  
計  
計  
圖

图  
号  
SHEET NO

-1F.P-05

NOTE

□在未经同意前，不得复制图纸及其设计任何部分。

□所有图纸尺寸标注须在实际工地上复核及量度。

□请勿按比例量度图纸，应采用已标明的尺寸。  
□本图纸必须和规格说明、合同条款及其他有关图纸一并使用。如发现图纸内容有不符之处，必须立刻通知设计者。

业 主	CLIENT
项目名称 PROJECT	


龙湖椿山

总 负 责 PRINCIPAL	10
设 计 DESIGNER	09
绘 图 DRAWN BY	08
校 对 COLLATE	07
审 核 APPROVE	06
比 例 SCALE	05
日 期 DATE	04
图 名 DRAWING TITLE	03
-1F立面索引图	02
图 号 SHEET NO	01

-1F.P-06

是境  
设计

06 -1F立面索引图  
SCALE:1:60

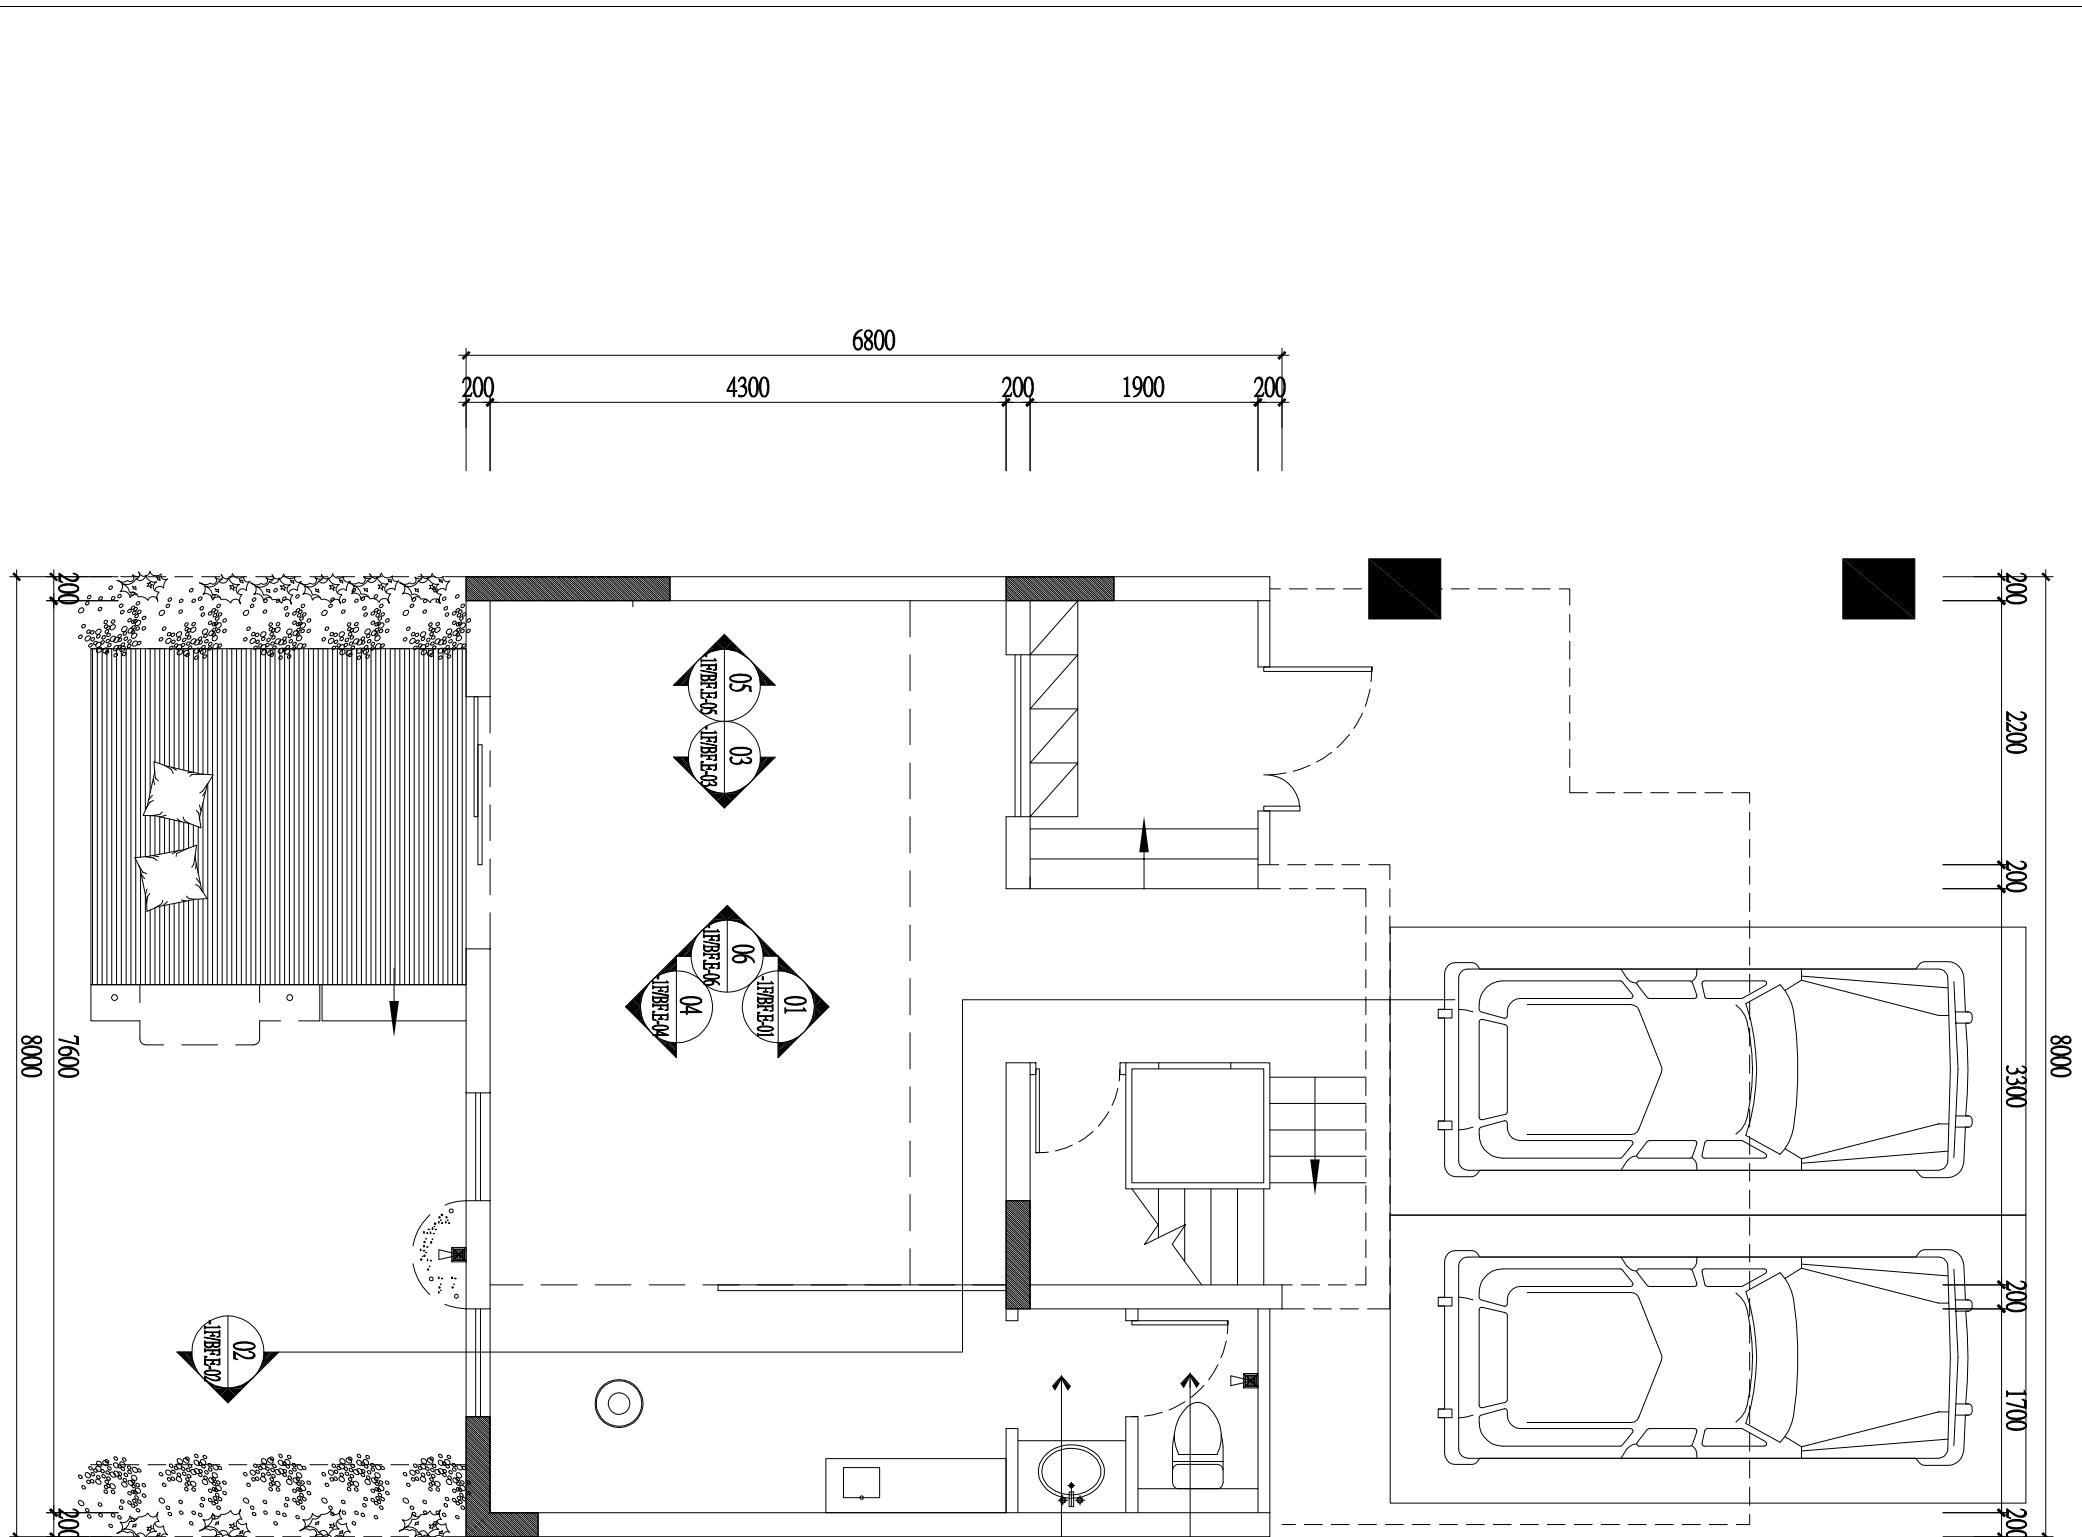

6800  
200 4300 200 1900 200

200 2200 200 3300 200  
8000  
200 1700 200  
7600  
200 8000  
200



200 4300 200 1900 200

10  
09  
08  
07  
14  
13  
12  
11  
06  
05  
04  
03  
02

-1F立面索引图

图 号  
SHEET NO

-1F.P-06

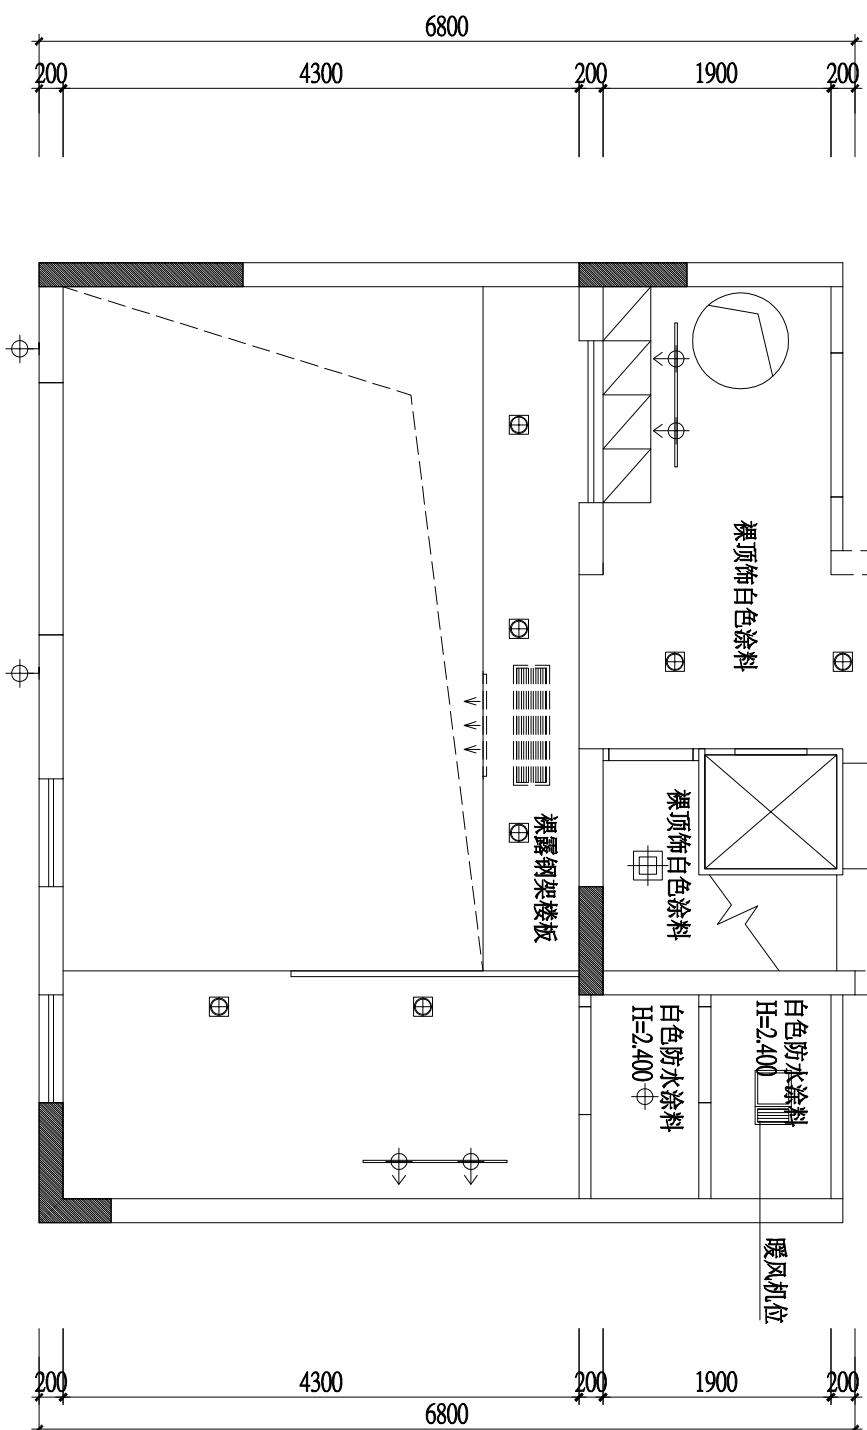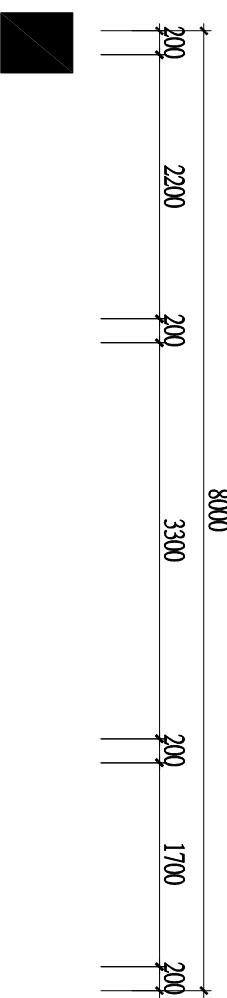

照明灯具说明：

图例	名称	图例	名称
⊕	明装筒灯	——	暗藏式灯带
⊕	防潮筒灯	⊕	壁灯
↑	轨道射灯	⊕⊕	艺术吊灯
⊕	嵌入式筒灯	串	吸顶灯



-1F天花布置图

图号  
SHEET NO  
-1F.P-07

是境  
设计

07 -1F天花布置图  
SCALE:1:60

备 注  
NOTE  
□在未经同意前，不得复制图纸及其设计  
任何部分。  
□所有图纸尺寸标注须在实际工地复核及  
量度。  
□请勿按比例量度图纸，应采用已标明的  
尺寸。  
□本图纸必须和规格说明、合同条款及其  
他有关图纸，并使用，如发现图纸内容  
有不符之处，必须立刻通知设计者。

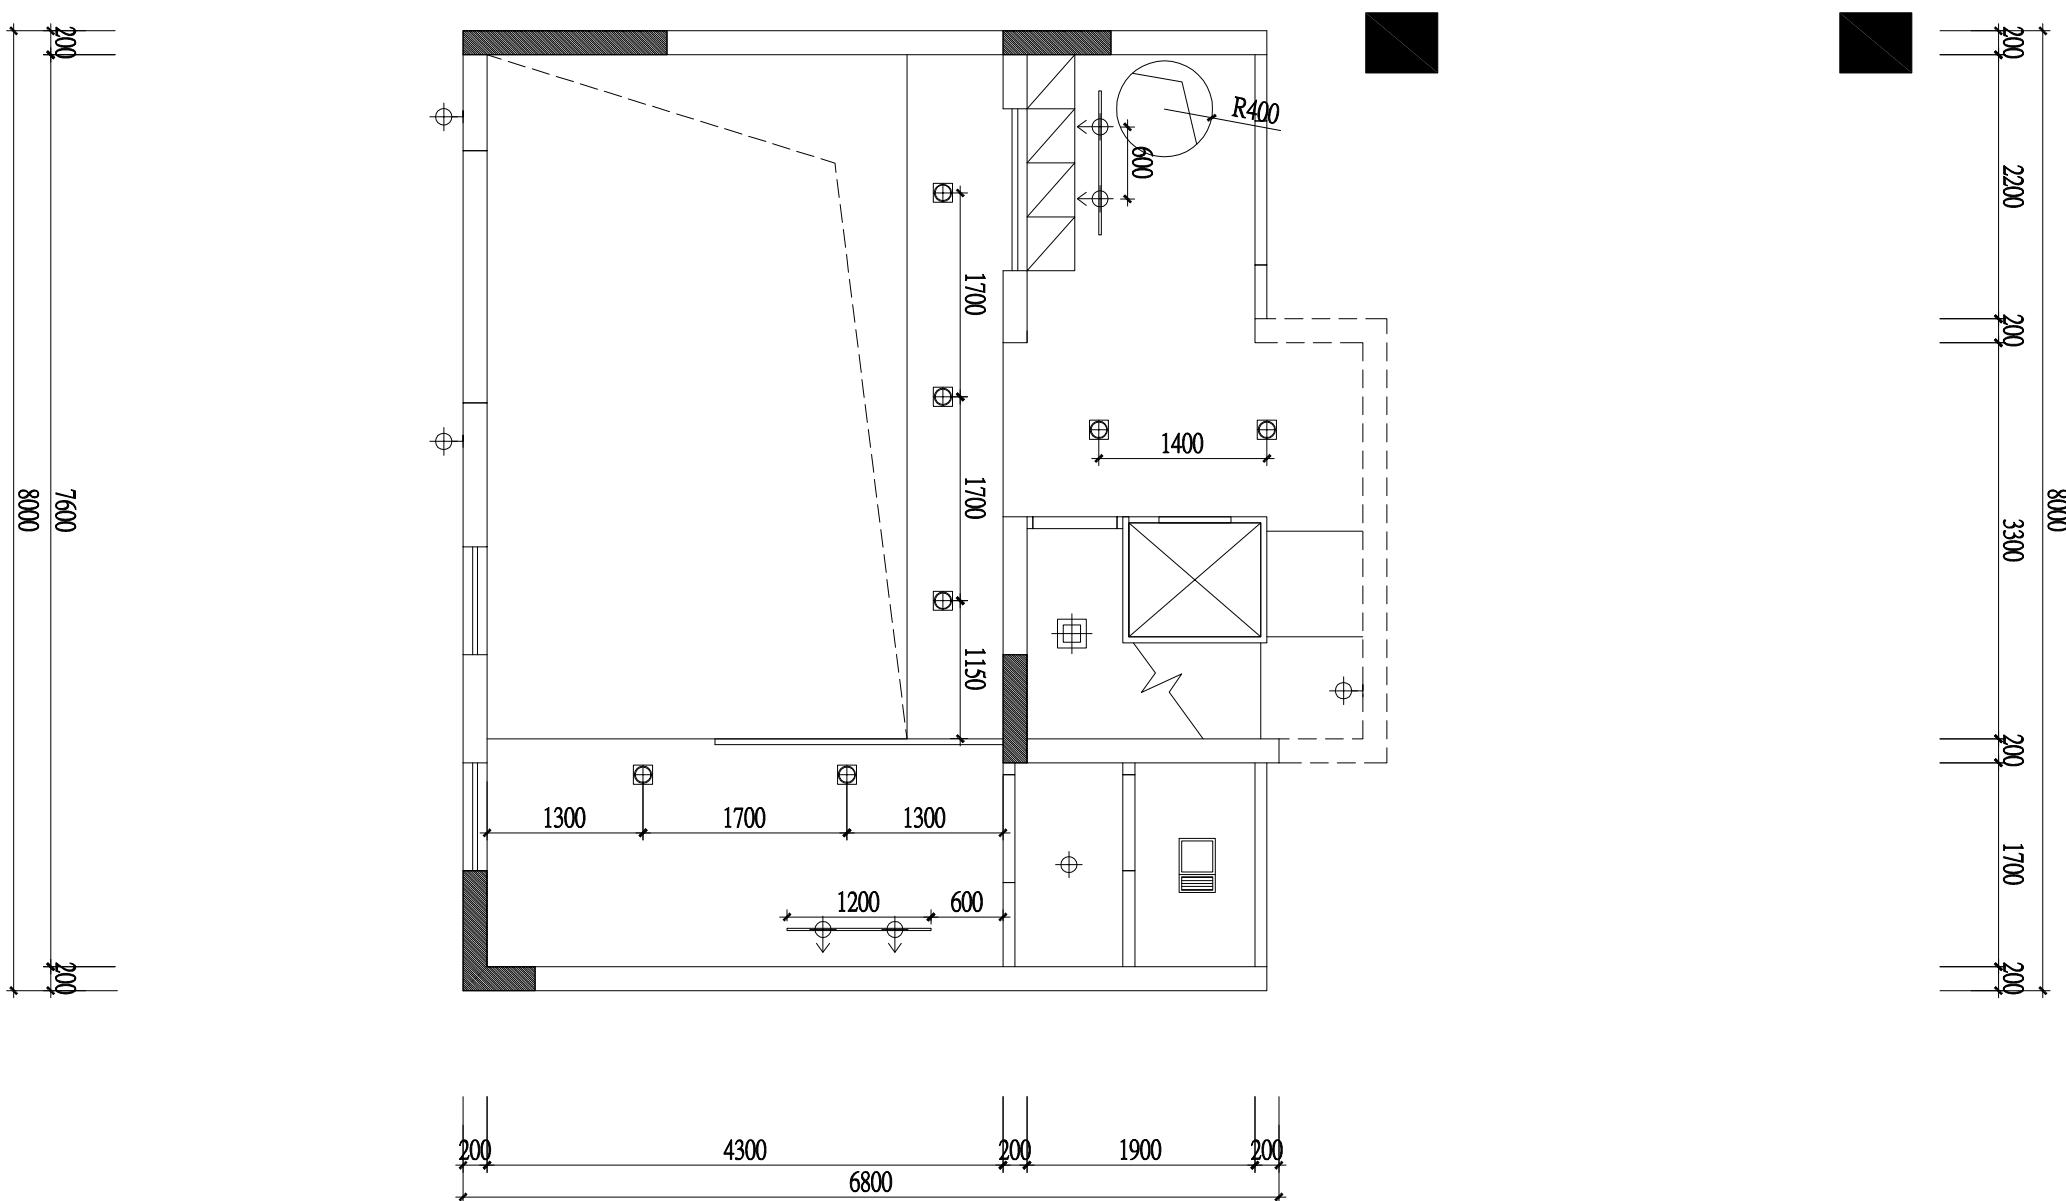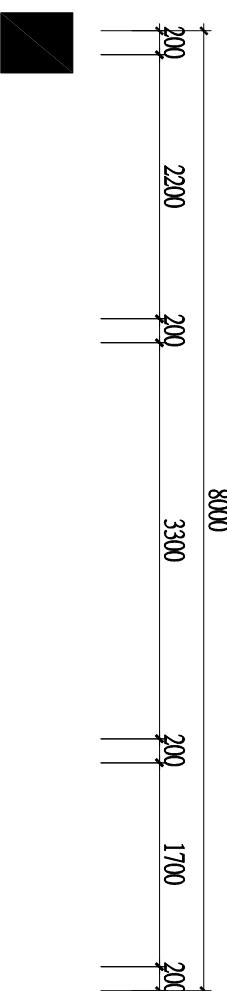

**照明灯具说明：**

图例	名称	图例	名称
Φ	明装筒灯	——	暗藏灯带
⊕	防潮筒灯	⊕	壁灯
↑	轨道射灯	⊕⊕	艺术吊灯
⊕	嵌入式筒灯	串	吸顶灯

-1F天花尺寸图


图号  
SHEET NO

-1F.P-08

是境  
设计

08 -1F天花尺寸图  
SCALE:1:60

备注  
NOTE  
□本图未经同意，不得复制图纸及其设计任何部分。  
□所有图纸尺寸标注须在实际工地复核及量度。  
□请勿按比例量度图纸，应采用已标明的尺寸。  
□本图纸必须和现场说明，合同条款及其他有关图纸，并使用，如发现图纸内容有不符之处，必须立刻通知设计师。

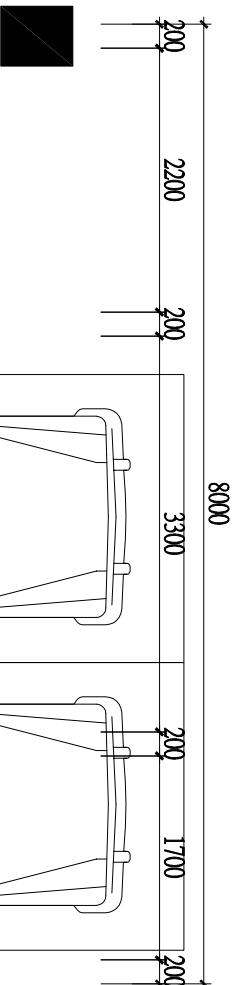

備注  
NOTE

◎在未經同意前，不得複制圖紙及其設計任何部份。

◎所有圖紙尺寸标注須在實際工地實測及量度。

◎請勿按比例量度圖紙，應採用已標明的尺寸。

◎本圖紙必須與規格說明、合同條款及其他有关图纸一并使用。如发现图纸内容有不符之处，必须立刻通知设计者。

業主  
CLIENT

項目名稱  
PROJECT

龍湖椿山

總負責人 PRINCIPAL	
設計師 DESIGNER	
繪圖 DRAWN BY	
校對 COLLATE	
審核 APPROVE	
比例 SCALE	1 : 60
日期 DATE	2020.07
圖名 DRAWING TITLE	-1F.P-09

-1F插座布置图


插座说明

圖例	名稱	圖例	名稱
○	二,三級單相組合安全插座	■	防水插座
●	吹风机	□	地插
▼	電話接口	④	電視接口
◆	網絡接口	EEB	等電位

注：开关盒面板间距20mm;所有标高为中距地。

是境  
設計  
設計

09 -1F插座布置图  
SCALE:1:60

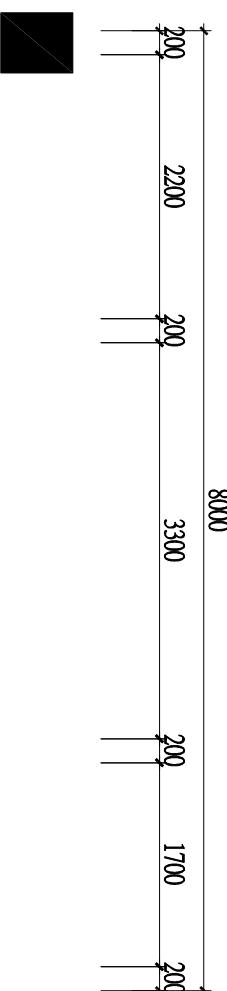

備注  
NOTE

□在未經同意前，不得复制图纸及其设计  
任何部分。  
□所有图纸尺寸标注须在实际工地复核及  
量度。  
□本图纸必须和规格说明、合同条款及其  
他有关图纸，并使用，如发现图纸内容  
有不符之处，必须立刻通知设计者。

□所有图纸尺寸标注须在实际工地复核及  
量度。  
□请勿按比例量度图纸，应采用已标明的  
尺寸。

### 业 主

CLIENT

项目名称  
PROJECT

PRINCIPAL

设计  
DESIGNER

绘图  
DRAWN BY

校对  
COLLATE

审核  
APPROVE

核  
COLLATE

比  
SCALE

例  
EXAMPLE

1 : 60


日  
DATE

期  
PERIOD

2020.07

图  
DRAWING

名  
TITLE

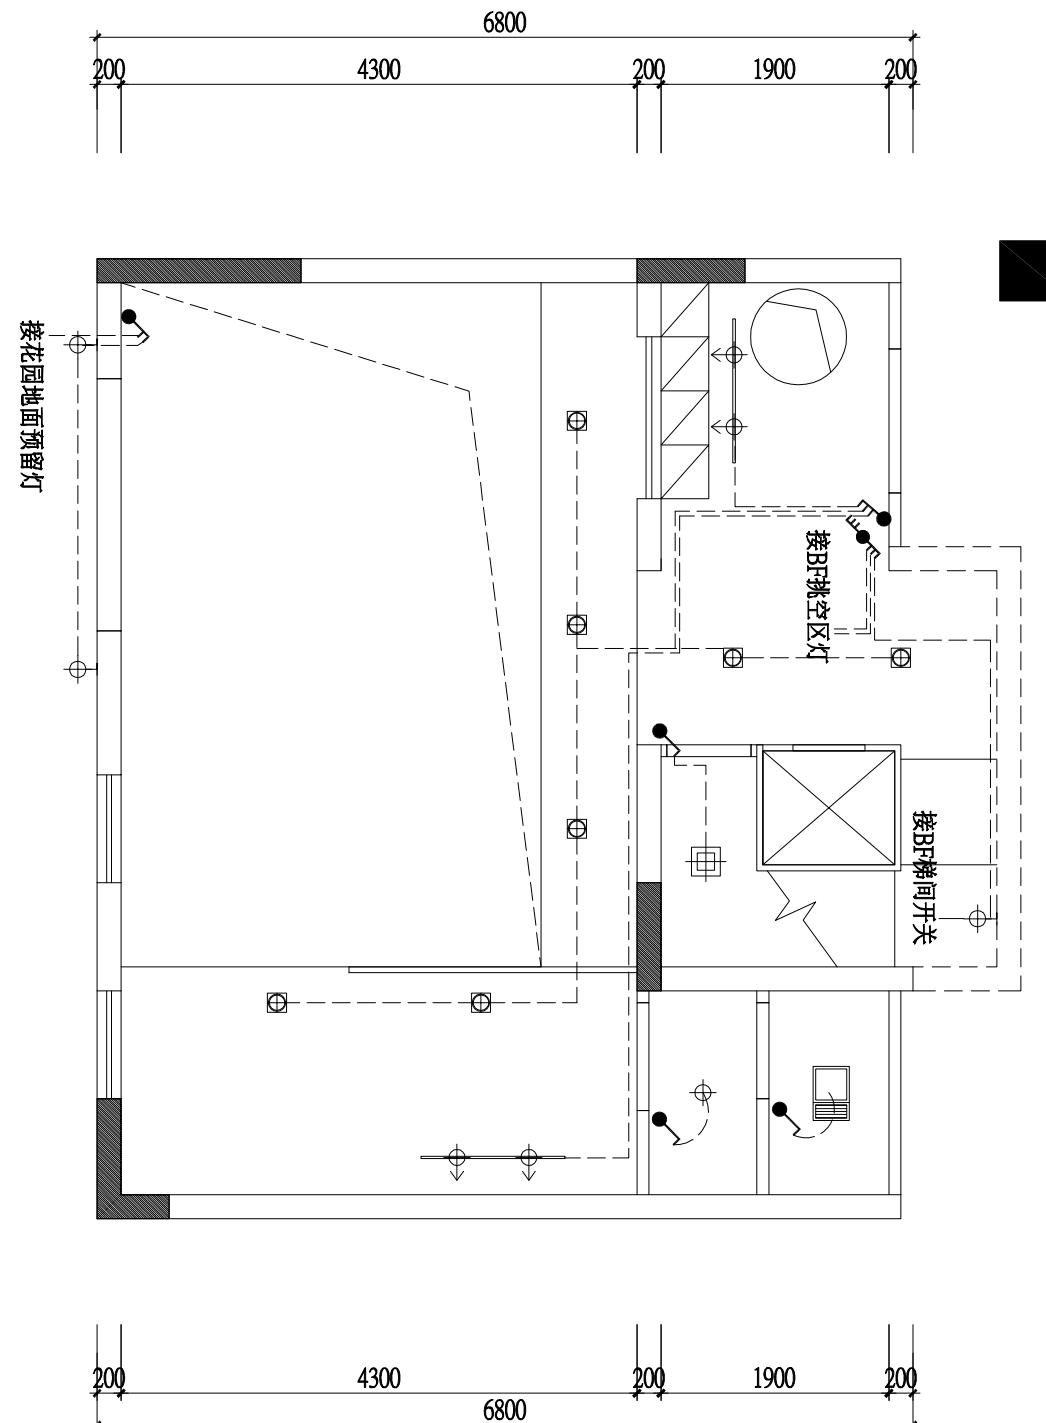

### 照明灯具说明：

图例	名称	图例	名称
● ↗	单联单控开关	↙ ●	单联双控+单联单控开关
● ↗ ↗	双联单控开关	↙ ↗ ●	双联双控开关
● ↗ ↗ ↗	三联单控开关	↙ ↗ ↗ ●	三联双控开关
↙ ↗ ↗ ↗	单联双控开关	■ AC	空调开关

注：开关盒面板间距20mm;所有标高为中性距地。

### -1F开关布置图


图号  
SHEET NO

-1F.P-10

是 境  
設 計  
計 言

10 -1F开关布置图  
SCALE:1:60



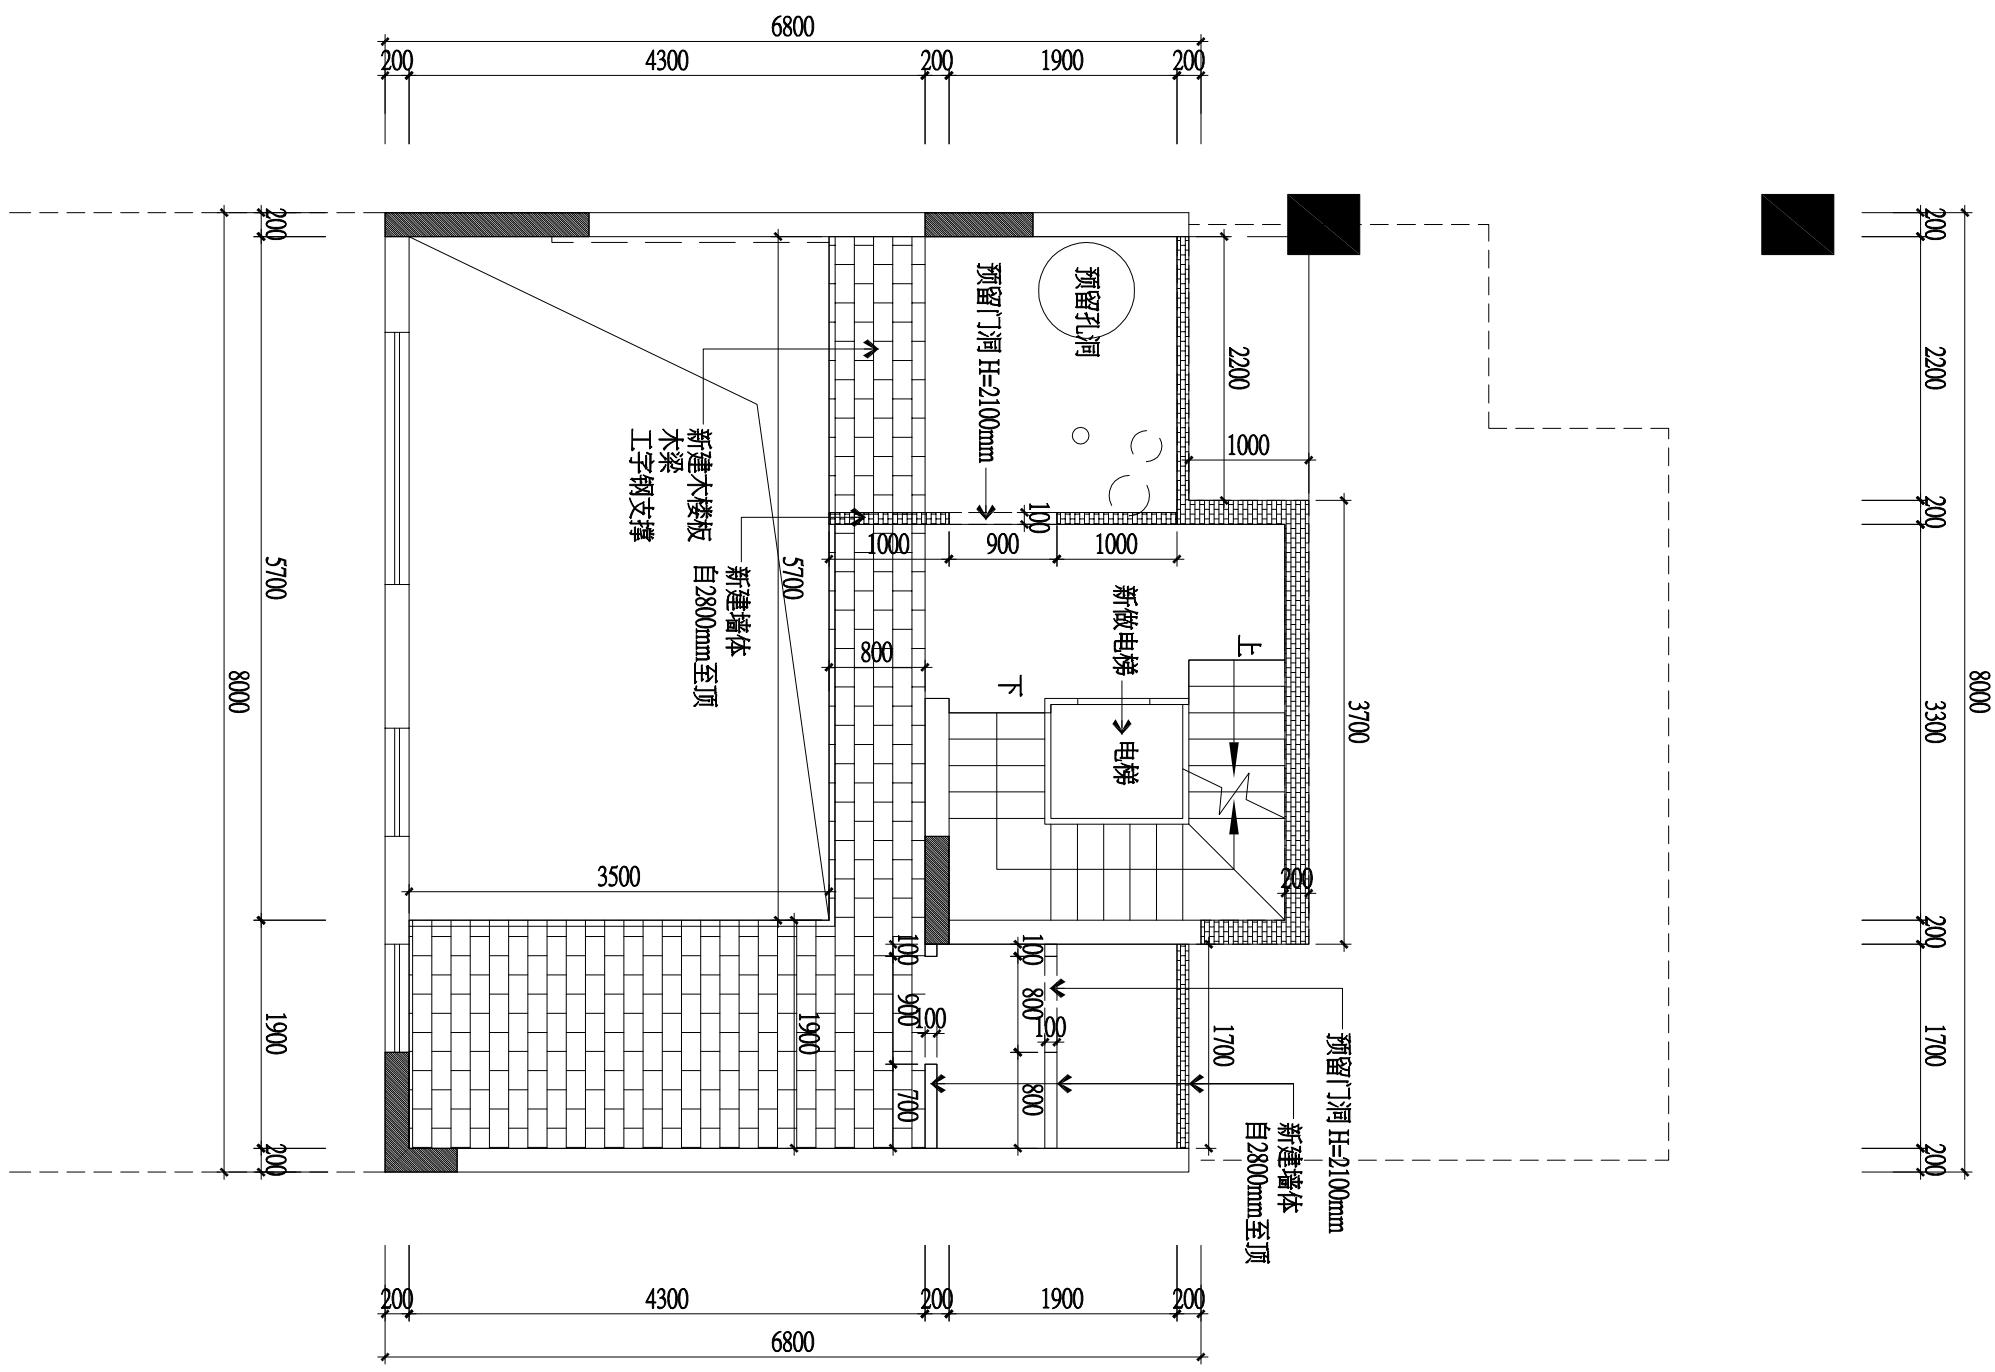

备注  
NOTE

---

Page 1

— 1 —

卷之三


四

2

四

— 6 —

1

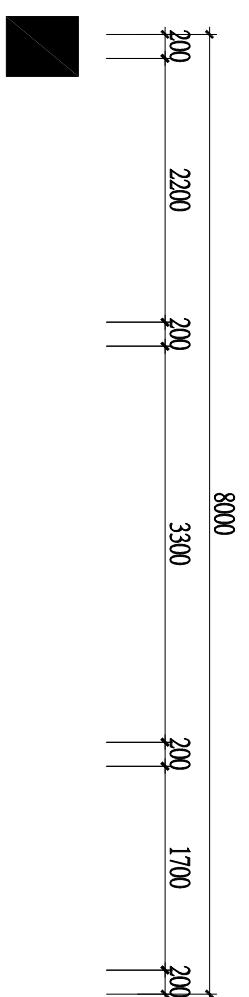

备  
注  
NOTE

□在未经同意前，不得复制图纸及其设计任何部分。

□所有图纸尺寸标注须在实际工地复核及量度。

□请勿按比例量度图纸，应采用已标明的尺寸。

□本图纸必须和现场说明、合同条款及其他有关图纸，并使用，如发现图纸内容有不符之处，必须立刻通知设计师。

业  
主  
CLIENT

项  
目  
名  
称  
PROJECT

龙湖椿山

总  
负  
责  
PRINCIPAL

设  
计  
DESIGNER

绘  
图  
DRAWN BY

校  
对  
COLLATE

审  
核  
APPROVE

比  
例  
SCALE 1 : 60


日  
期  
DATE 2020.07

图  
名  
DRAWING TITLE

BFA平面布置图

图  
号  
SHEET NO

B.F.P-03

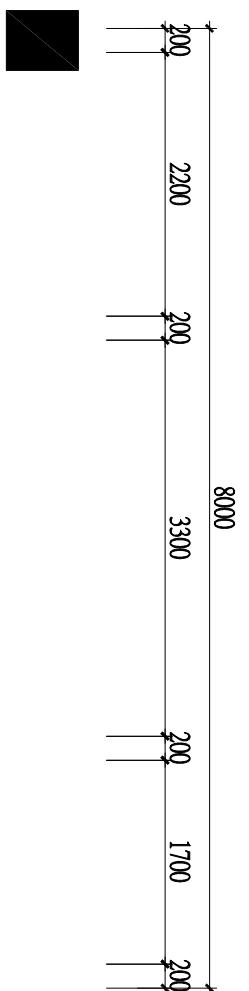

备  
注  
NOTE

□在未经同意前，不得复制图纸及其设计任何部分。

□所有图纸尺寸标注须在实际工地复核及量度。

□请勿按比例量度图纸，应采用已标明的尺寸。

□本图纸必须和现场说明、合同条款及其他有关图纸，并使用，如发现图纸内容有不符之处，必须立刻通知设计师。

业  
主  
CLIENT

项  
目  
名  
称  
PROJECT

龙湖椿山

总  
负  
责  
PRINCIPAL

设  
计  
DESIGNER

绘  
图  
DRAWN BY

校  
对  
COLLATE

审  
核  
APPROVE

比  
例  
SCALE


日  
期  
DATE

图  
名  
DRAWING TITLE

BF隔墙尺寸图

图  
号  
SHEET NO

BF.P-04

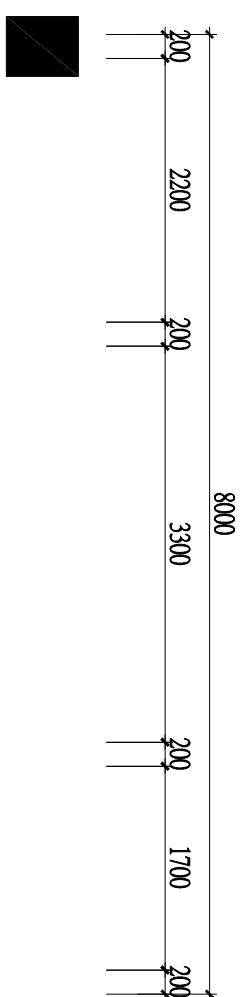

备  
注  
NOTE

□在未经同意前，不得复制图纸及其设计任何部分。  
□所有图纸尺寸标注须在实际工地上复核及量度。  
□请勿按比例量度图纸，应采用已标明的尺寸。

□本图纸必须和现场说明、合同条款及其他有关图纸，并使用，如发现图纸内容有不符之处，必须立刻通知设计师。

业  
主  
CLIENT

项  
目  
名  
称  
PROJECT

总  
负  
责  
人  
PRINCIPAL

设  
计  
师  
DESIGNER

绘  
图  
DRAWM BY

校  
对  
COLLATE

审  
核  
APPROVE

比  
例  
SCALE

日  
期  
DATE

图  
名  
DRAWING TITLE


BF.P-05

图  
号  
SHEET NO

BF地  
面  
材  
质  
图

是  
境  
設  
計



05  
BF地  
面  
材  
質  
圖  
SCALE:1:60

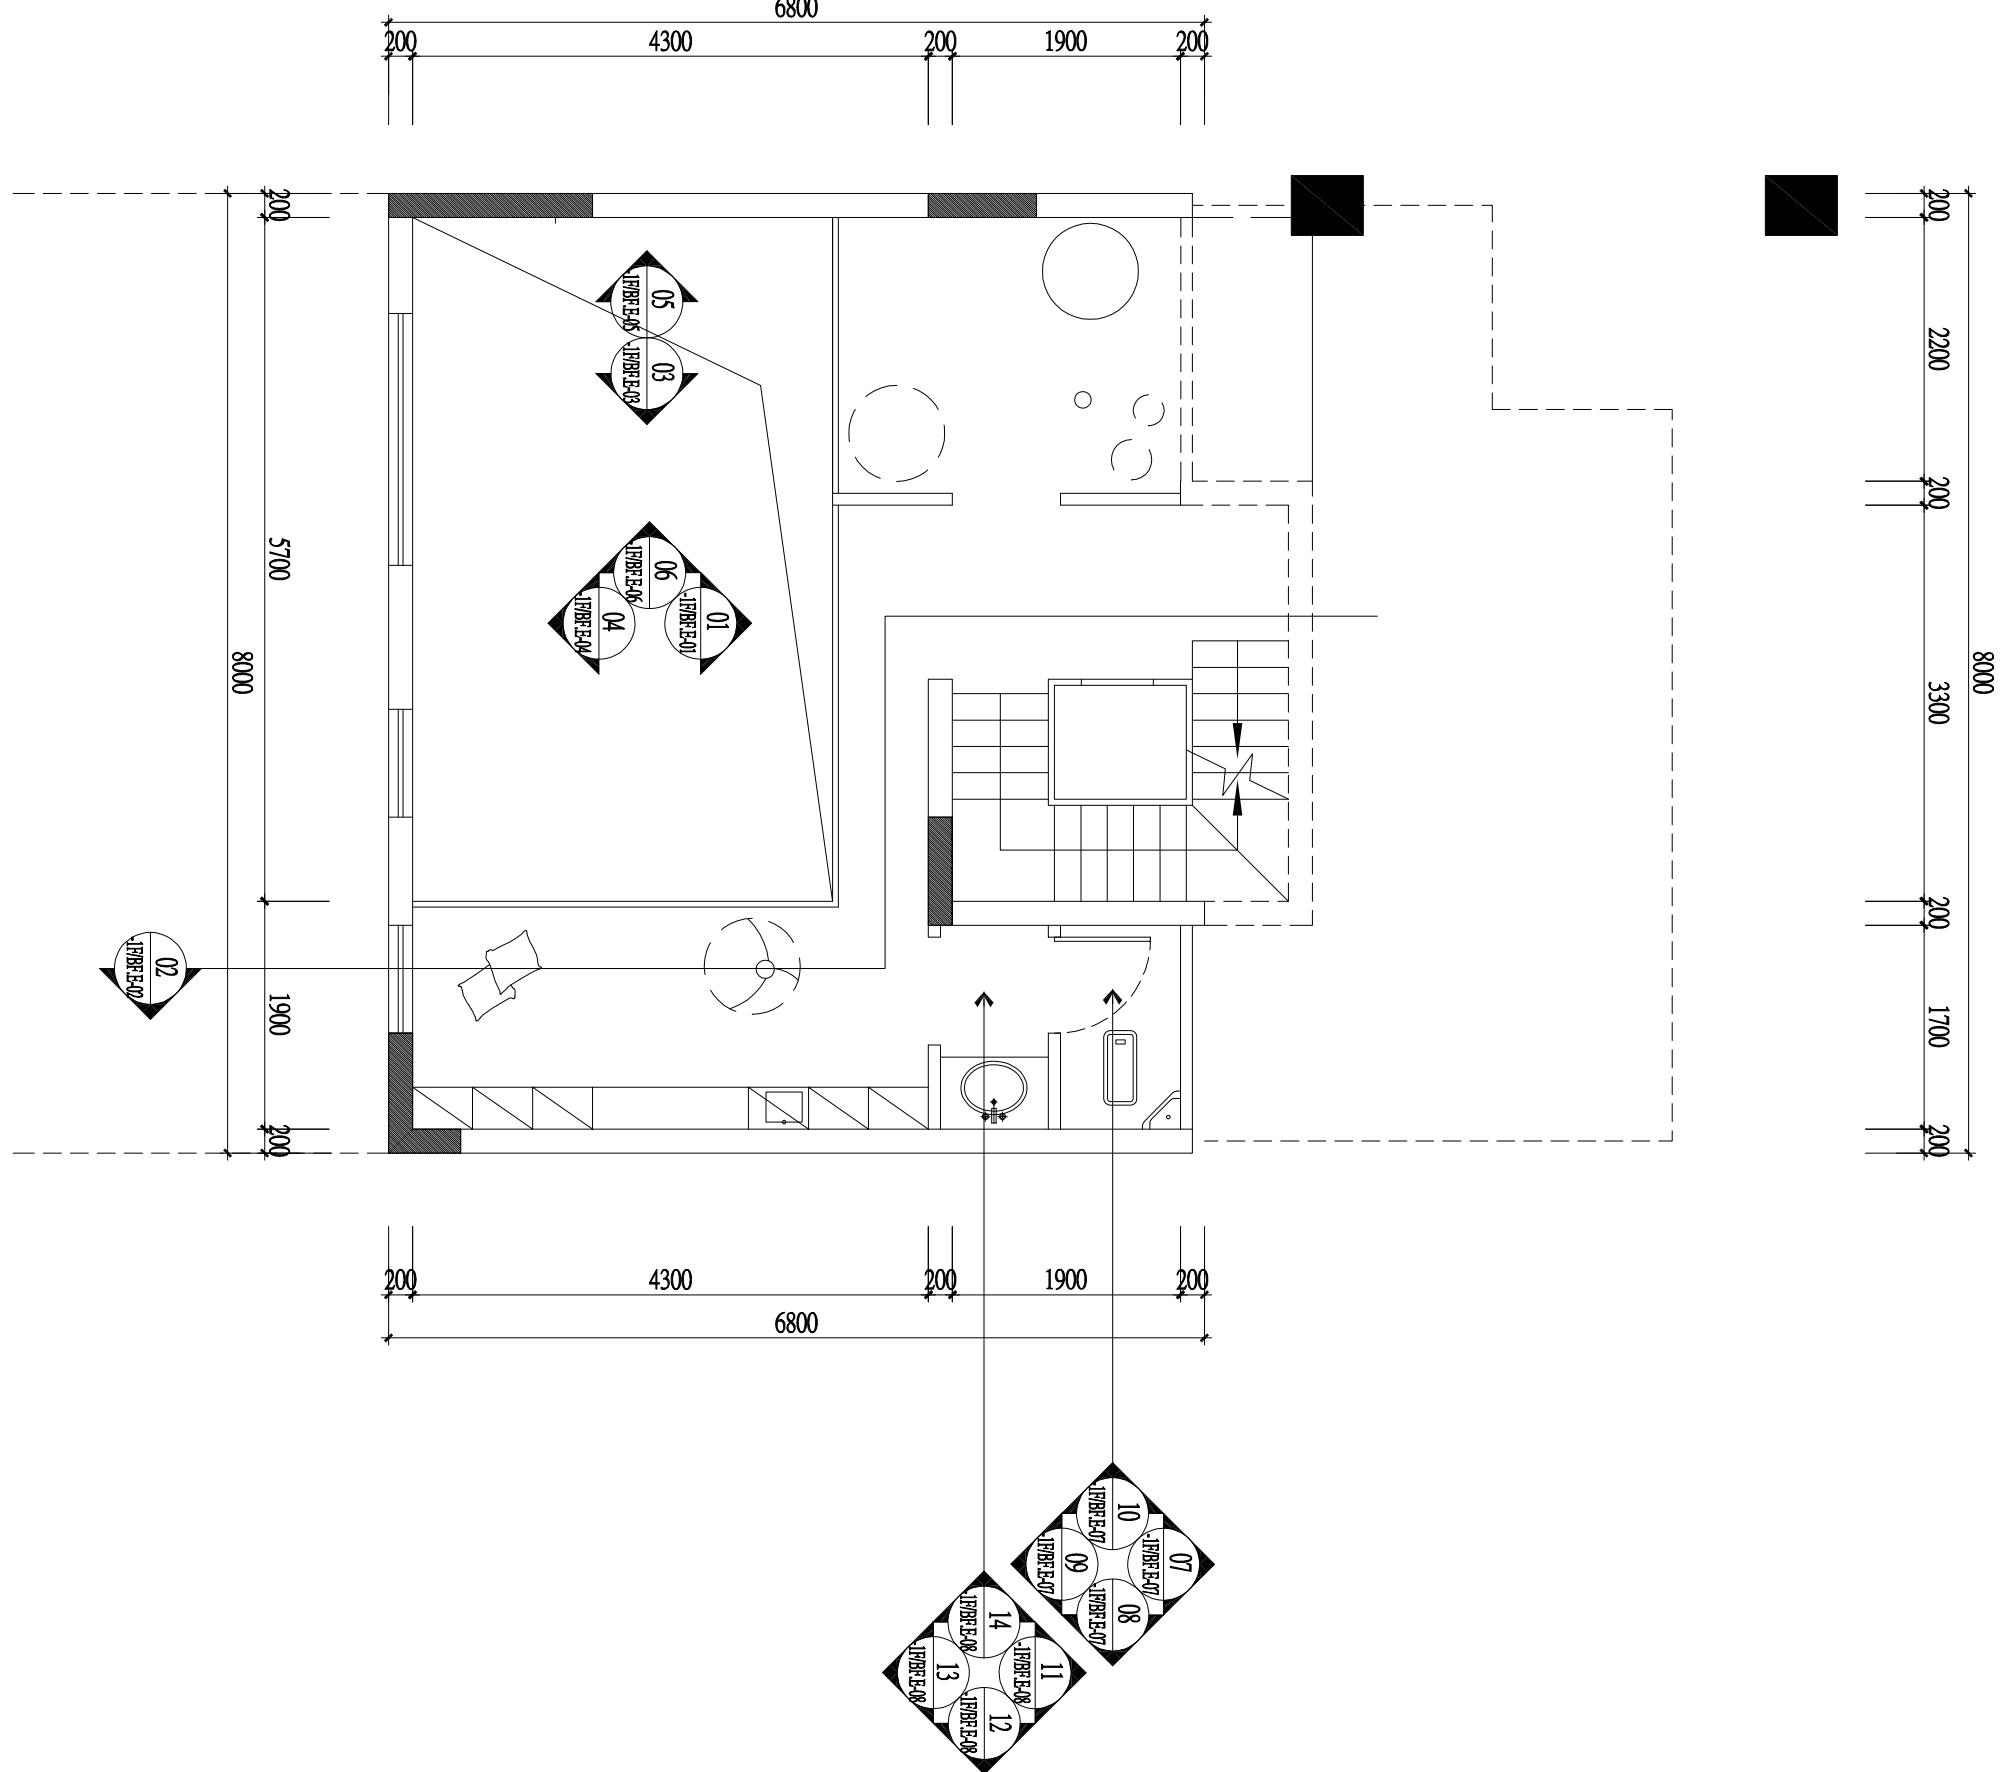

<p><b>业 主</b></p> <p>CLIENT</p>	<p><b>备 注</b></p> <p>NOTE</p> <p>□在未经同意前，不得复制图纸及其设计 任何部份。</p> <p>□所有图纸尺寸标注须在实际工地上复核及 量度。</p> <p>□请勿按比例量度图纸，应采用已标明的 尺寸。</p> <p>□本图纸必须和规格说明、合同条款及其 有关图纸一并使用，如发现图纸内容 有不符之处，必须立刻通知设计院。</p>
---------------------------------	--

# 是境設計

- 06 = BF立面索引圖  
SCALE:1/60

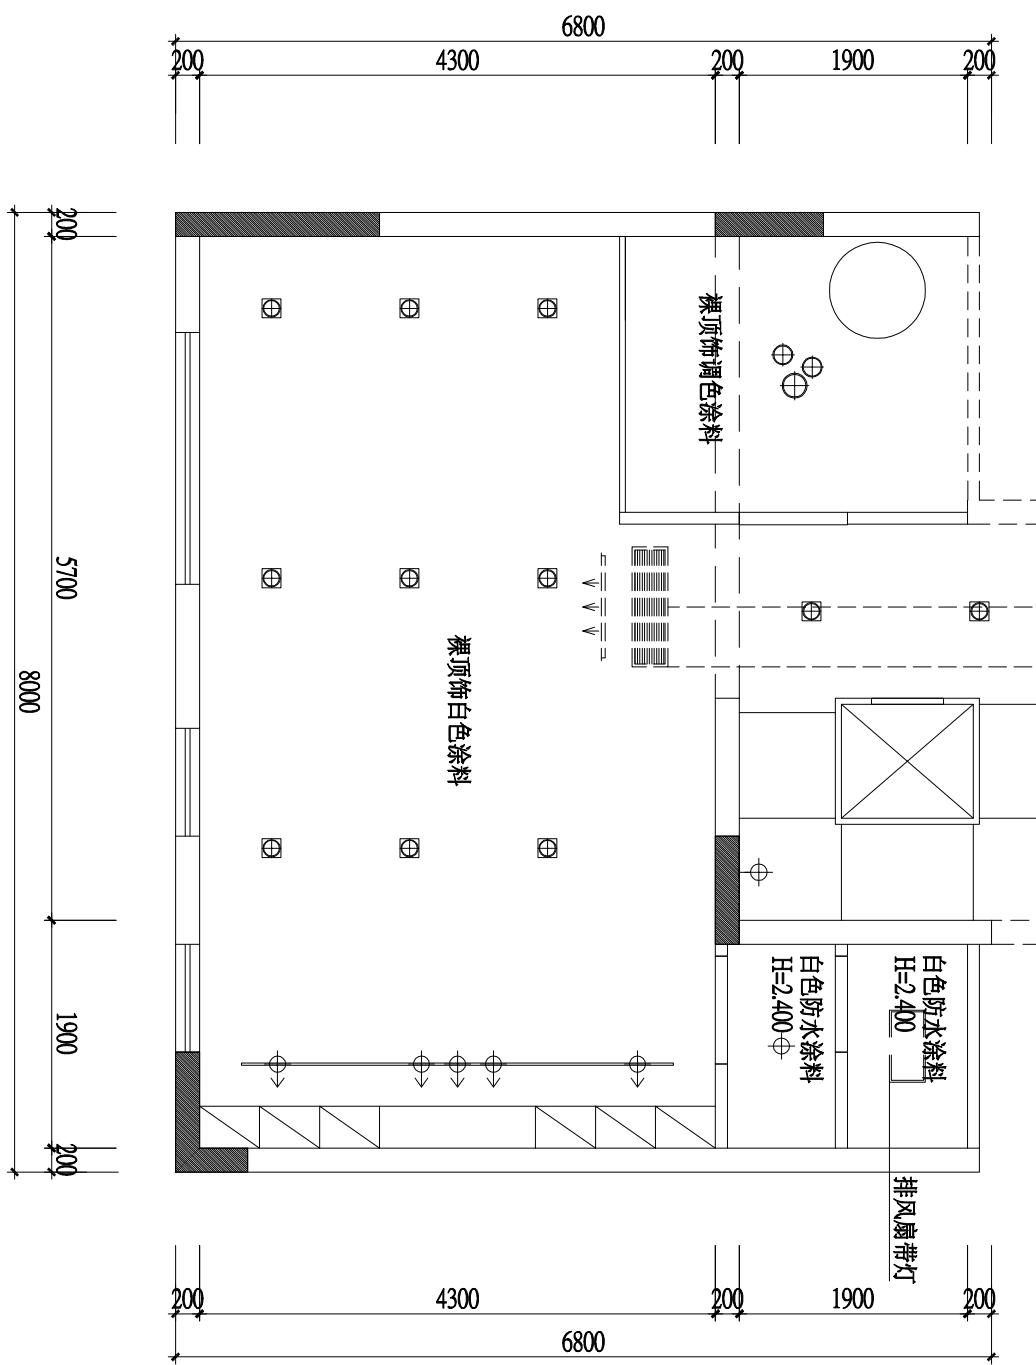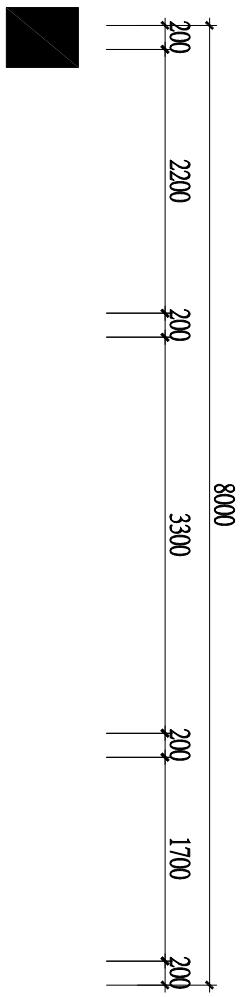

**照明灯具说明：**

图例	名称	图例	名称
⊕	明装筒灯	——	暗藏式灯带
+	防潮筒灯	⊕	壁灯
↑	轨道射灯	⊕⊕	艺术吊灯
⊕	嵌入式筒灯	串	吸顶灯

BF天花布置图

图号  
SHEET NO  
BF.P-07

是境  
设计

07 BF天花布置图  
SCALE:1:60

备注  
NOTE  
①本图未经同意，不得复制图纸及其设计任何部分。  
②所有图纸尺寸标注须在实际工地复核及量度。  
③请勿按比例量度图纸，应采用已标明的尺寸。

④本图纸必须和规格说明、合同条款及其他有关图纸，并使用，如发现图纸内容有不符之处，必须立刻通知设计师。  
⑤请勿按比例量度图纸，应采用已标明的尺寸。

业 主  
CLIENT

项目名称  
PROJECT  
龙湖椿山

总负责人  
PRINCIPAL

设计  
DESIGNER

绘图  
DRAWN BY



校对  
COLLATE

审核  
APPROVE

比例  
SCALE

日期  
DATE

图名  
DRAWING TITLE  
BF天花布置图

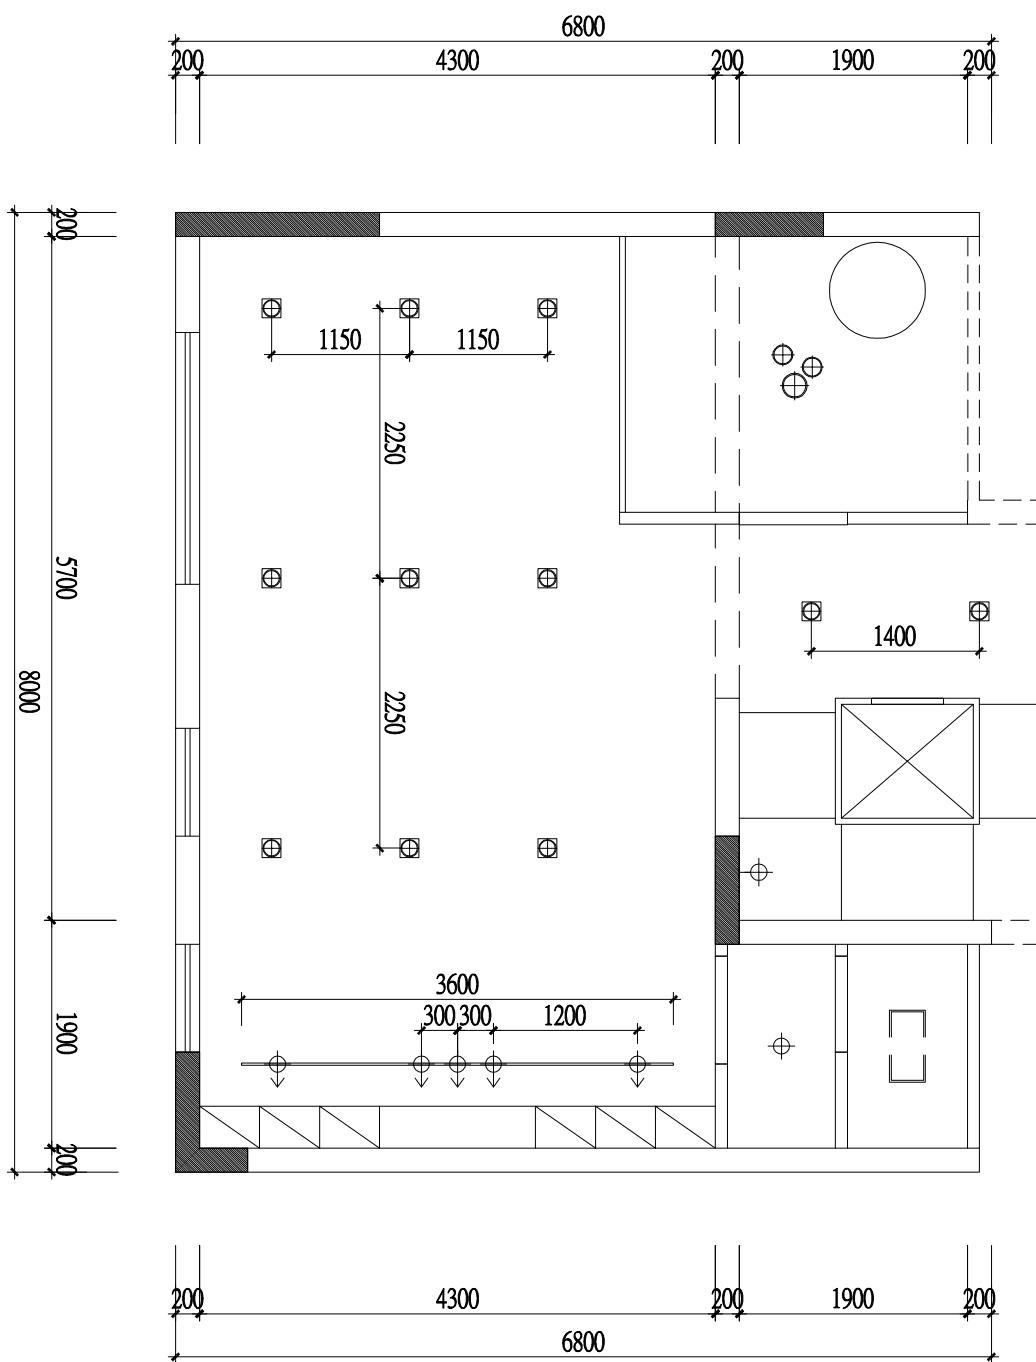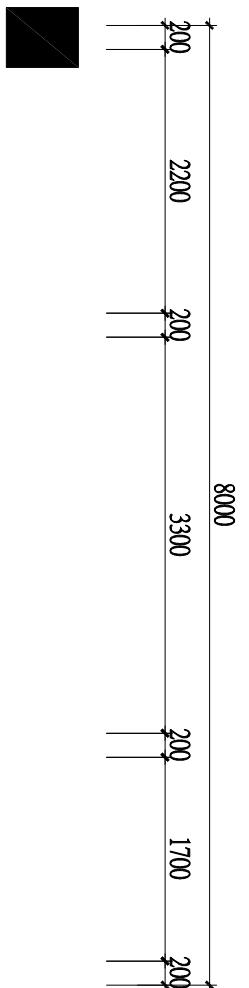

照明灯具说明：

图例	名称	图例	名称
⊕	明装筒灯	——	暗藏式灯带
+	防潮筒灯	⊕	壁灯
↑	轨道射灯	⊕⊕	艺术吊灯
⊕	嵌入式筒灯	串	吸顶灯

是  
境  
設  
計

08 BF天花尺寸图  
SCALE:1:60

图号  
SHEET NO  
BF.P-08

图名  
DRAWING TITLE  
BF天花尺寸图

备注  
NOTE  
□本图版必须和规格说明、合同条款及其  
他有关图纸，并使用，如发现图纸内容  
有不符之处，必须立刻通知设计者。

□本图版必须和规格说明、合同条款及其  
他有关图纸，并使用，如发现图纸内容  
有不符之处，必须立刻通知设计者。

业主  
CLIENT

项目名称  
PROJECT

总负责人  
PRINCIPAL

设计师  
DESIGNER

绘图  
DRAWN BY


校对  
COLLATE

审核  
APPROVE



核对  
COLLATE

比例  
SCALE

日期  
DATE

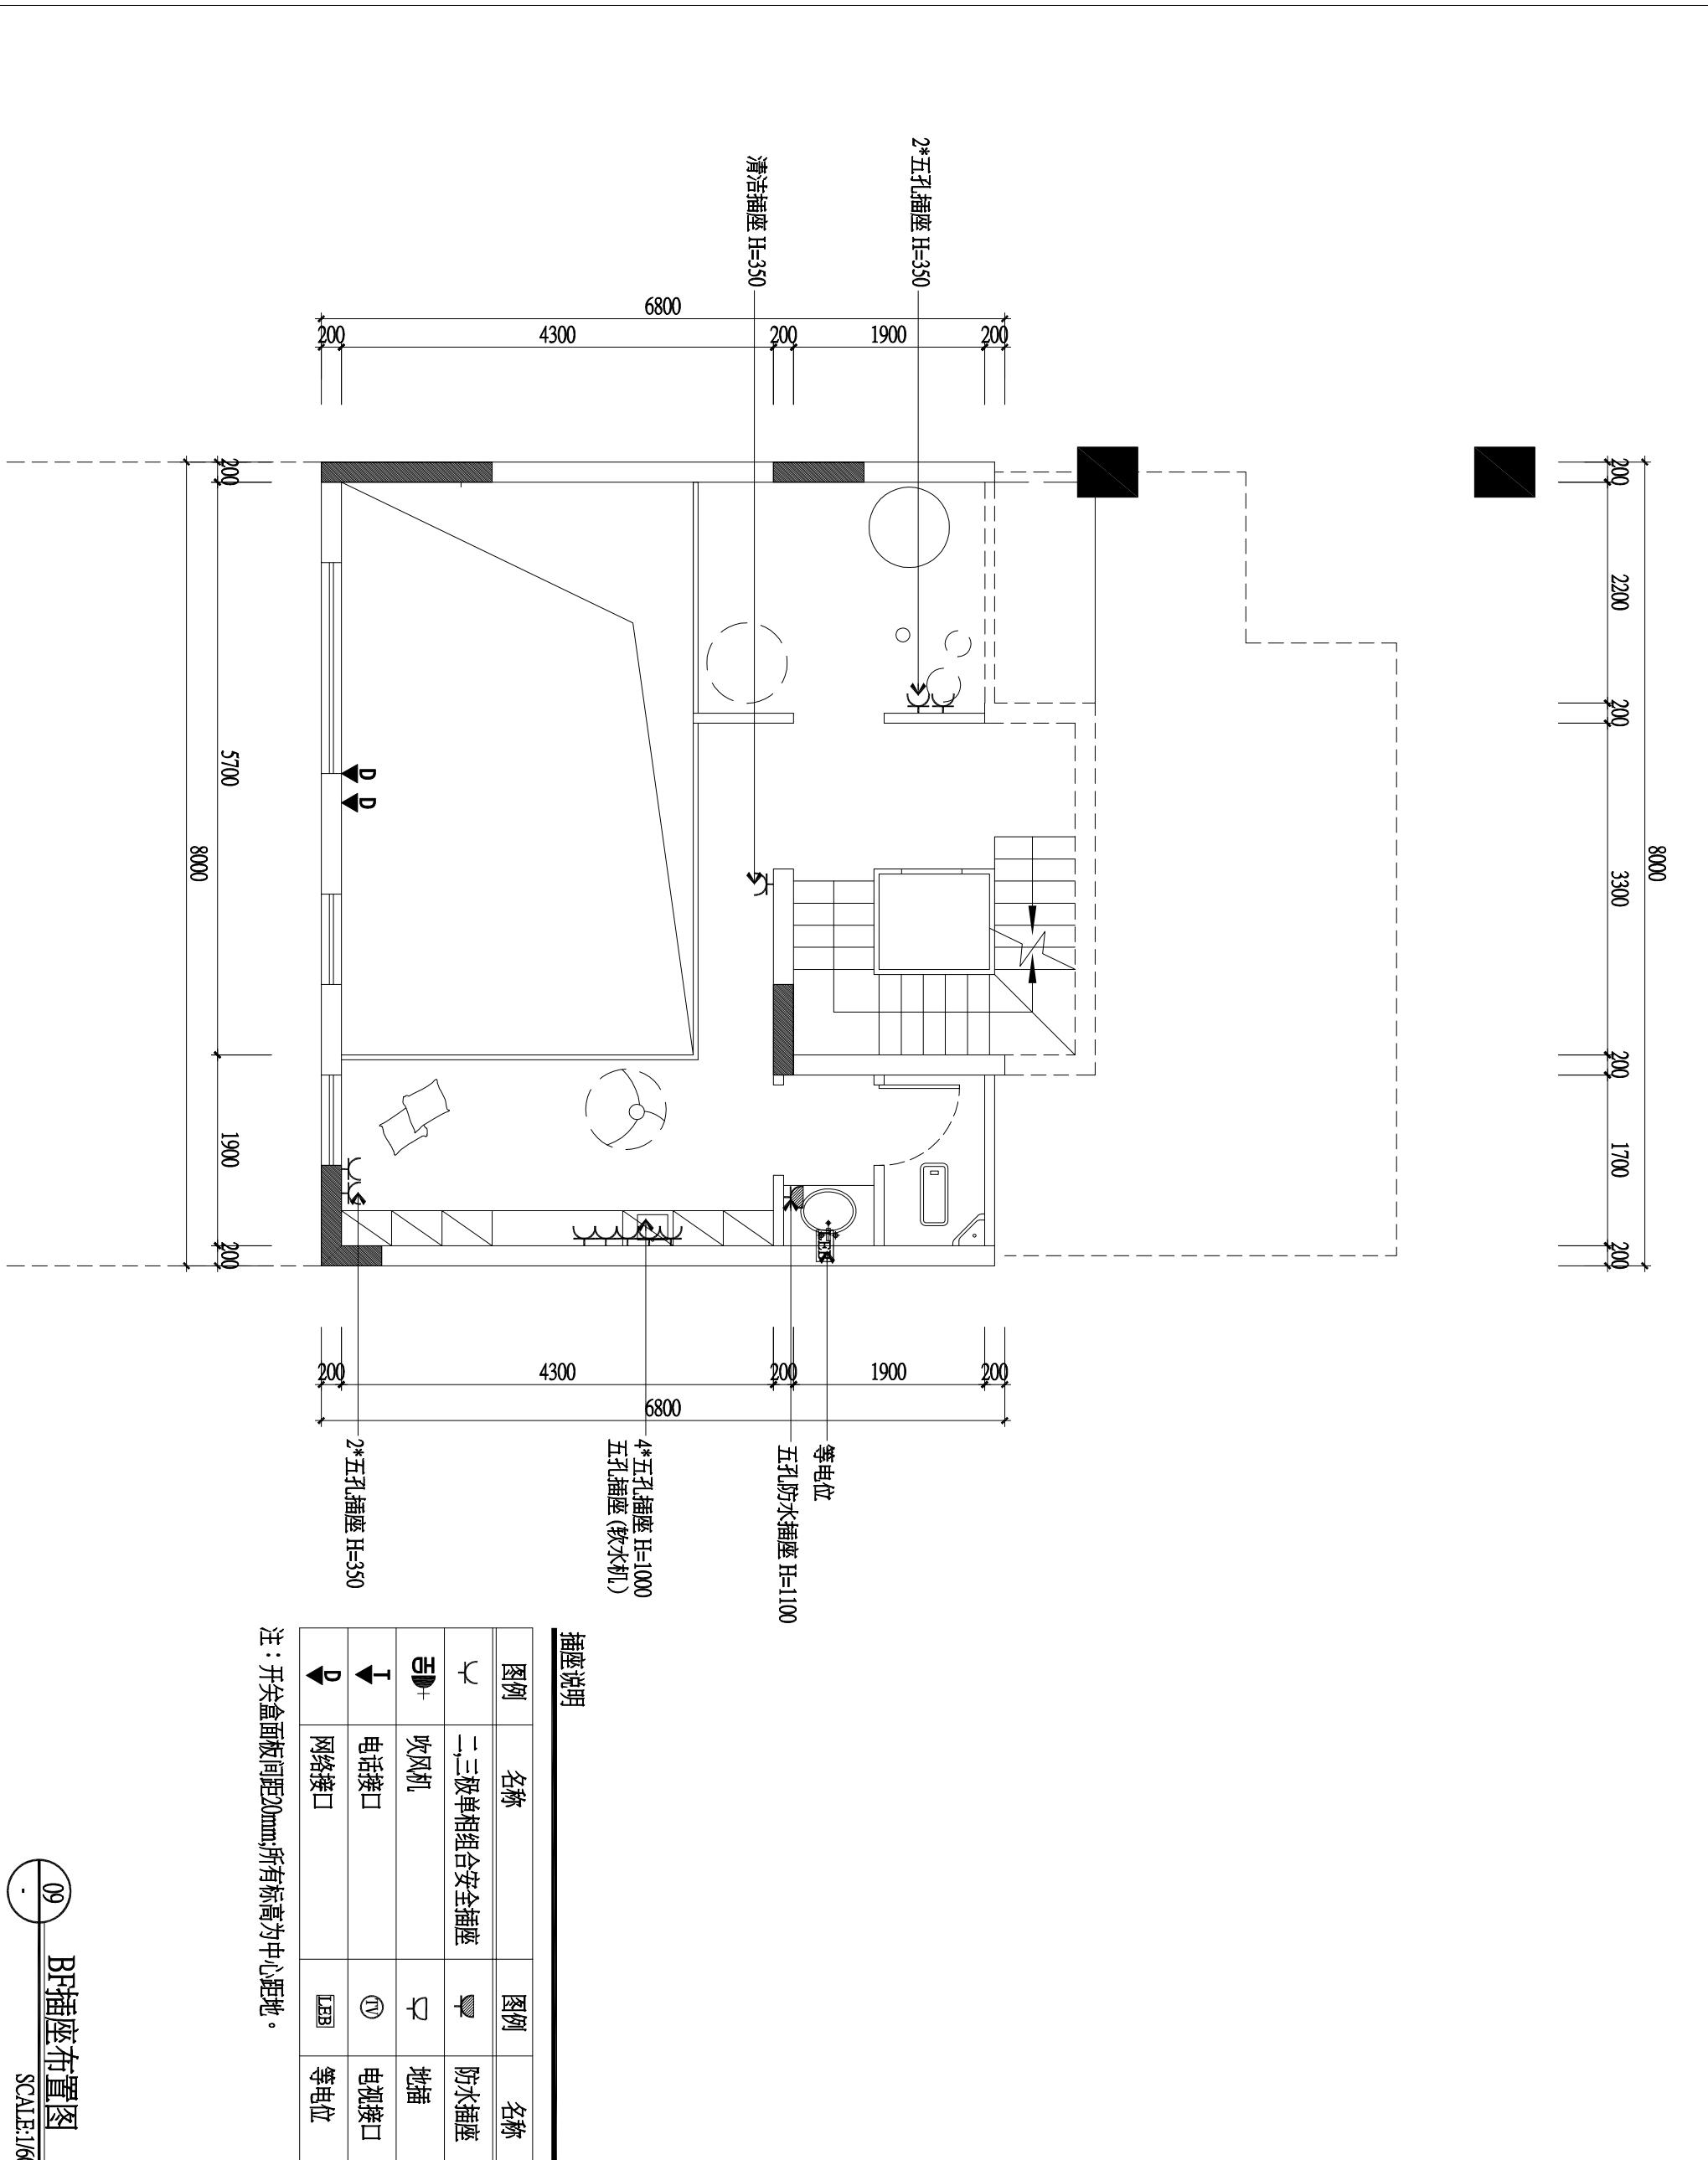

<p><b>项目名称</b> PROJECT</p>	<p><b>备注</b> NOTE</p>
<p><b>业主</b> CLIENT</p>	<p>□在未经同意前，不得复制图纸及其设计 任何部份。 □所有图纸尺寸标注须在实际工地上复核及 量度。 □请勿按比例量度图纸，应采用已标明的 尺寸。 □本图纸必须和规格说明、合同条款及其 他有关图纸一并使用，如发现图纸内容 有不妥之处，必须立刻通知设计师。</p>

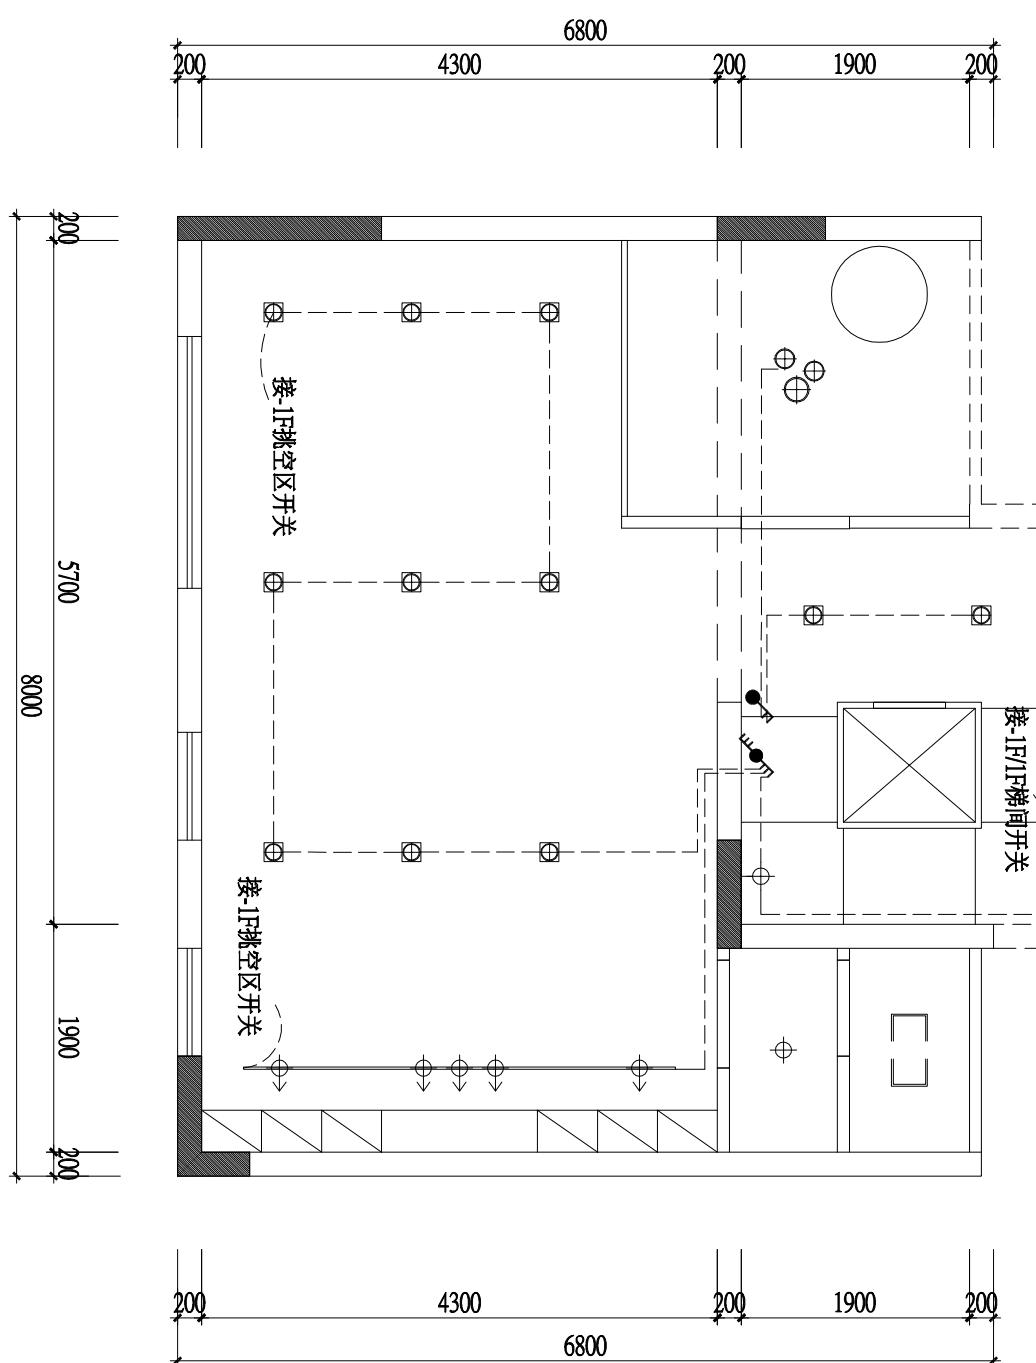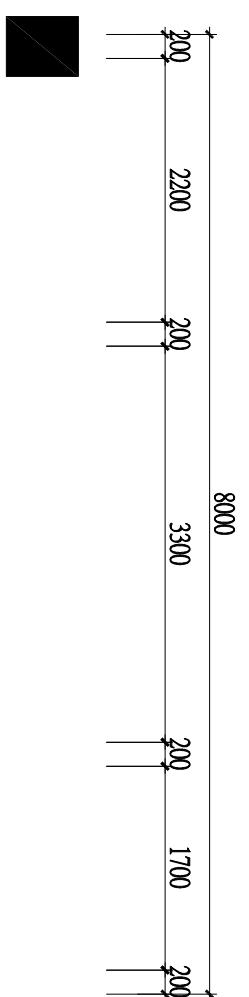

注：开关盒面板间距20mm;所有标高为中距地。

#### 照明灯具说明：


图例	名称	图例	名称
● ↗	单联单控开关	↙ ●	单联双控+单联单控开关
● ↗ ↗	双联单控开关	↙ ↗ ●	双联双控开关
● ↗ ↗ ↗	三联单控开关	↙ ↗ ↗ ●	三联双控开关
↙ ↗ ↗ ↗	单联双控开关	■ AC	空调开关

BF开关布置图

图号 SHEET NO  
BF.P-10

是境  
设计

备 注  
NOTE  
□ 本图未经同意，不得复制图纸及其设计任一部分。  
□ 所有图纸尺寸标注须在实际工地上复核及量度。  
□ 请勿按比例量度图纸，应采用已标明的尺寸。  
□ 本图纸必须和规格说明、合同条款及其他有关图纸一并使用。如发现图纸内容有不符之处，必须立刻通知设计者。

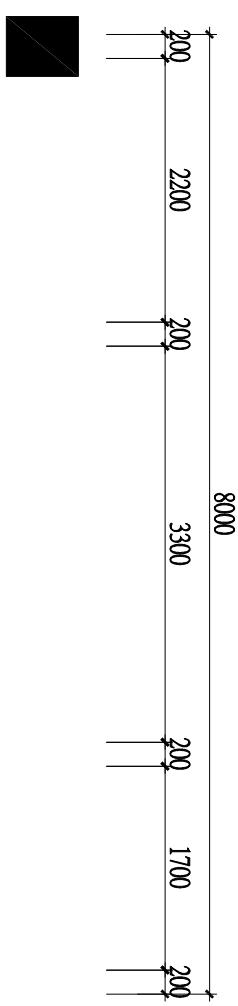

备注  
NOTE  
□ 未经同意，不得复制图纸及其设计任何部分。  
□ 所有图纸尺寸标注须在实际工地复核及量度。  
□ 请勿按比例量度图纸，应采用已标明的尺寸。  
□ 本图纸必须和现场说明、合同条款及其他有关图纸一并使用。如发现图纸内容有不符之处，必须立刻通知设计师。

业 主  
CLIENT

项 目 名 称  
PROJECT

总 负 责  
PRINCIPAL

设 计  
DESIGNER

绘 图  
DRAWN BY

校 对  
COLLATE

审 核  
APPROVE

比 例  
SCALE

日 期  
DATE

图 名  
DRAWING TITLE

给排水说明：

图例	名称	图例	名称
●	给水口	①	墙排水
⊗	热水上水口	——	热水管
●	排水口	——	给水管
◎	马桶排水口	△	热水器

注：室内水管均从梁底走，冷热水管直径25mm，排水管直径50mm。

BF水路布置图

图 号  
SHEET NO


BF.P-11

是 境  
設 計

11 BF水路布置图  
SCALE:1:60

备  
注  
NOTE  
□在未经同意前，不得复制图纸及其设计  
任何部分。  
□所有图纸尺寸标注须在实际工地上复核及  
量度。  
□请勿按比例量度图纸，应采用已标明的  
尺寸。

□本图纸必须和规格说明、合同条款及其  
他有关图纸，并使用、如发现图纸内容  
有不符之处，必须立刻通知设计者。

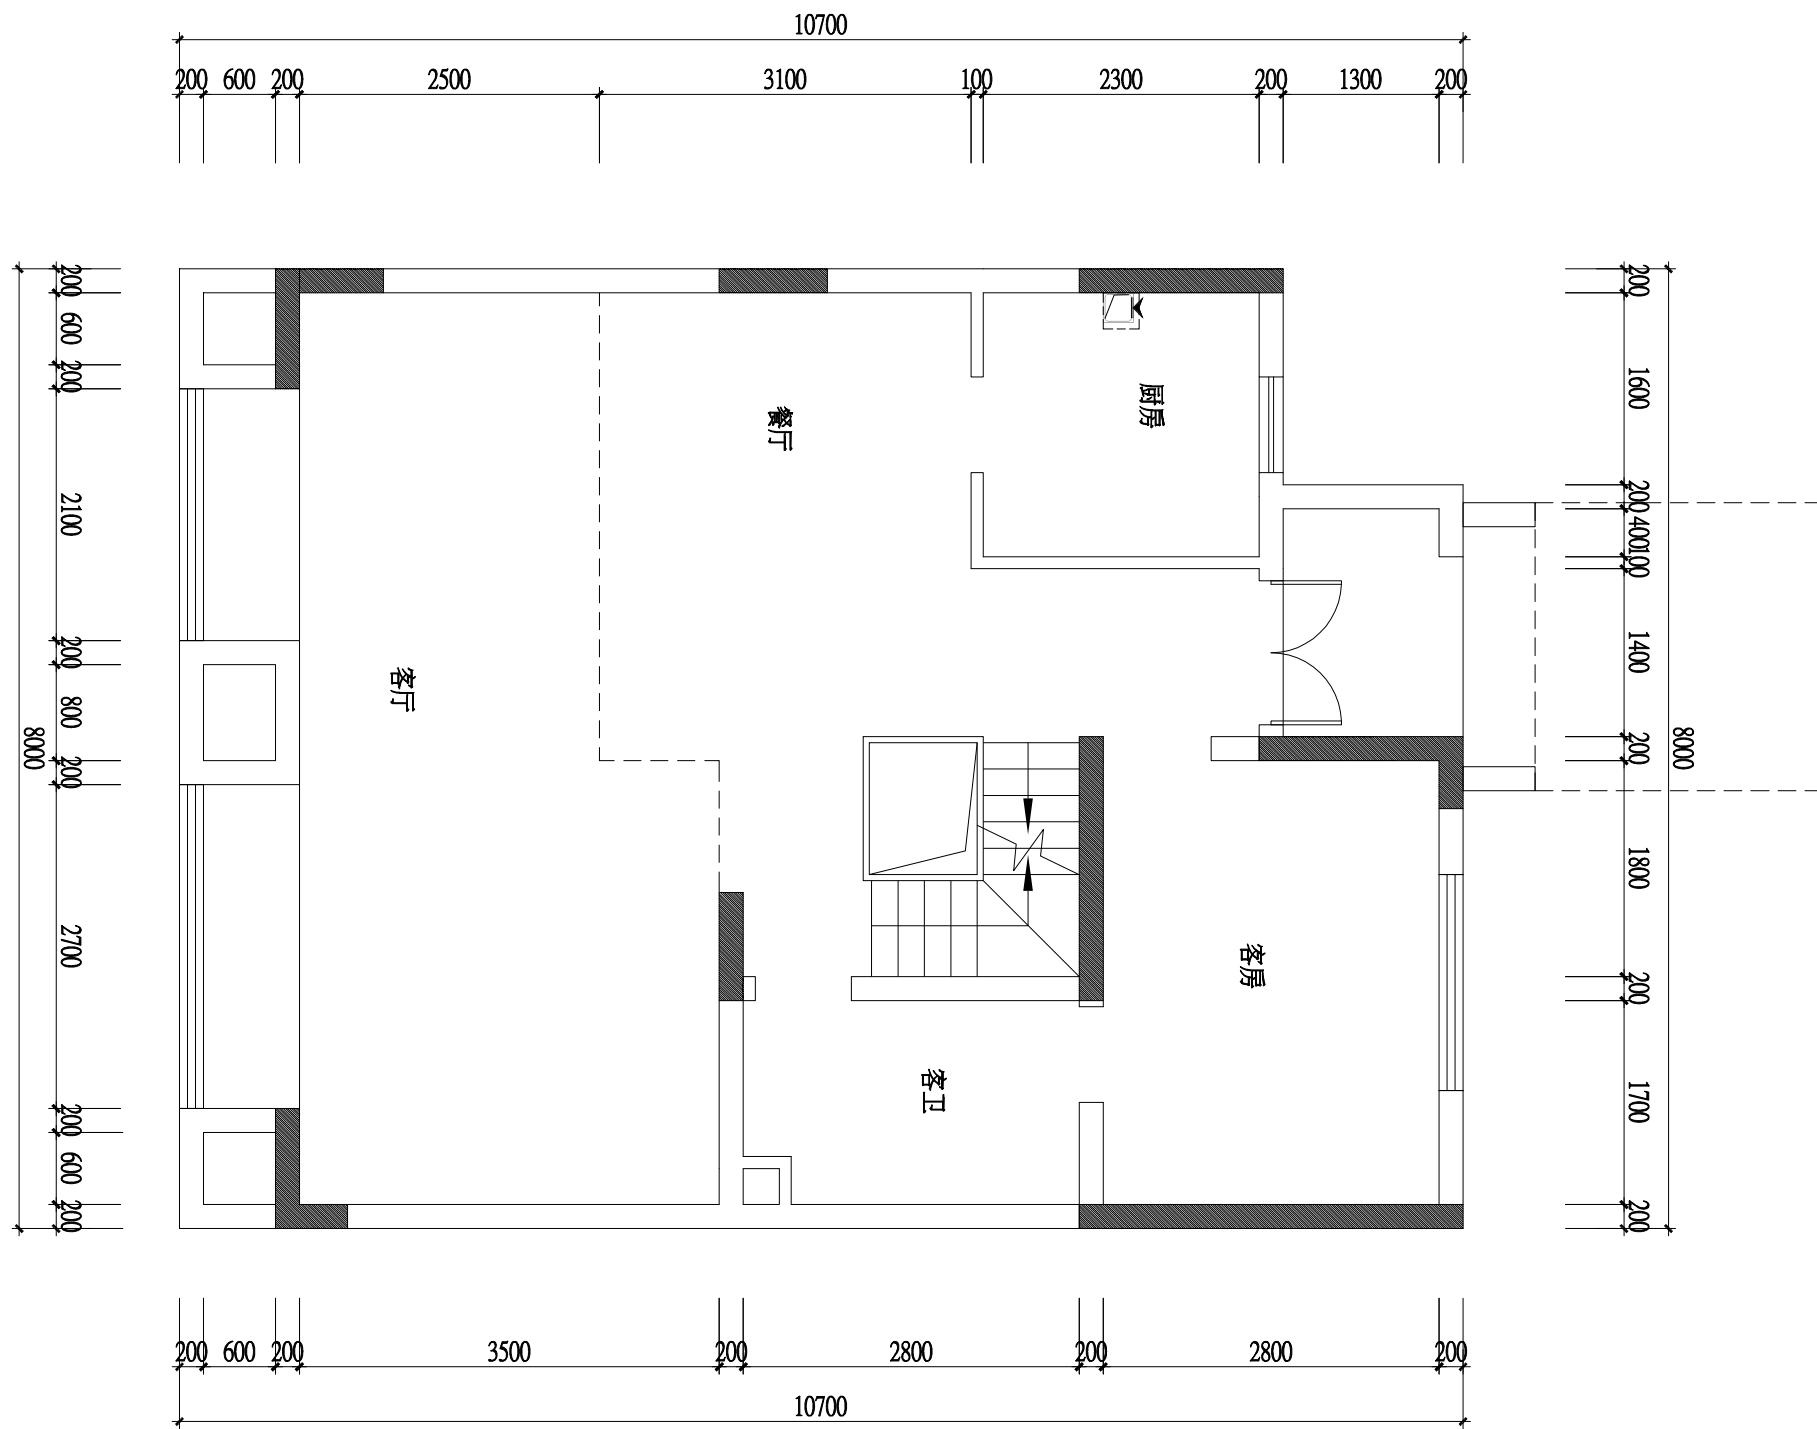

00 1F原始平面图  
SCALE:1:60

是境  
設計  
設計

1F原始平面图

图号  
SHEET NO

1F.P-00

项目名称 PROJECT	龙湖椿山
总负责人 PRINCIPAL	
设计师 DESIGNER	
绘图图 DRAWN BY	
校对 COLLATE	
审核 APPROVE	
比例 SCALE	1 : 60
日期 DATE	2020.07
图名 DRAWING TITLE	

备  
注  
NOTE  
□在未经同意前，不得复制图纸及其设计  
任何部分。  
□所有图纸尺寸标注须在实际工地上复核及  
量度。  
□请勿按比例量度图纸，应采用已标明的  
尺寸。

□本图纸必须和规格说明、合同条款及其  
他有关图纸，并使用、如发现图纸内容  
有不符之处，必须立刻通知设计者。

业  
主  
CLIENT

项  
目  
名  
称  
PROJECT

龙湖椿山

总  
负  
责  
PRINCIPAL

设  
计  
DESIGNER

绘  
图  
DRAWN BY

校  
对  
COLLATE

校  
核  
COLLATE

审  
核  
APPROVE

比  
例  
SCALE 1 : 60

日  
期  
DATE 2020.07

图  
名  
DRAWING TITLE


1F墙体拆除图

图  
号  
SHEET NO


1F.P-01

是  
境  
設  
計

01 1F墙体拆除图  
SCALE:1:60

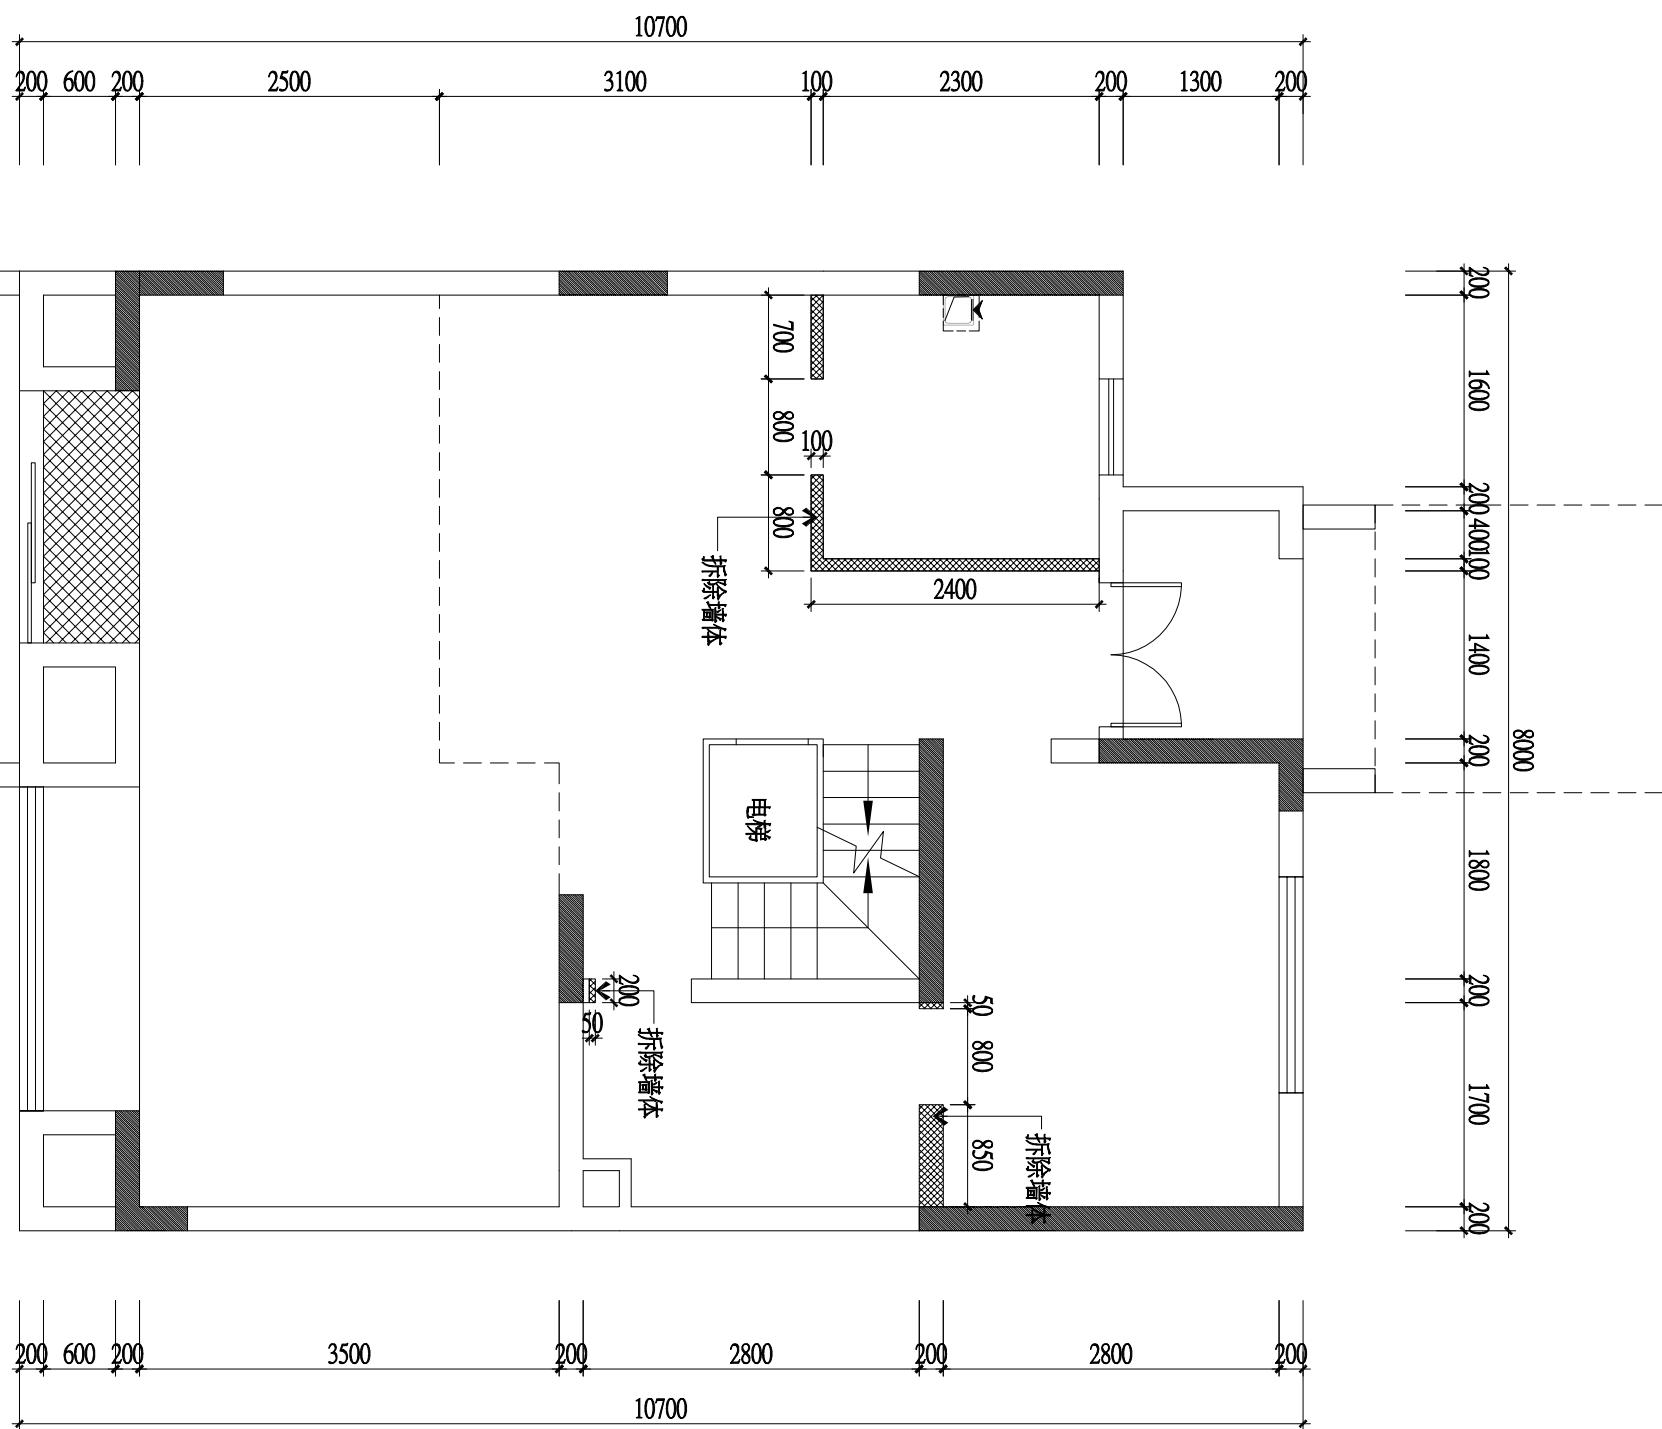




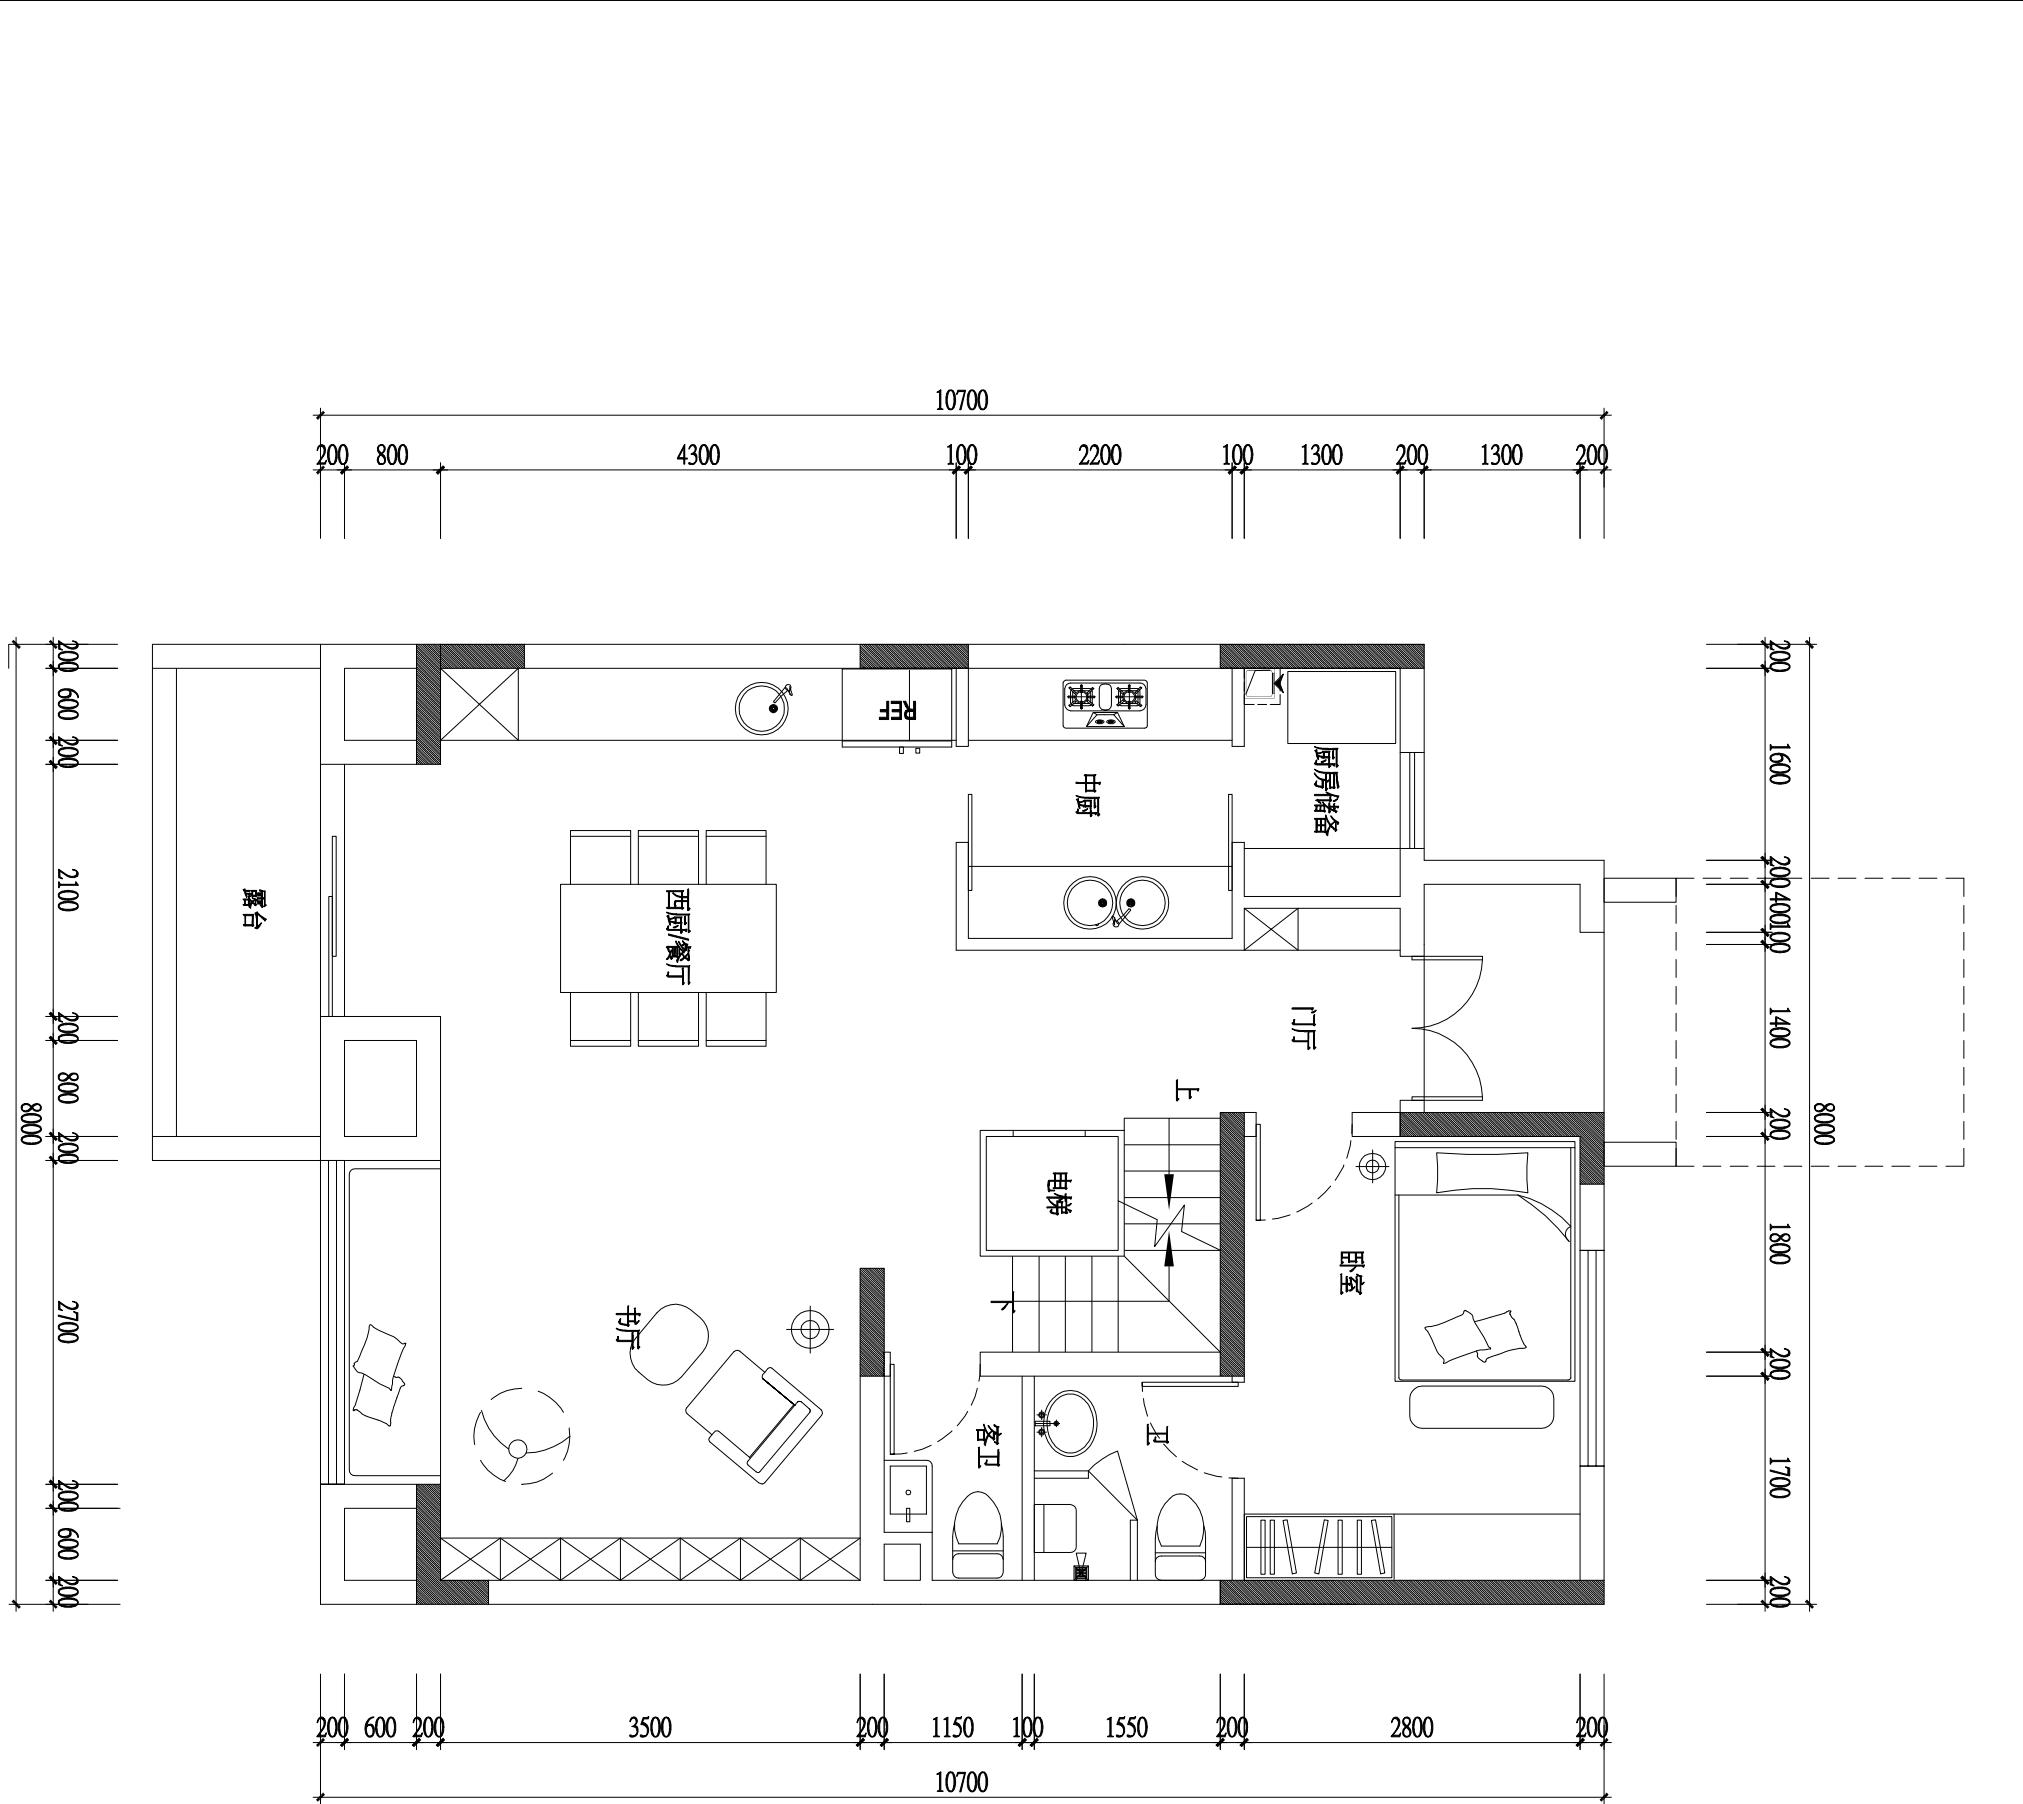

□在未经同意前，不得复制图纸及其设计  
NOTE

□ 所有图纸尺寸标注须在实际工地上复核及 量度。	
□ 请勿按比例重叠图纸，应采用已标明的 尺寸。	
项 目 名 称 PROJECT	龙湖精工
总 负 责 PRINCIPAL	
设 计 DESIGNER	
绘 图 DRAWN BY	
校 对 COLLATE	

# 是境設計

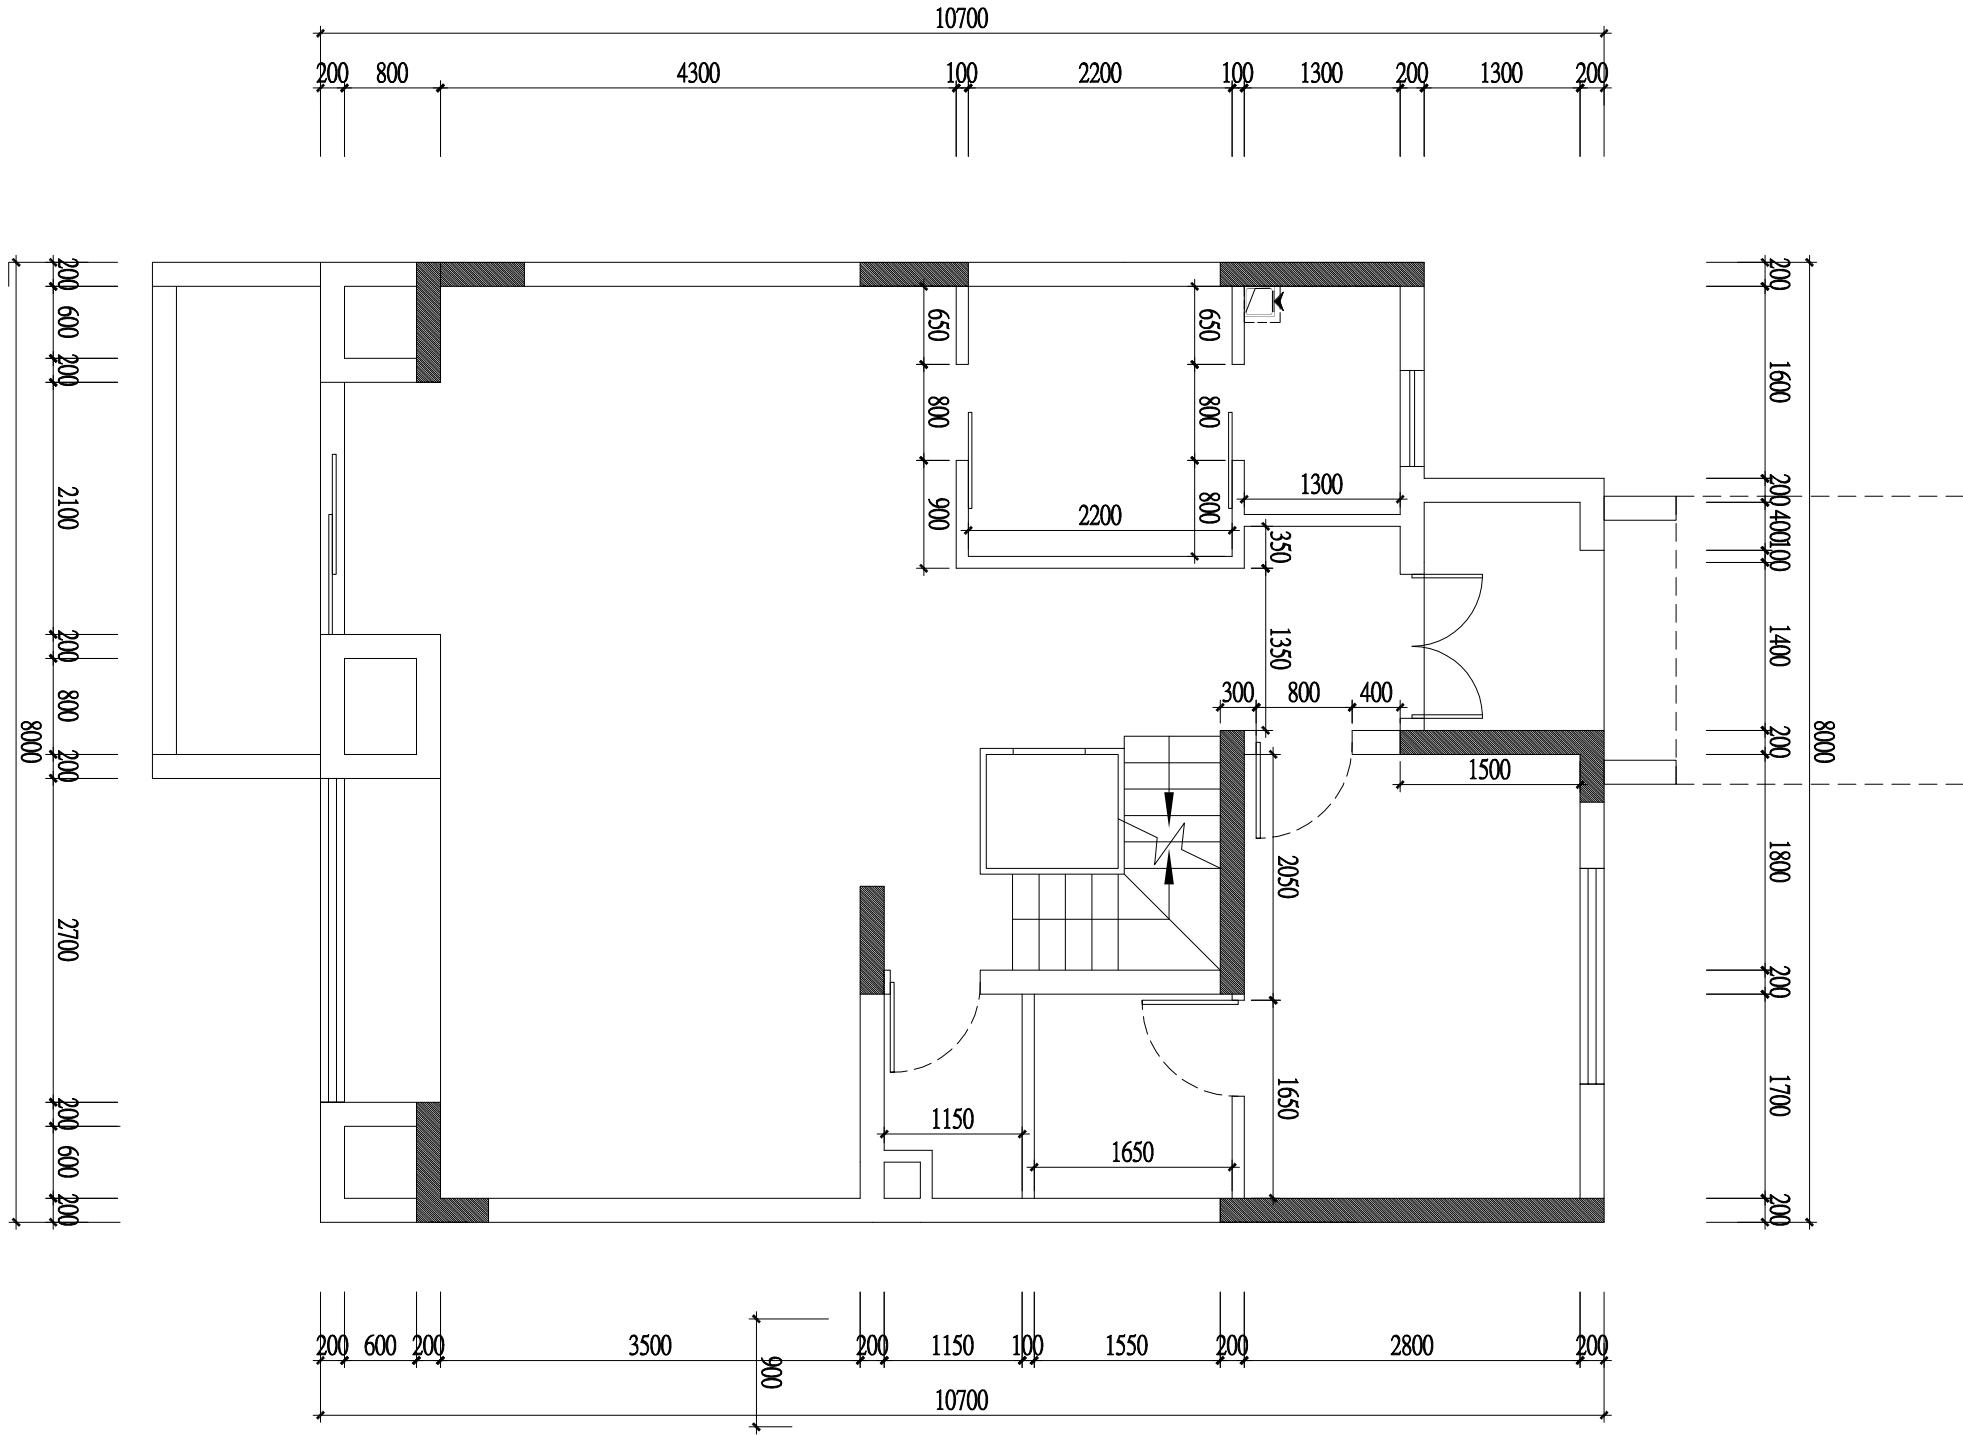


04  
1F隔墙尺寸图  
SCALE:1/60

是境  
設計

DRAWING TITLE  
1F隔牆尺寸

冬

备注 NOTE	<p>□在未经同意前，不得复制图纸及其设计任何部份。</p> <p>□所有图纸尺寸标注必须在实际工地复核及量度。</p> <p>□请勿按比例量度图纸，应采用已标明的尺寸。</p> <p>□本图纸必须和机房说明、会司多款及其有关图纸，并使用，如发现图纸内容有不符之处，必须立刻通知设计师。</p>
项目名称 PROJECT	龙湖椿山
业主 CLIENT	
总负责人 PRINCIPAL	
设计 DESIGNER	
绘图 DRAWN BY	
校对 COLLATE	
审核 APPROVE	
比例 SCALE	1 : 60
日期 DATE	2020.07
图名 NAME	

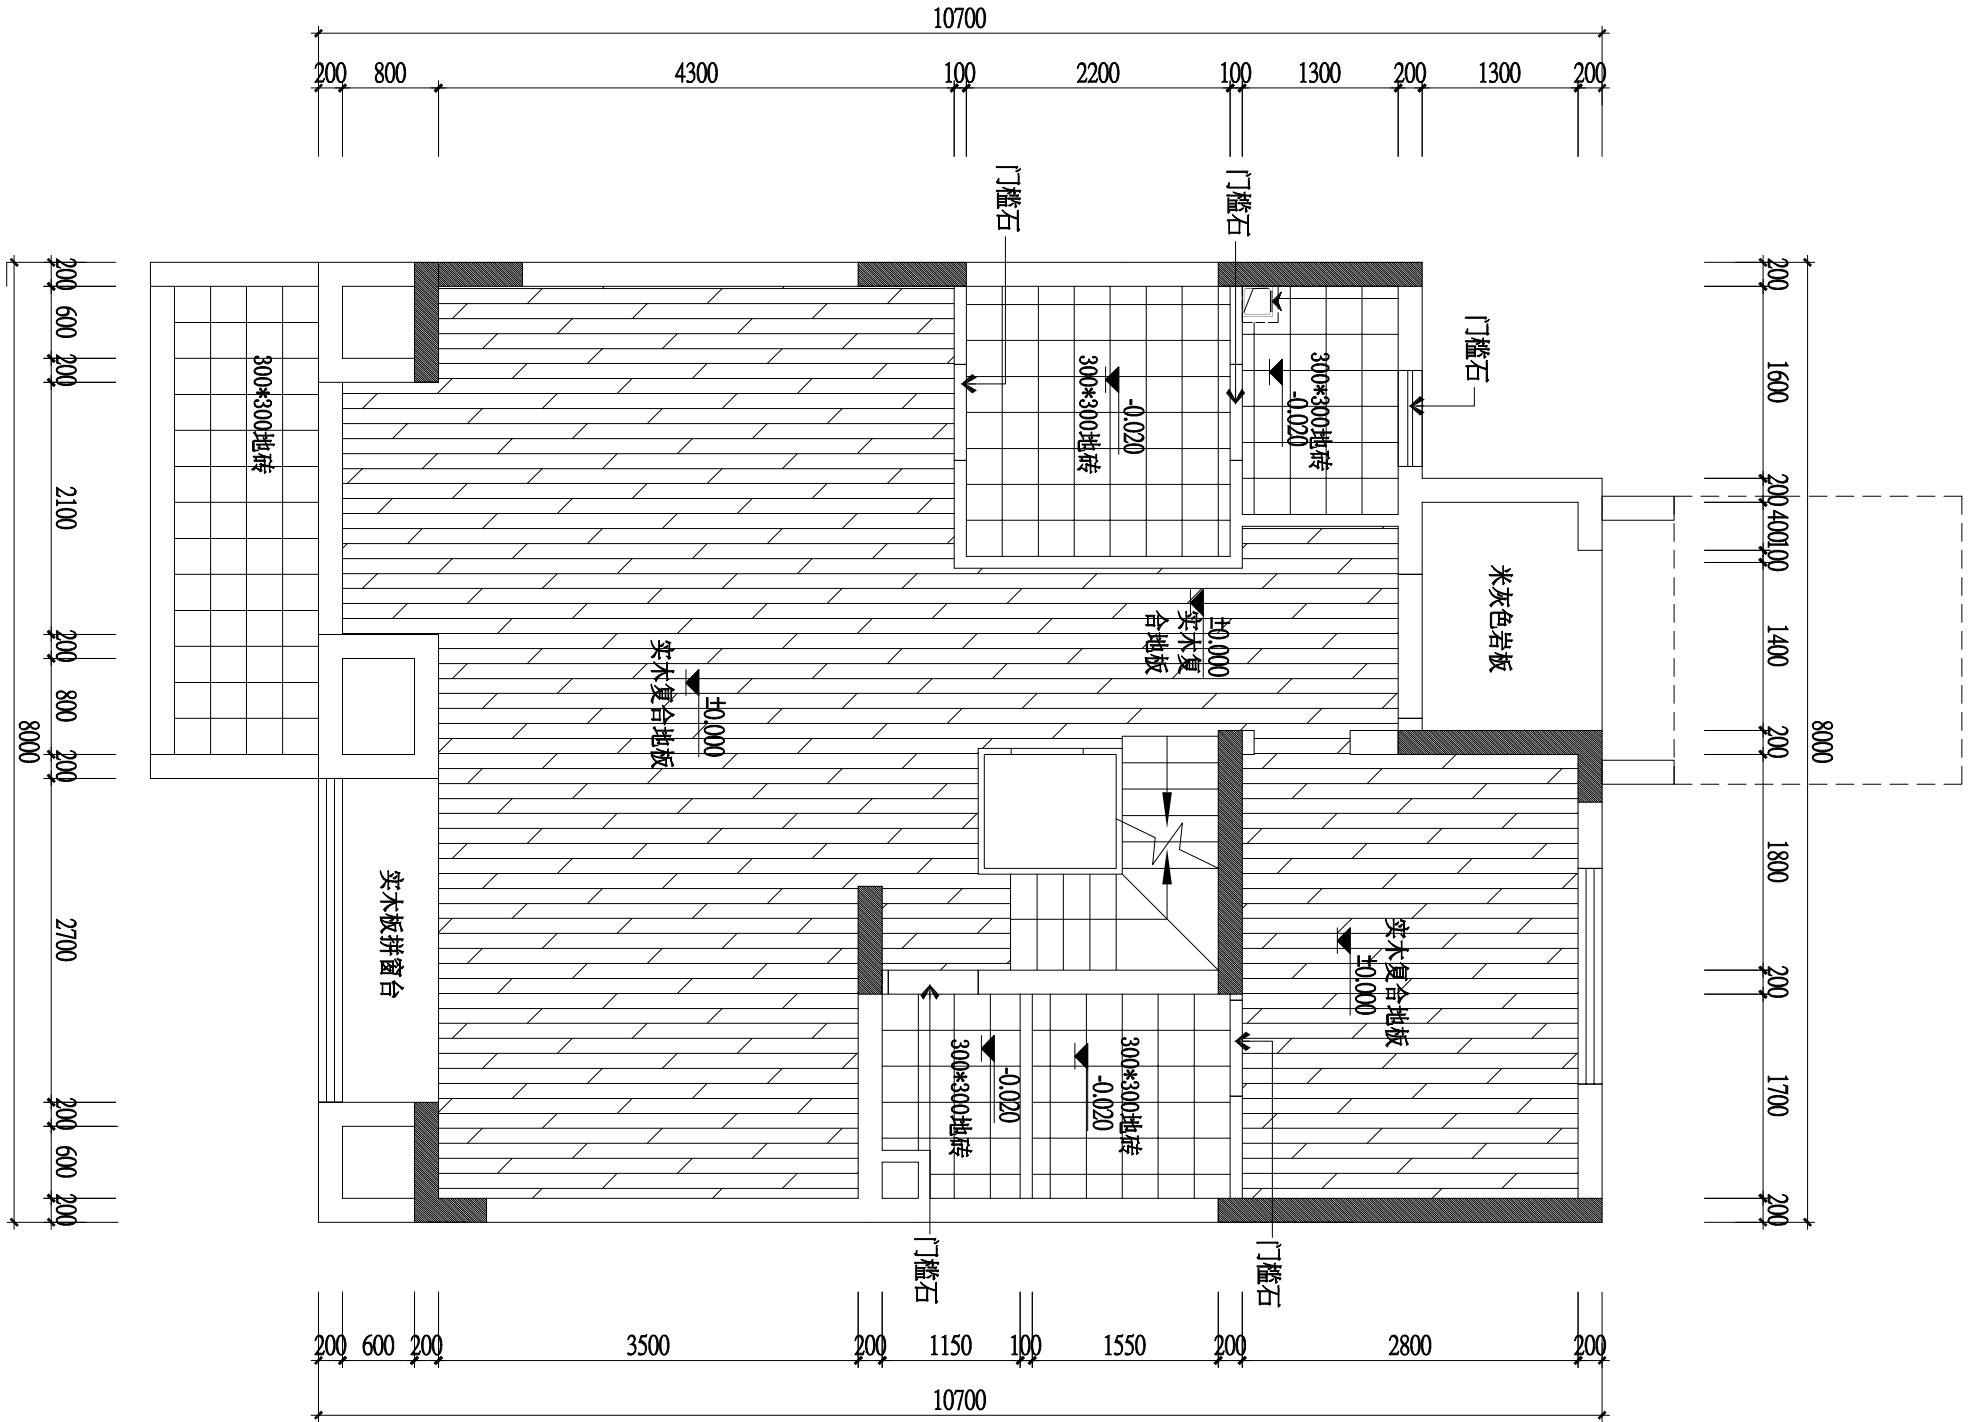

四  
玉

□在未经同意前，不得复制图纸及其设计任何部份。

□所有图纸尺寸标注须在实际工地上复核及量度。

□请勿按比例量度图纸，应采用已标明的尺寸。

□本图集从第10页起共10页，含各张单张图。

他有关图纸……并使用……如发现有不得之处，必须立刻通知

项目名称  
PROJECT  
龙湖椿山|

图名	DRAWING TITLE
比例	SCALE 1 : 6
日期	DATE 2020

# 1F地面前材質圖

1F地面前质图

圖  
SHEET NO  
1F.P-05

SHEET 1

NO. 5

---



1

1F.P-05

是境設計

厨房家具由专业  
橱柜公司深化设计

备 注  
NOTE  
□在未经同意前，不得复制图纸及其设计  
任何部分。  
□所有图纸尺寸标注须在实际工地上复核及  
量度。  
□请勿按比例量度图纸，应采用已标明的  
尺寸。

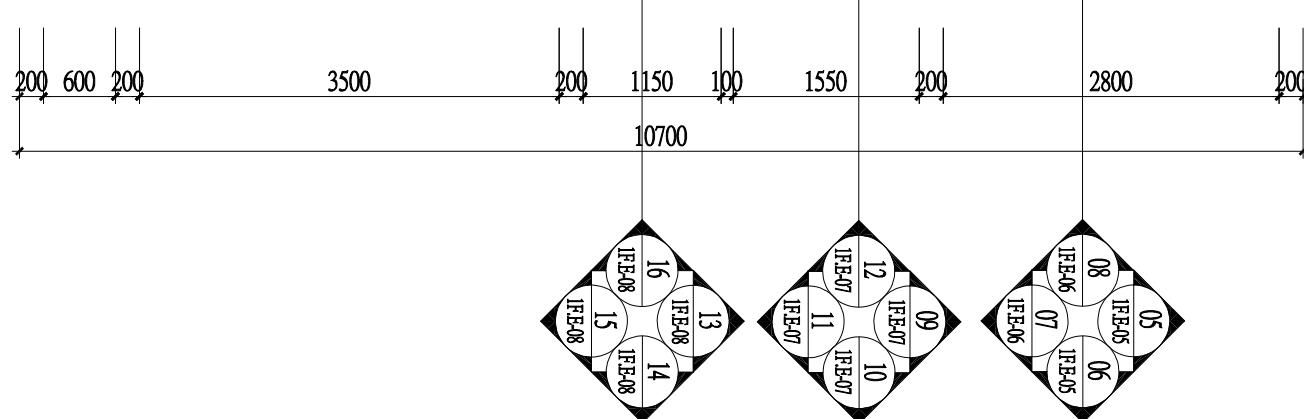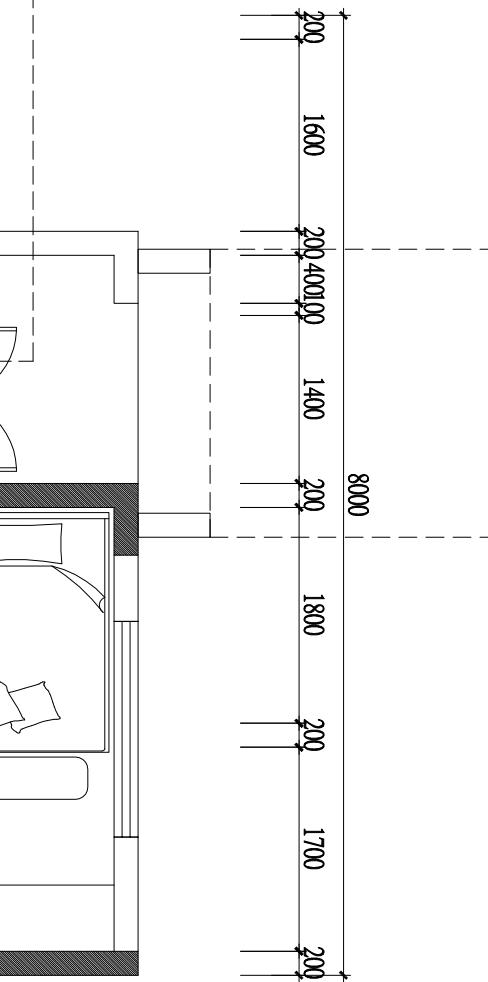

总 负 责 PRINCIPAL	业 主 CLIENT
项 目 名 称 PROJECT	龙湖椿山
设 计 DESIGNER	
绘 图 DRAWN BY	
校 对 COLLATE	
审 核 APPROVE	
比 例 SCALE	1 : 60
日 期 DATE	2020.07
图 名 DRAWING TITLE	1F立面索引图

图 号  
SHEET NO


1F.P-06

是 境  
設 計

06 1F立面索引图  
SCALE:1:60

备注  
NOTE  
□在未经同意前，不得复制图纸及其设计任何部分。  
□所有图纸尺寸标注须在实际工地复核及量度。  
□请勿按比例量度图纸，应采用已标明的尺寸。

□本图纸必须和规格说明、合同条款及其他有关图纸，并使用《建筑制图标准》有关规定。凡该图纸内容有不符之处，必须立刻通知设计者。

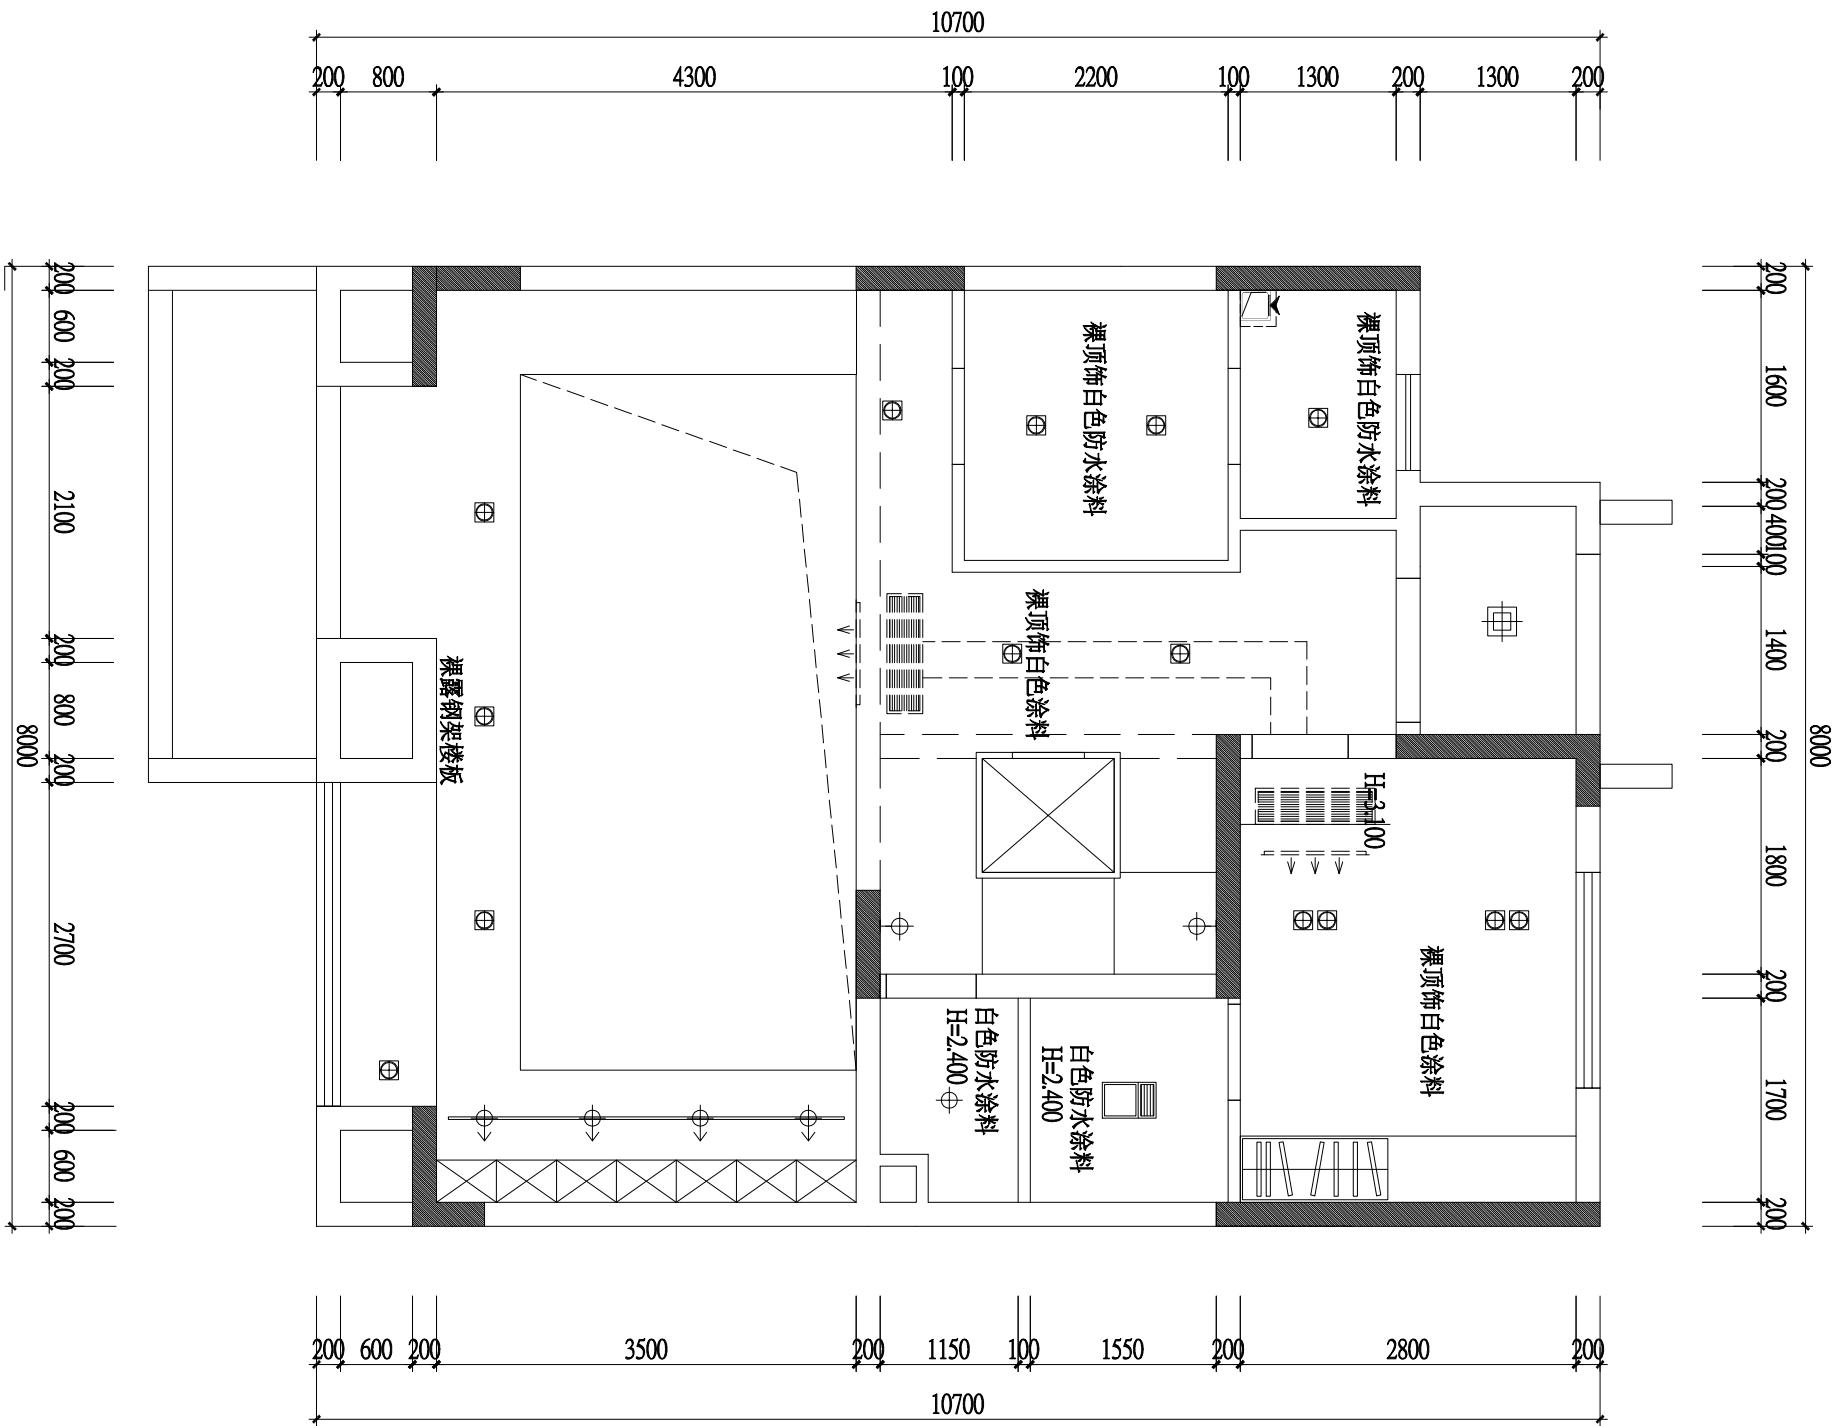

照明灯具说明：

图例	名称	图例	名称
□	明装筒灯	——	暗藏式灯带
⊕	防潮筒灯	⊕	壁灯
↑	轨道射灯	⊕⊕	艺术吊灯
⊕	嵌入式筒灯	串	吸顶灯

1F天花布置图


图号  
SHEET NO  
1F.P-07

是境  
设计  
設計



备注  
NOTE  
□本图版必须和接线图、合同条款及其设计任同部分。  
□所有图纸尺寸标注须在实际工地复核及他有关图纸，并使用，如发现图纸内容有不符之处，必须立刻通知设计者。

□本图版必须和接线图、合同条款及其设计任同部分。  
□所有图纸尺寸标注须在实际工地复核及他有关图纸，并使用，如发现图纸内容有不符之处，必须立刻通知设计者。

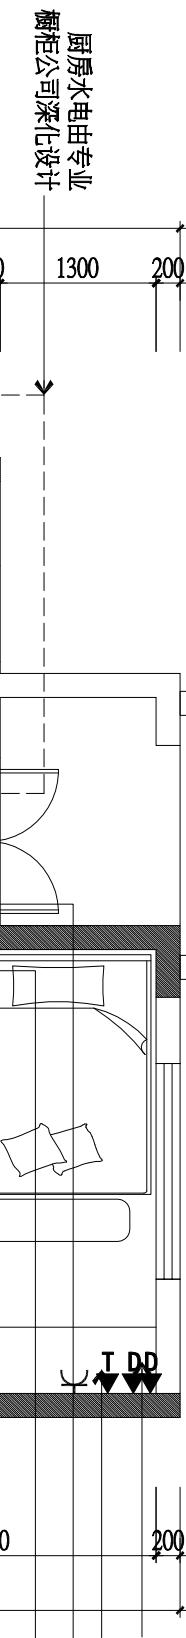

### 插座说明

图例	名称	图例	名称
+	二,三极单相组合安全插座	■	防水插座
●	吸风机	□	地插
▼	电话接口	④	电视接口
▼	网络接口	EEB	等电位

注：开关盒面板间距20mm;所有标高为重心距地。



备注  
NOTE  
◎本图未经同意，不得复制图纸及其设计任何部分。  
◎所有图纸尺寸标注须在实际工地复核及量度。  
◎请勿按比例量度图纸，应采用已标明的尺寸。

◎本图必须根据说明、合同条款及其他有关图纸，并使用《建筑制图标准》规定的内容和符号。必须立刻通知设计者。  
◎请勿按比例量度图纸，应采用已标明的尺寸。

业 主  
CLIENT

项 目 名 称  
PROJECT  
龙湖椿山

总 负 责  
PRINCIPAL

设 计  
DESIGNER

绘 图  
DRAWN BY

校 对  
COLLATE

审 核  
APPROVE

核

比 例  
SCALE

1 : 60

日 期  
DATE


2020.07  
DRAWING TITLE

1F水路布置图

图 号  
SHEET NO

1F.P-11

注：室内水管均从梁底最高处走，冷热水管直径25mm，排水管直径50mm。

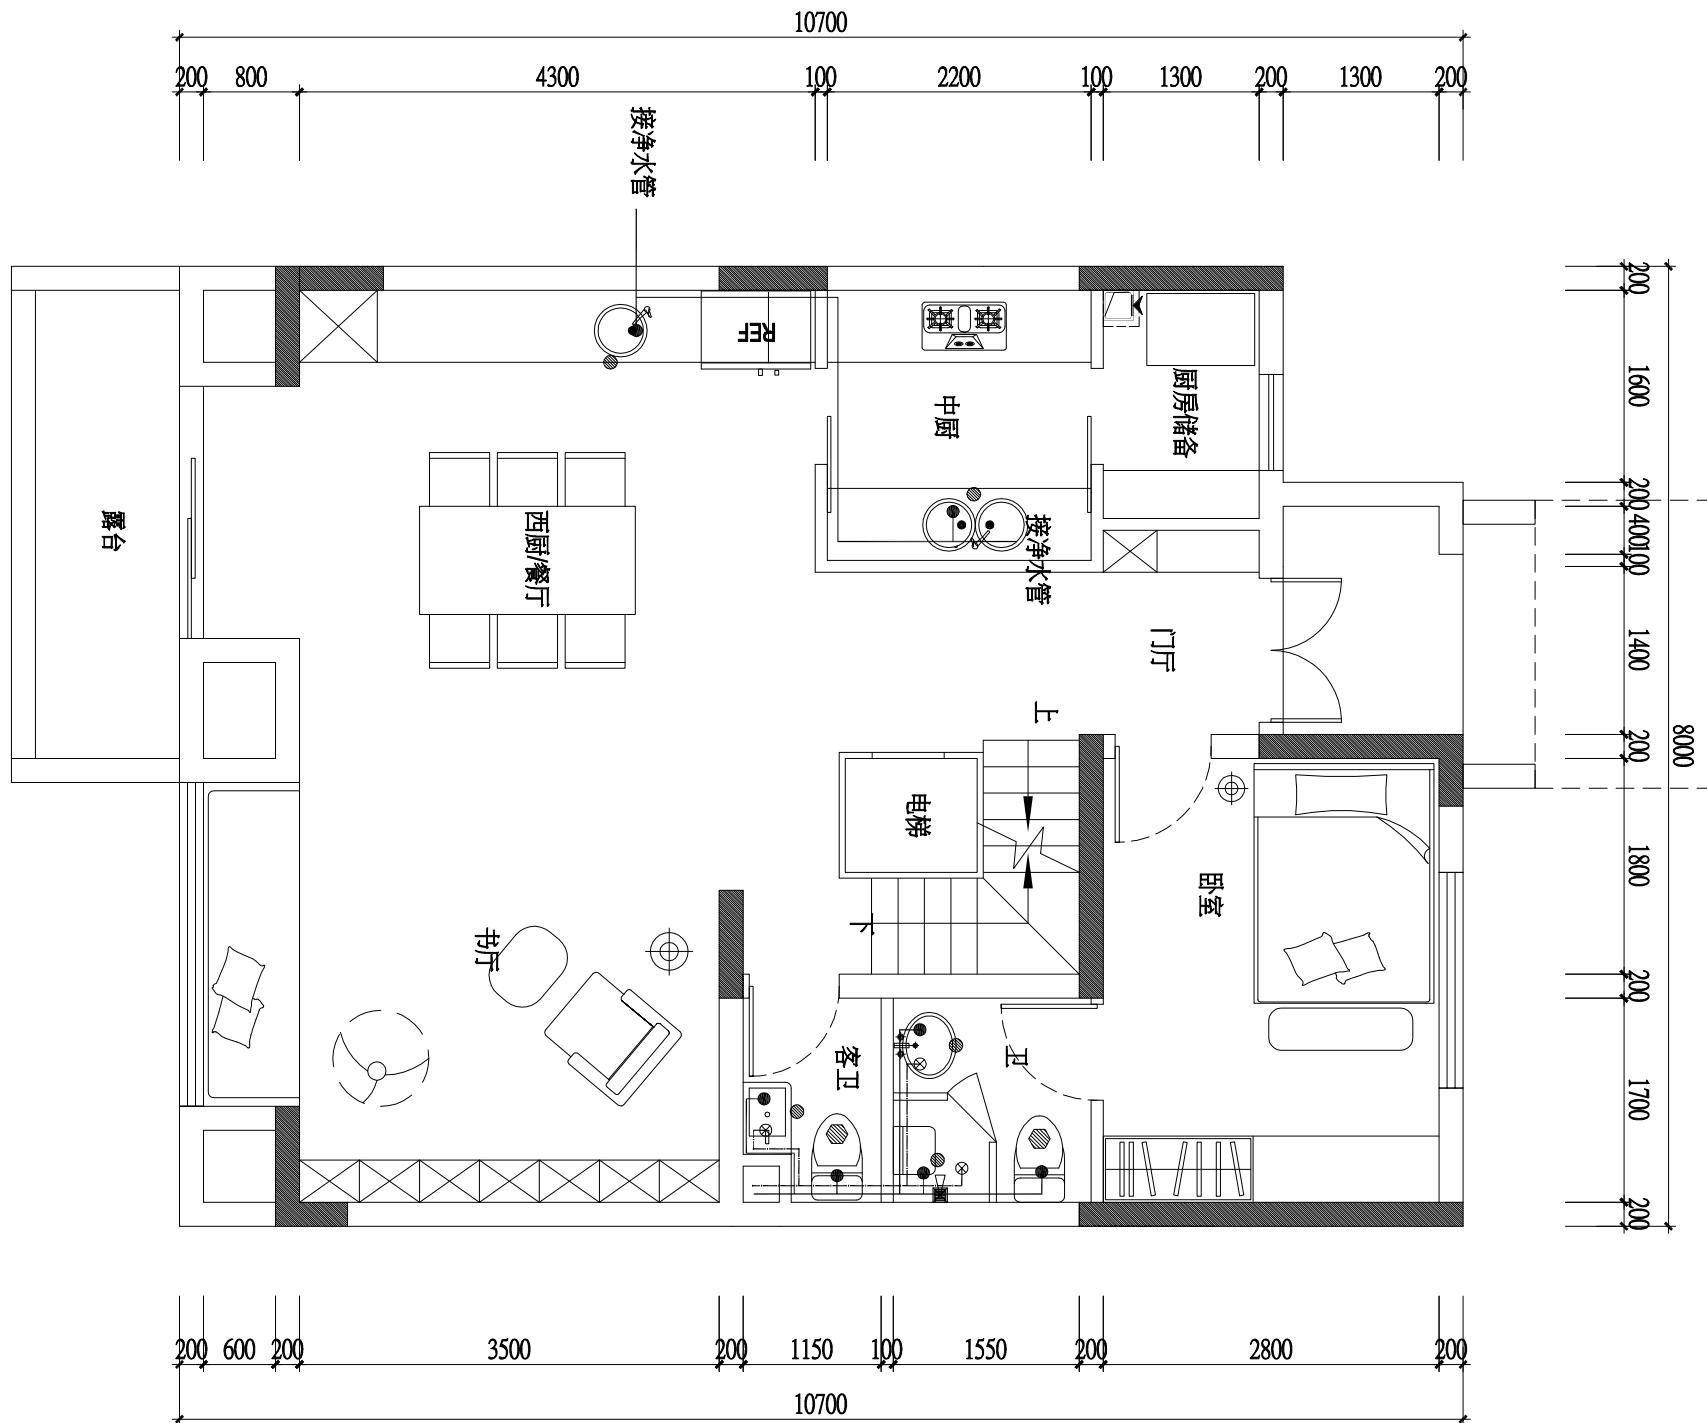


给排水说明：

图例	名称	图例	名称
●	给水口	①	墙排水
⊗	热水上水口	——	热水管
●	排水口	——	给水管
◎	马桶排水口	□	热水器

备 注  
NOTE

□在未经同意前，不得复制图纸及其设计任何部分。  
□所有图纸尺寸标注须在实际工地复核及量度。  
□请勿按比例量度图纸，应采用已标明的尺寸。  
□本图纸必须和规格说明、合同条款及其有关图纸，并使用，如发现图纸内容有不符之处，必须立刻通知设计者。

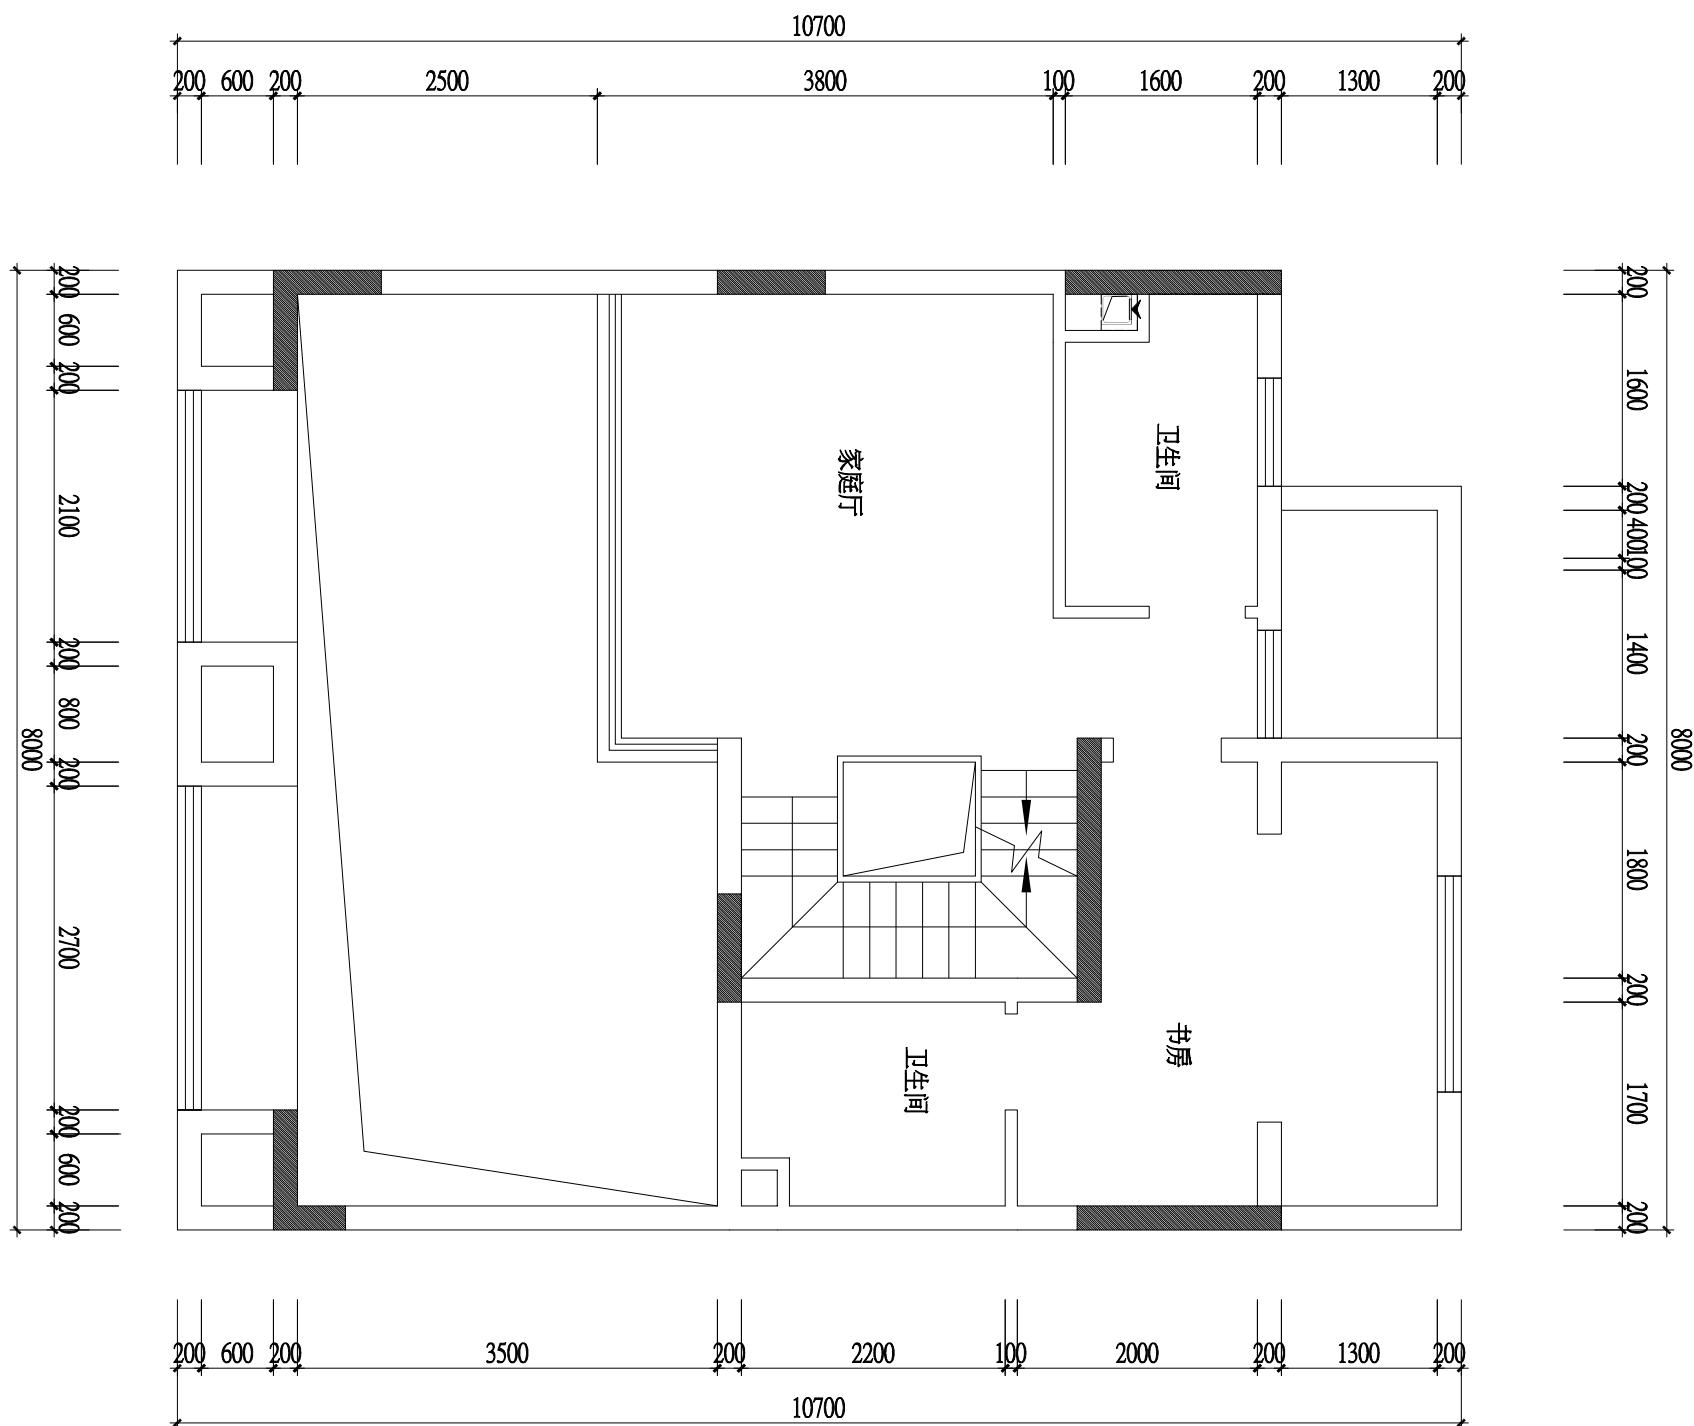

00 2F原始平面图  
SCALE:1:60

审 核	APPROVE
比 例	1 : 60
SCALE	
日 期	2020.07
图 名	DRAWING TITLE

2F原始平面图

图 号  
SHEET NO

2F.P-00

是 境  
設 計

备注  
NOTE

□在未经同意前，不得复制图纸及其设计任何部份。  
□所有图纸尺寸标注须在实际工地复核及量度。  
□请勿按比例量度图纸，应采用已标明的尺寸。

CLIENT

项目名称  
PROJECT

总负责

设计  
DESIGNER

絵  
DRAWN BY

校对

审批  
APPROVE

比例尺  
SCALE

日期  
DATE  
20

DRAWING TITLE

24增体扩筋

圖號

9E P-01

1

1

1

卷一

This architectural floor plan illustrates a demolition project with specific dimensions and instructions:

- Overall Dimensions:** The main horizontal span is 10700 mm, divided into sections of 200, 600, 200, 2500, 3800, 100, 1600, 200, 1300, and 200 mm.
- Demolition Areas:**
  - A large rectangular area on the left side, bounded by 200, 600, 200 mm on the left and 2500, 3800 mm on the right, contains a hatched pattern. A callout labeled "拆除楼板" (remove slab) points to its center, with dimensions 3900 mm wide and 1000 mm high.
  - A vertical section on the right side, bounded by 100, 1600, 200, 1300, and 200 mm, features three horizontal segments. The top segment has a height of 2300 mm. The middle segment has a height of 800 mm, with a 100 mm gap above it. The bottom segment has a height of 800 mm, with a 100 mm gap above it. Callouts labeled "拆除墙体" (remove wall) point to these segments, with dimensions 800 mm wide and 100 mm high for each.
  - A vertical section on the far right, bounded by 200, 1600, 200, 400, 100, 1400, 200, 1800, 200, 1700, and 200 mm, contains a hatched pattern. A callout labeled "拆除墙体" (remove wall) points to its center, with dimensions 600 mm wide and 200 mm high.
- Notes:**
  - A callout on the left side, enclosed in a cloud-like shape, contains the text: "备注：现场拆开小块看是否有水管类，若无便拆除2楼部分" (Note: Remove in small pieces on site to check for pipe類, if no pipes, remove the 2nd floor part).



备 注  
NOTE  
□在未经同意前，不得复制图纸及其设计  
任何部分。  
□所有图纸尺寸标注须在实际工地上复核及  
量度。  
□请勿按比例量度图纸，应采用已标明的  
尺寸。

□本图纸必须和规格说明、合同条款及其  
他有关图纸，并使用，如发现图纸内容  
有不符之处，必须立刻通知设计者。

业 主  
CLIENT

项 目 名 称  
PROJECT

龙湖椿山

总 负 责  
PRINCIPAL

设 计  
DESIGNER

绘 图  
DRAWN BY

校 对  
COLLATE

校 对  
COLLATE

审 核  
APPROVE

核

比 例  
SCALE

1 : 60


图 名  
DRAWING TITLE

日 期  
DATE


2020.07

图 号  
SHEET NO

2F墙体新建图  
2F.P-02

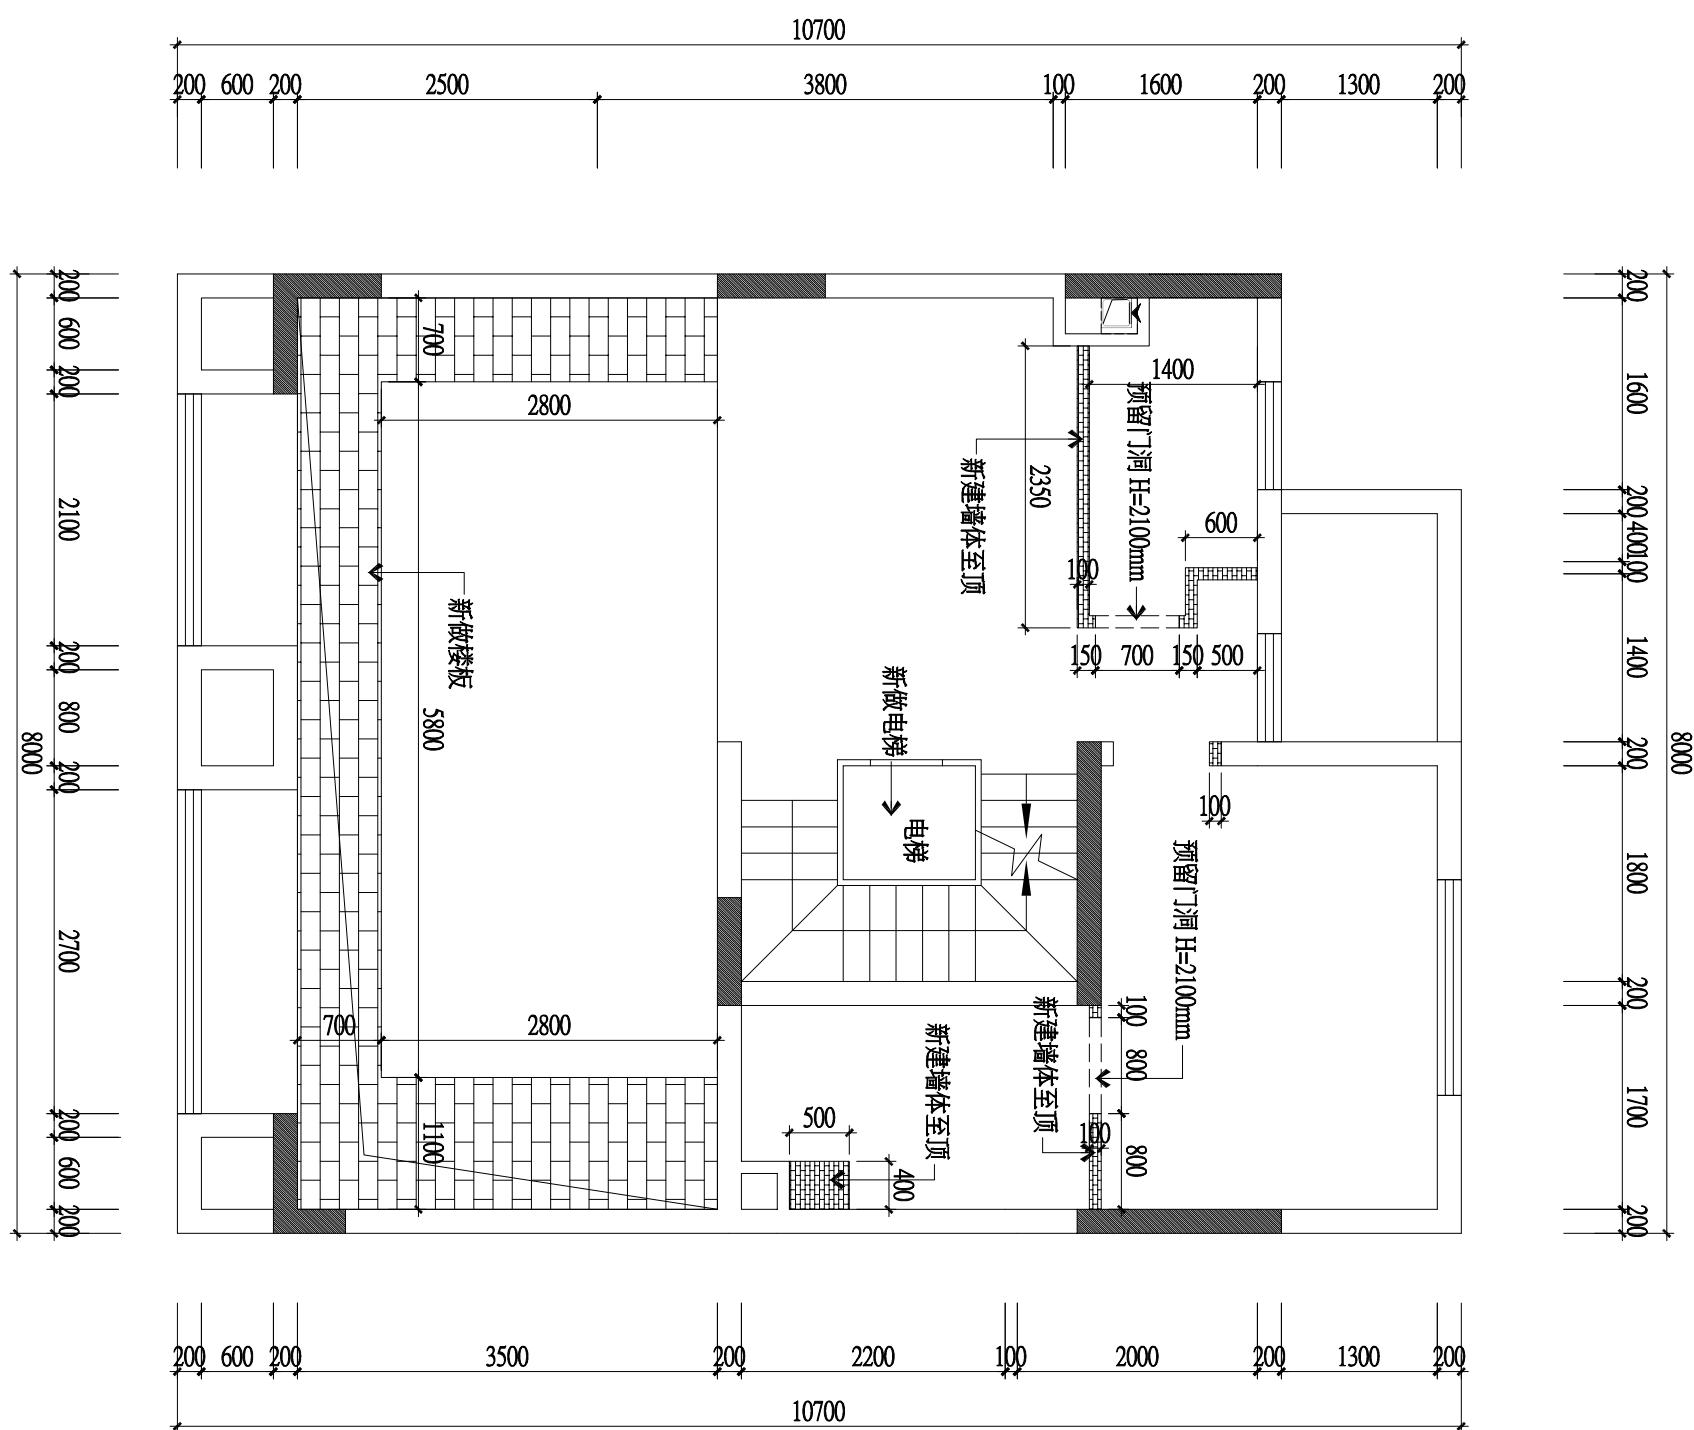

NOTE  
◎本图未经同意，不得复制图纸及其设计任何部分。  
◎所有图纸尺寸标注须在实际工地复核及量度。  
◎请勿按比例量度图纸，应采用已标明的尺寸。

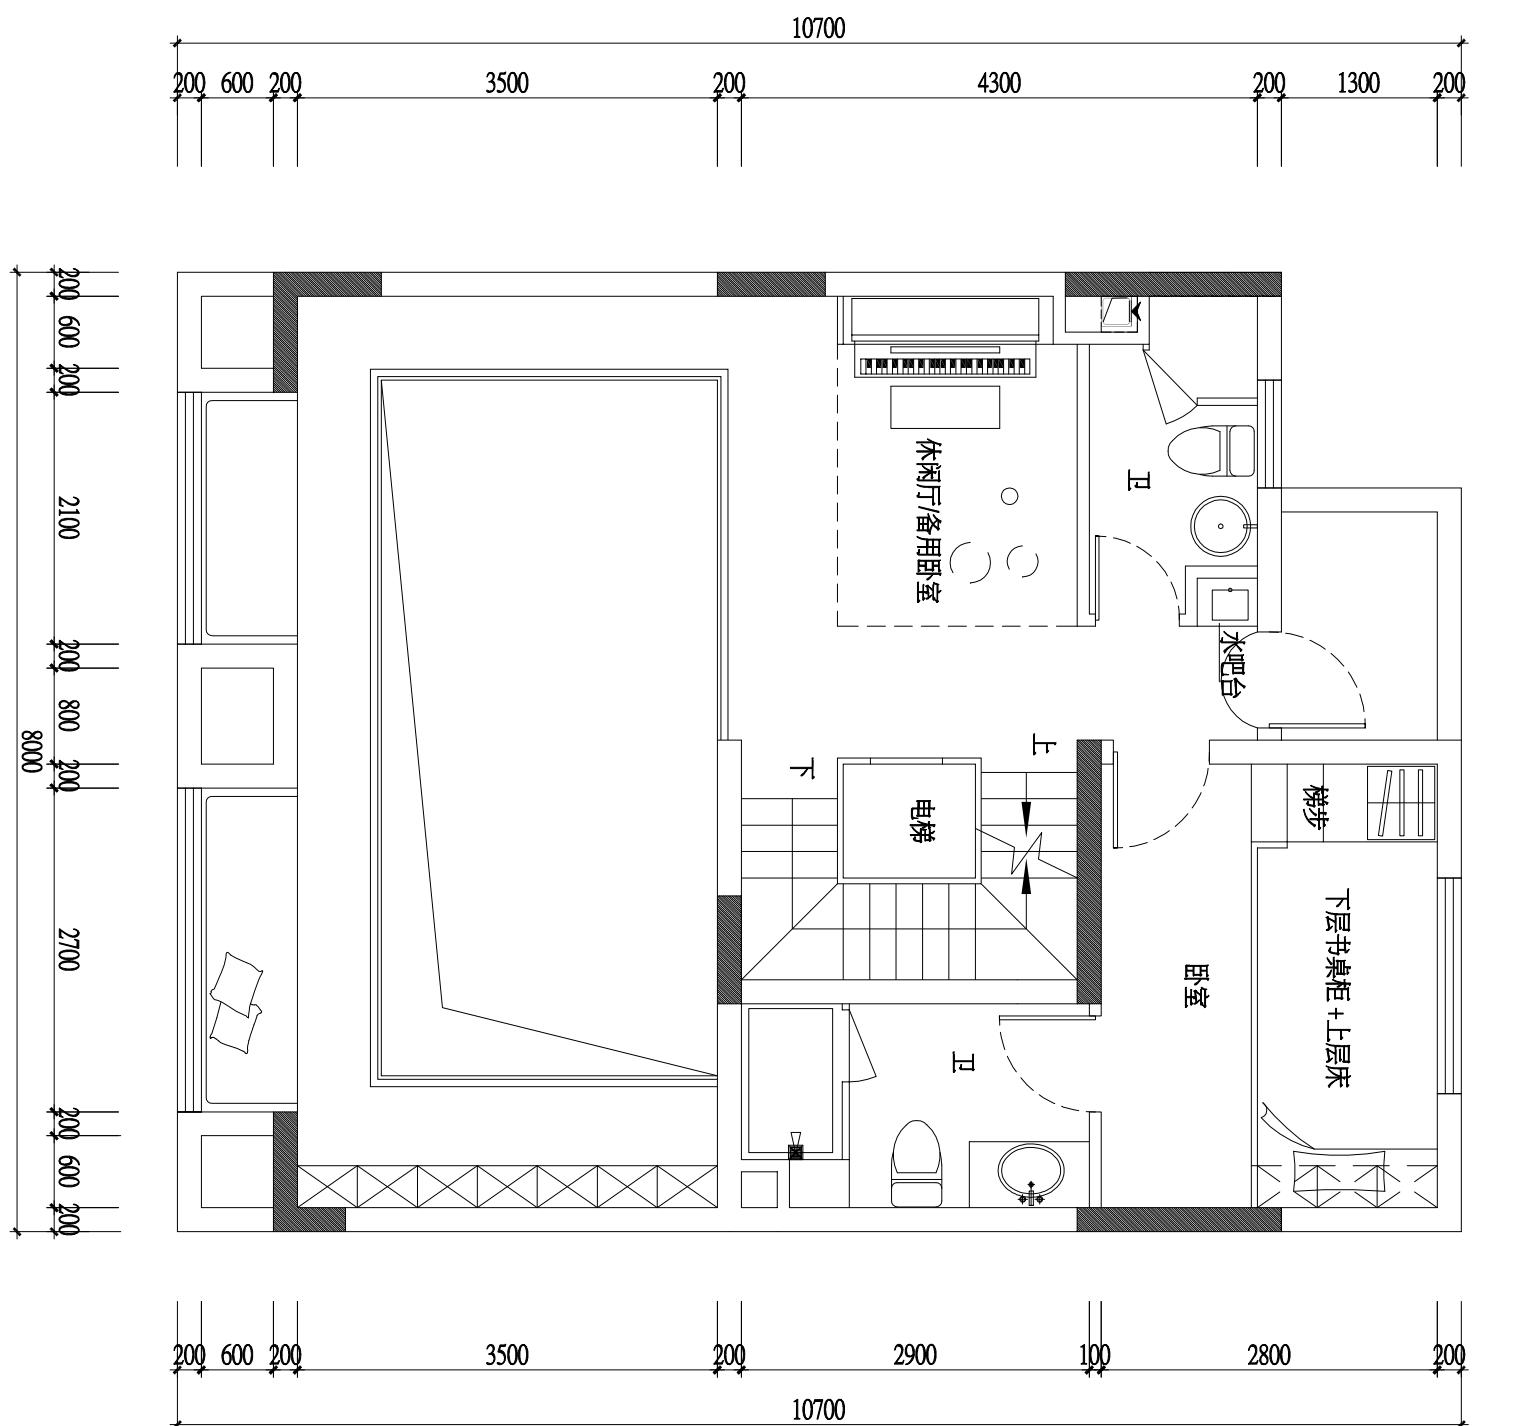

03 2F平面布置图  
SCALE:1:60


是境  
設計  
設計

2F平面布置图  
图号  
SHEET NO.  
2F.P-03

备 注  
NOTE  
◎本图未经同意，不得复制图纸及其设计任何部分。  
◎所有图纸尺寸标注须在实际工地复核及量度。  
◎请勿按比例量度图纸，应采用已标明的尺寸。

总 负 责 PRINCIPAL	业 主 CLIENT
项 目 名 称 PROJECT	龙湖椿山
设 计 DESIGNER	
绘 图 DRAWN BY	
校 对 COLLATE	
审 核 APPROVE	
比 例 SCALE	1 : 60
日 期 DATE	2020.07
图 名 DRAWING TITLE	



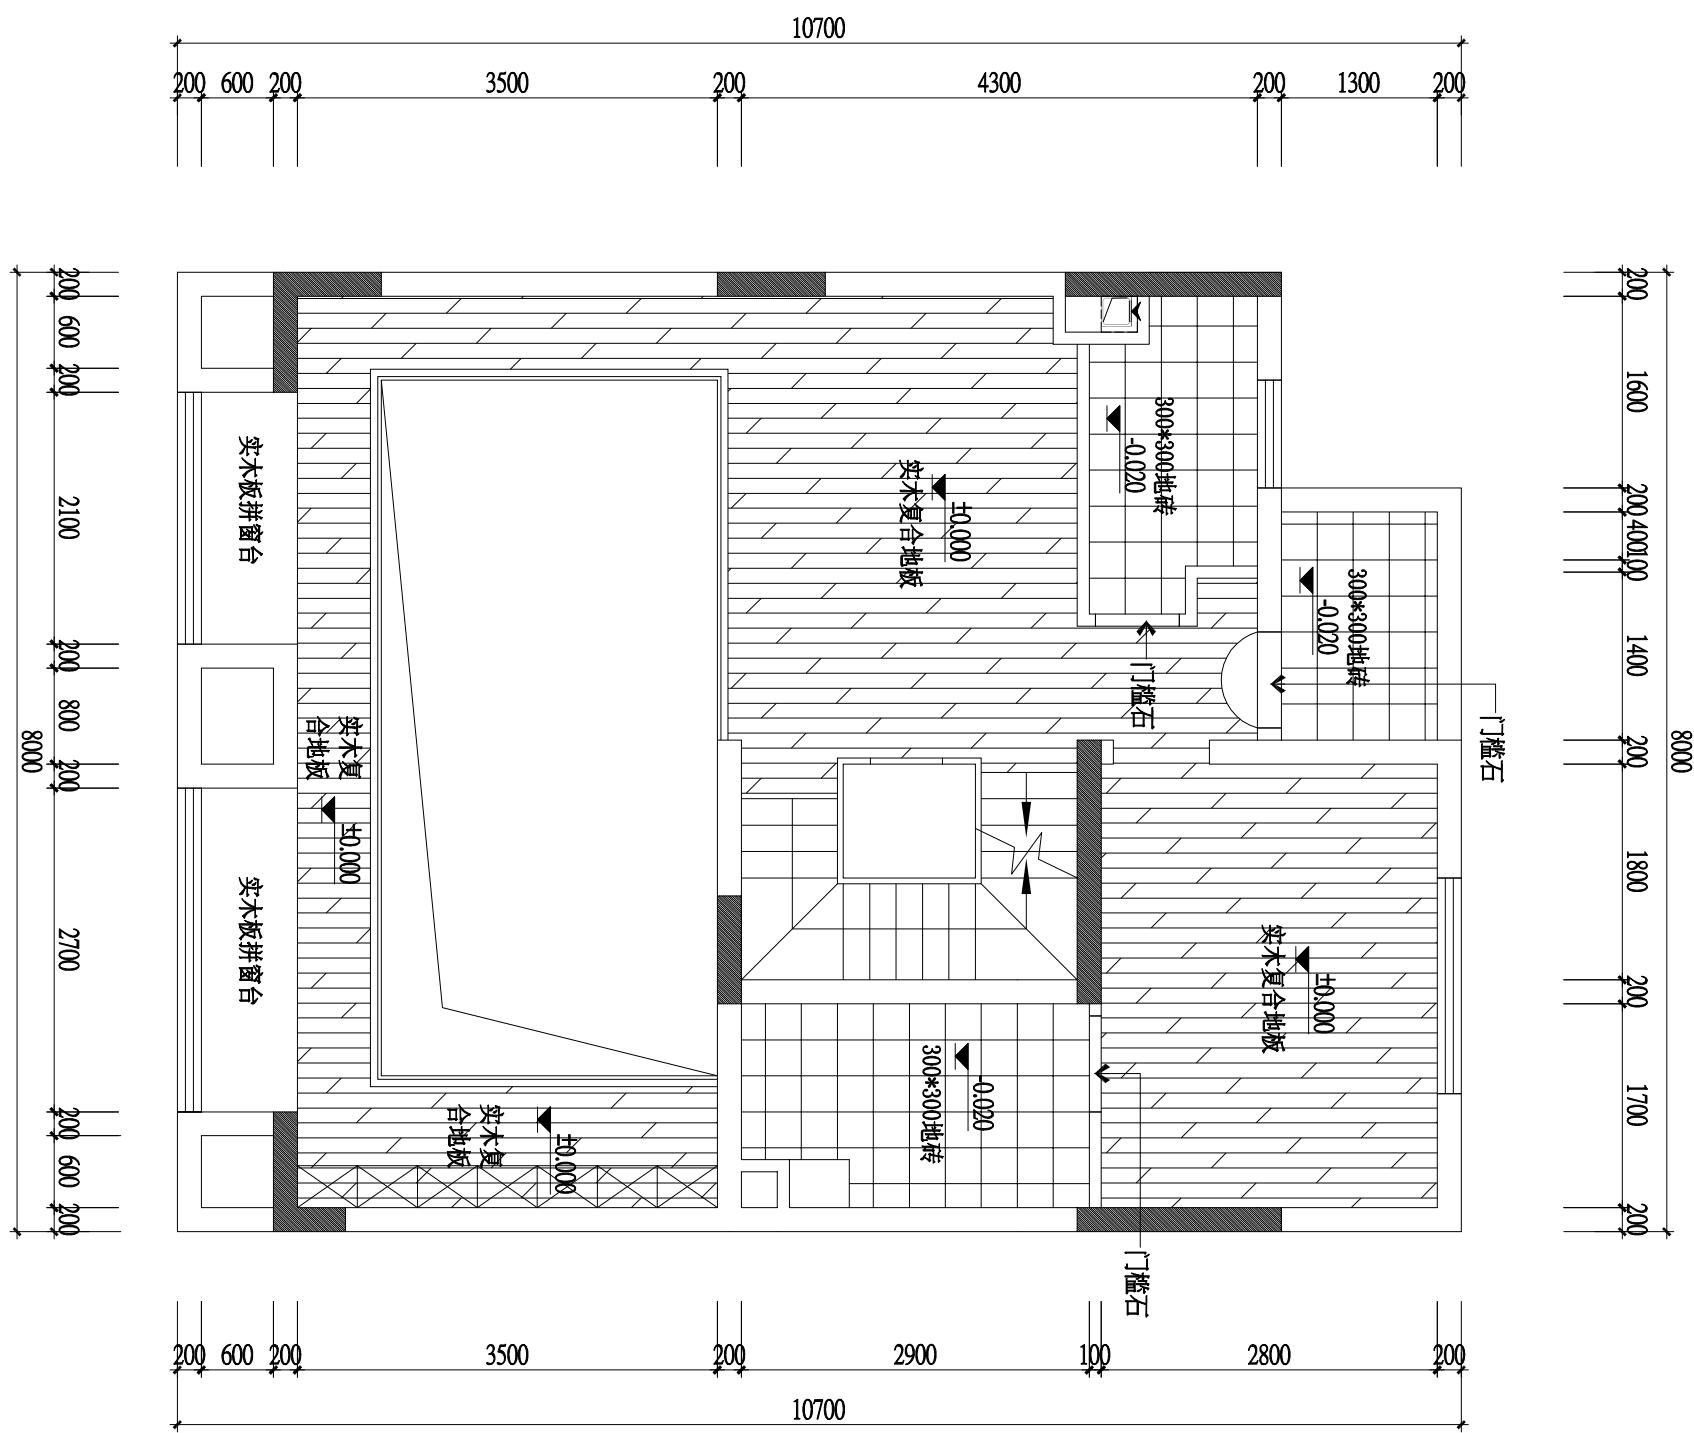

备注 NOTE
□在未经同意前，不得复制图纸及其设计 任何部分。

NOTE  
◎本图必须按图样说明、合同条款及其  
他有关图纸，并使用、如发现图纸内容  
有不符之处，必须立刻通知设计者。

◎本图尺寸标注须在实际工地上复核及  
量度。  
◎勿按比例量度图纸，应采用已标明的  
尺寸。

业 主  
CLIENT

项 目 名 称  
PROJECT

龙湖椿山

总 负 责  
PRINCIPAL

设 计  
DESIGNER

绘 图  
DRAWN BY

校 对  
COLLATE

审 核  
APPROVE

比 例  
SCALE

日 期  
DATE

图 名  
DRAWING TITLE


2F立面索引图

图 号  
SHEET NO

2F.P-06

是 境  
設 計


06 2F立面索引图  
SCALE:1:60

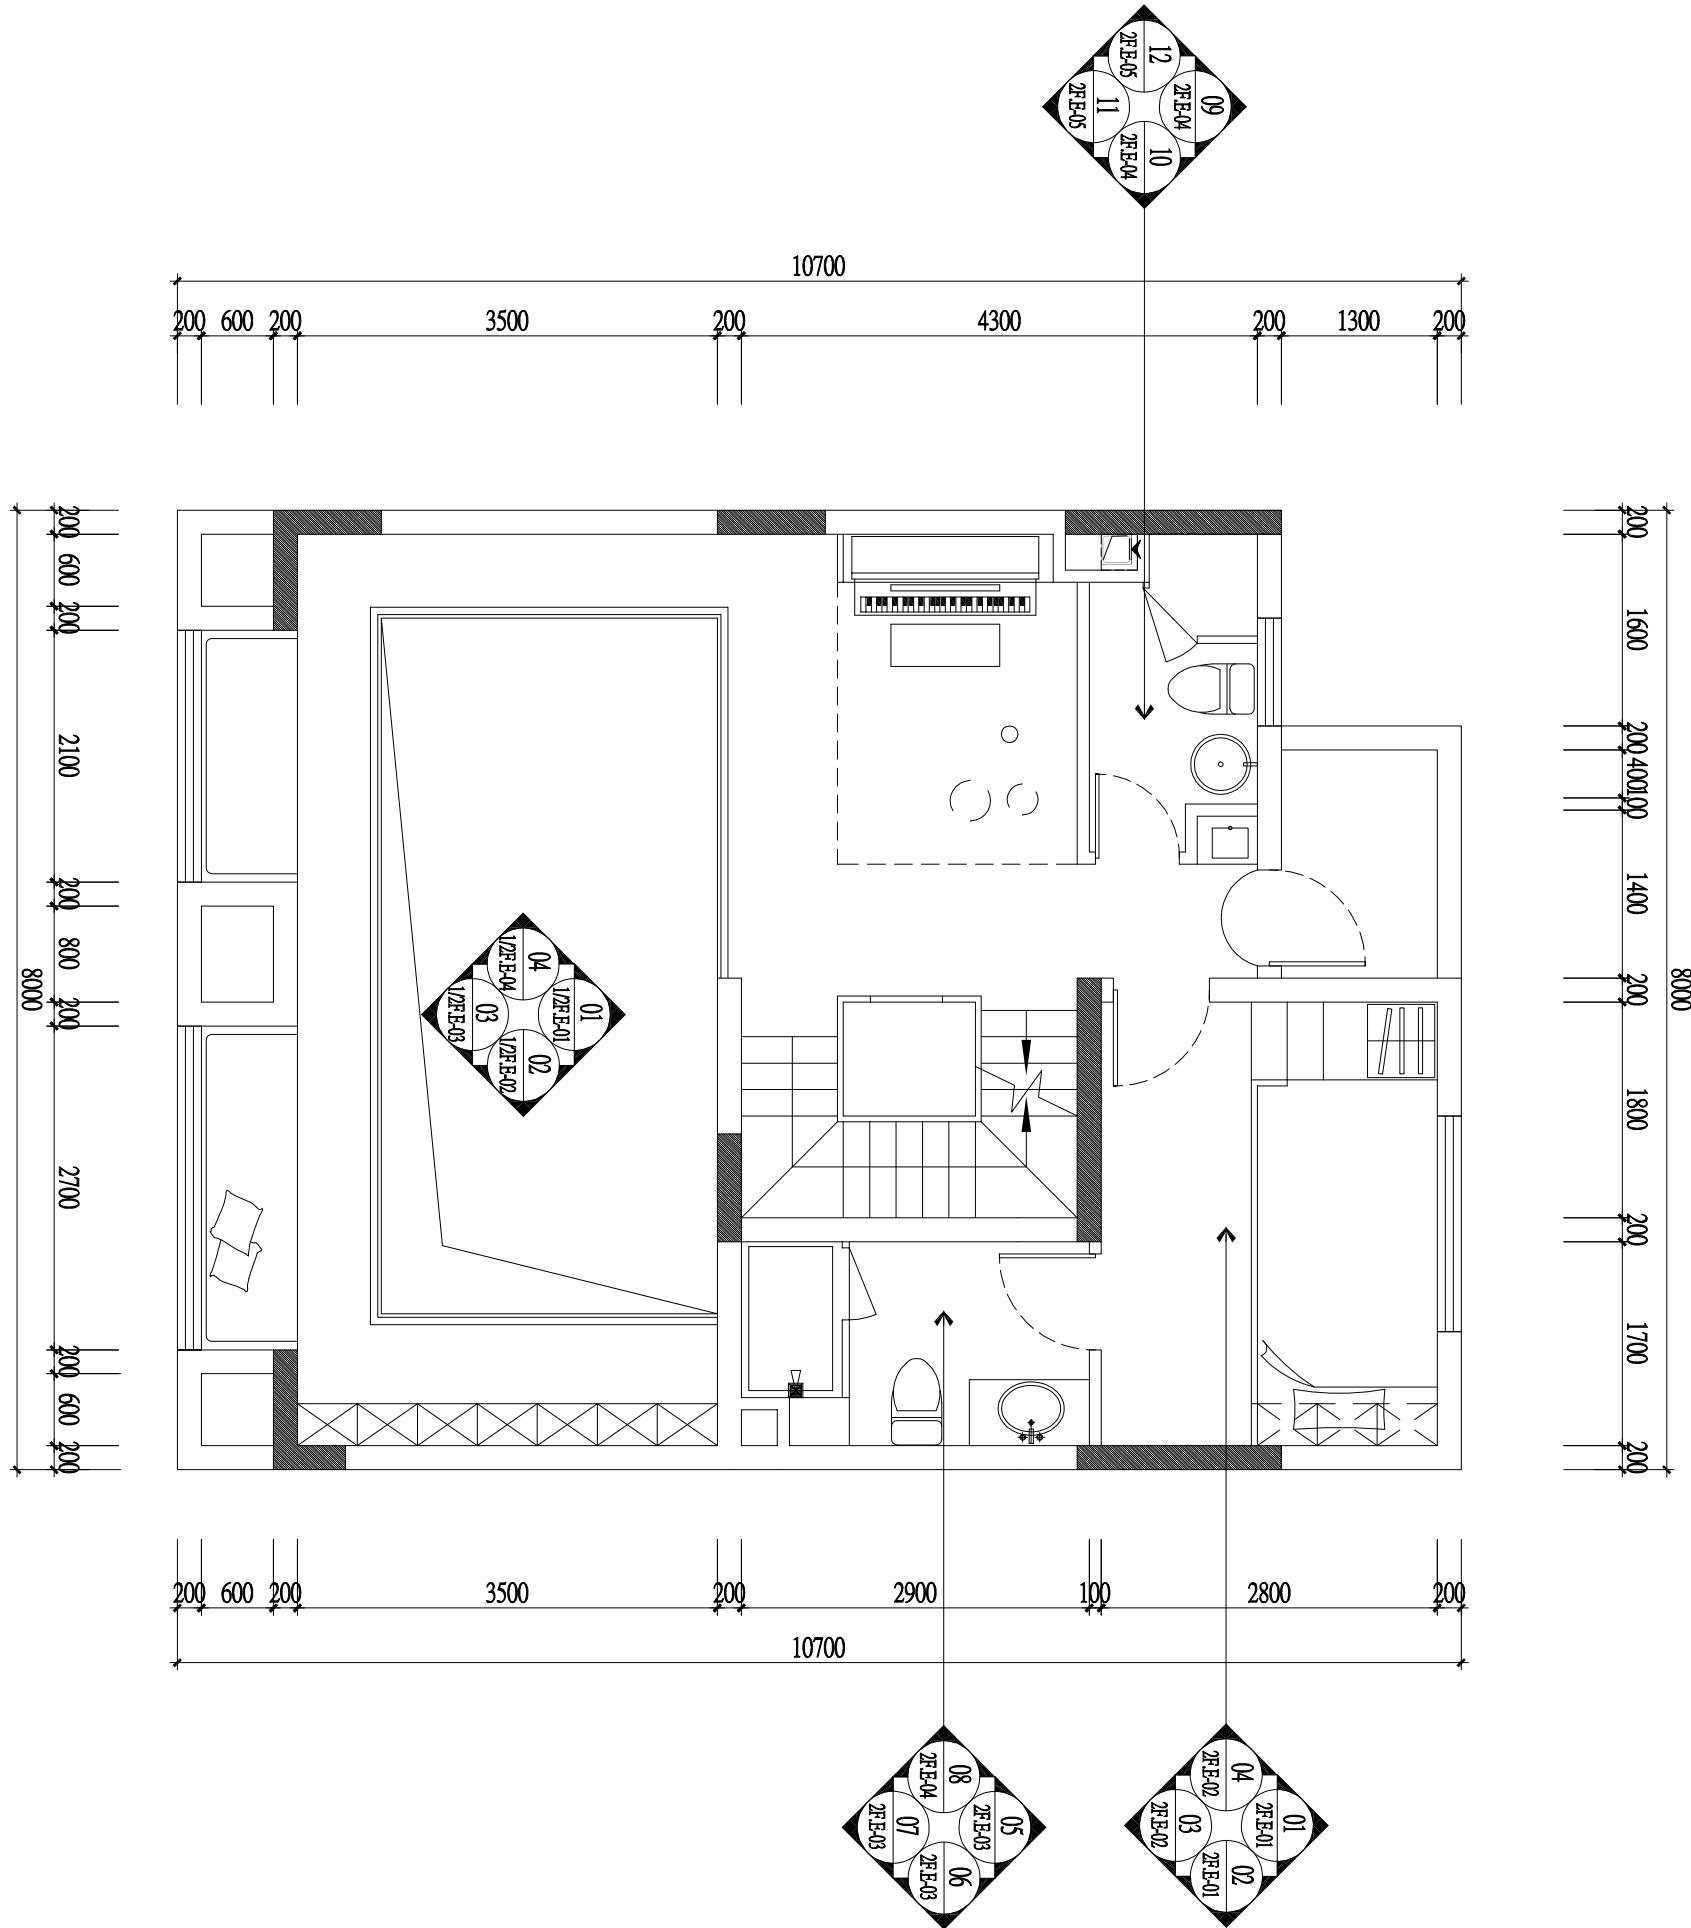

备注  
NOTE

□本图版必须和规格说明、合同条款及其  
他有关图纸一并使用。如发现图纸内容  
有不符之处，必须立刻通知设计者。

□所有图纸尺寸标注须在实际工地复核及  
量度。  
□请勿按比例量度图纸，应采用已标明的  
尺寸。

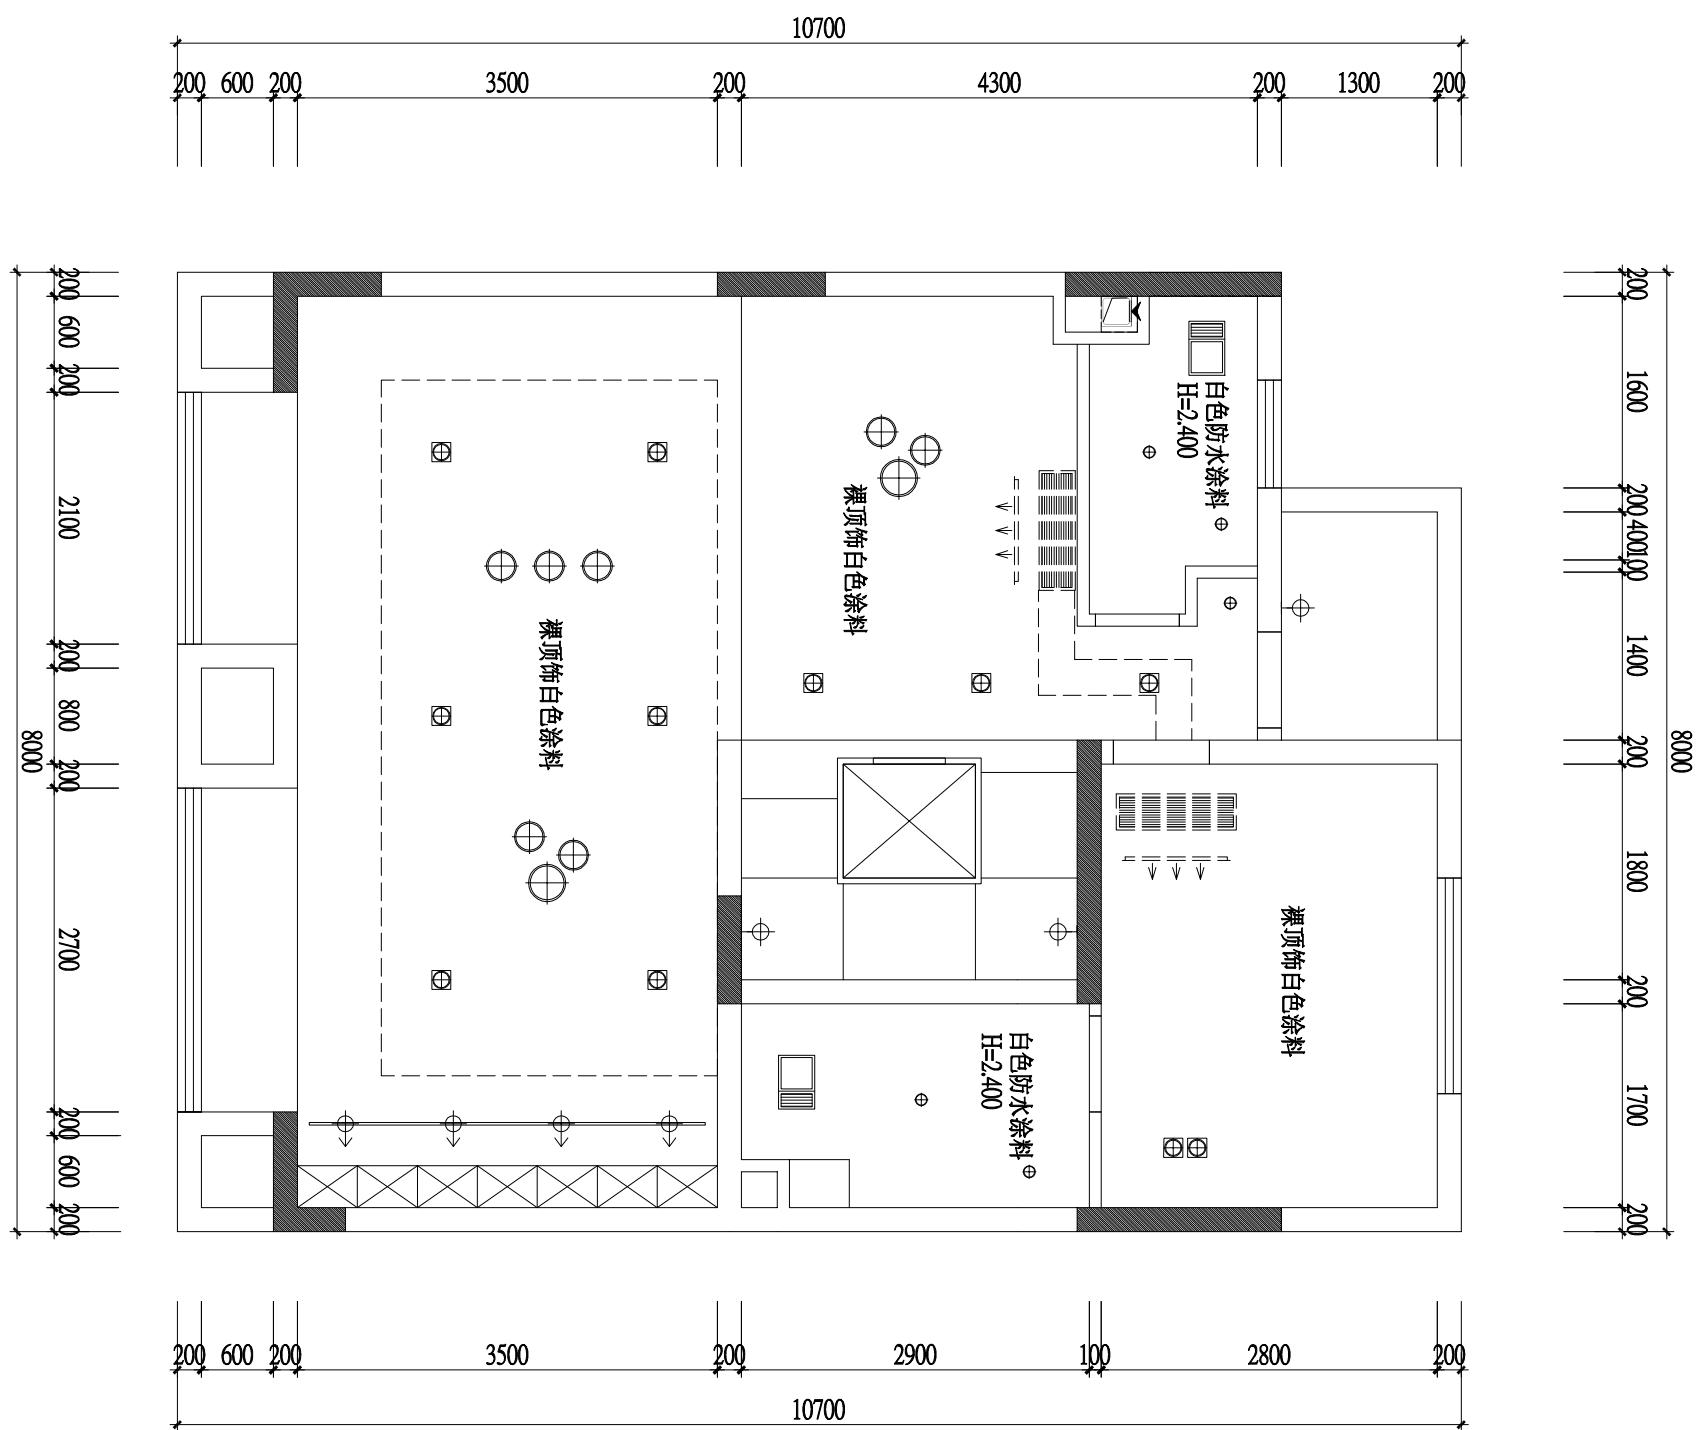

照明灯具说明：

图例	名称	图例	名称
⊕	明装筒灯	——	暗藏式灯带
⊕	防潮筒灯	⊕	壁灯
↑	轨道射灯	⊕⊕	艺术吊灯
⊕	嵌入式筒灯	⊕	吸顶灯


2F天花布置图

图号  
SHEET NO  
2F.P-07

是境  
设计

07 2F天花布置图  
SCALE:1:60

备  
注  
NOTE  
□本图版必须和说明配合使用，不得复制图纸及其设计任  
何部分。  
□所有图纸尺寸标注须在实际工地复核及  
量度。  
□请勿按比例量度图纸，应采用已标明的  
尺寸。

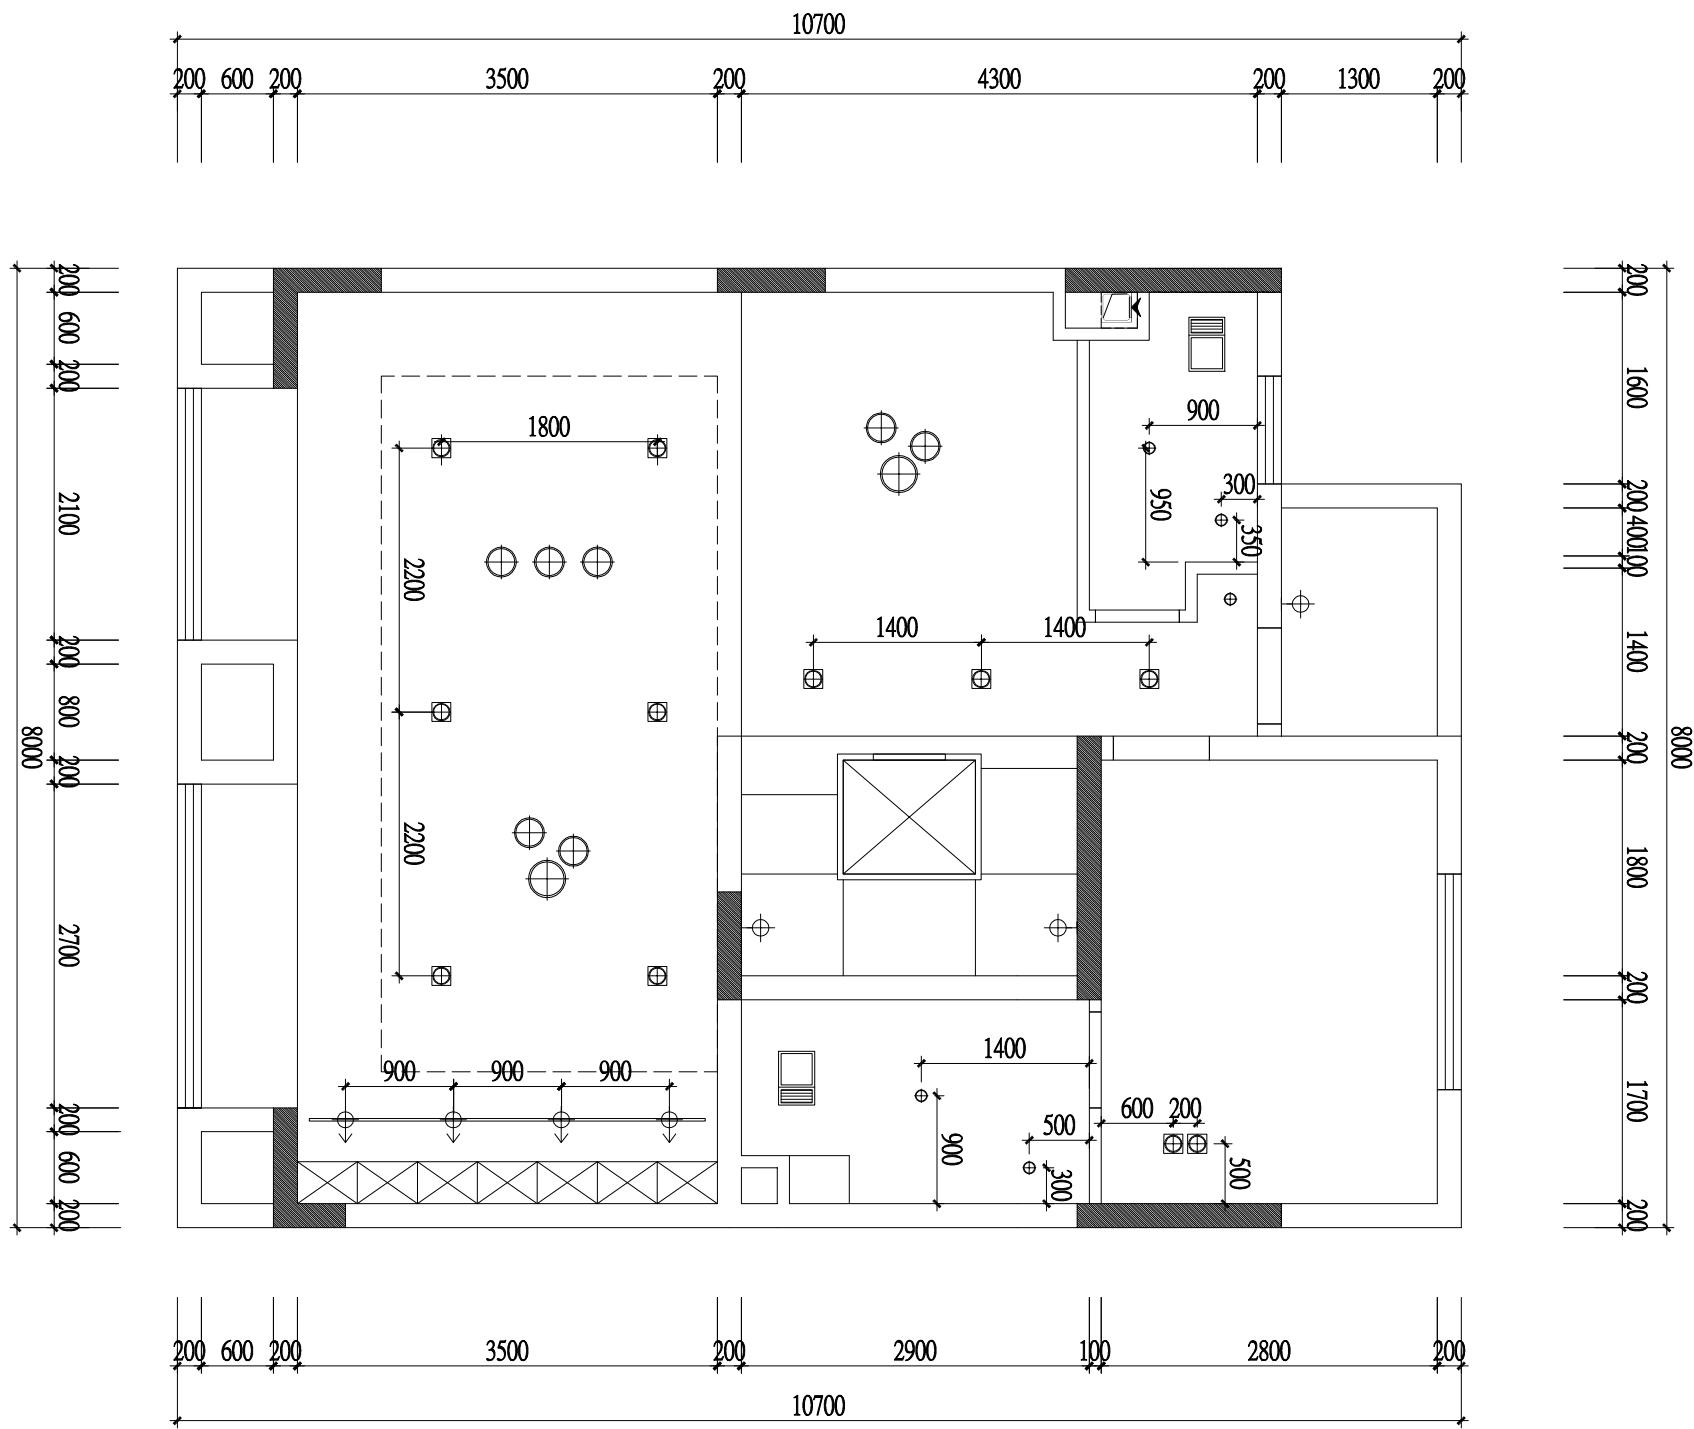


照明灯具说明：

图例	名称	图例	名称
□	明装筒灯	——	暗藏式灯带
⊕	防潮筒灯	⊕	壁灯
↑	轨道射灯	⊕⊕	艺术吊灯
⊕	嵌入式筒灯	串	吸顶灯

2F天花尺寸图

图  
号  
SHEET NO  
2F.P-08

是  
境  
設  
計

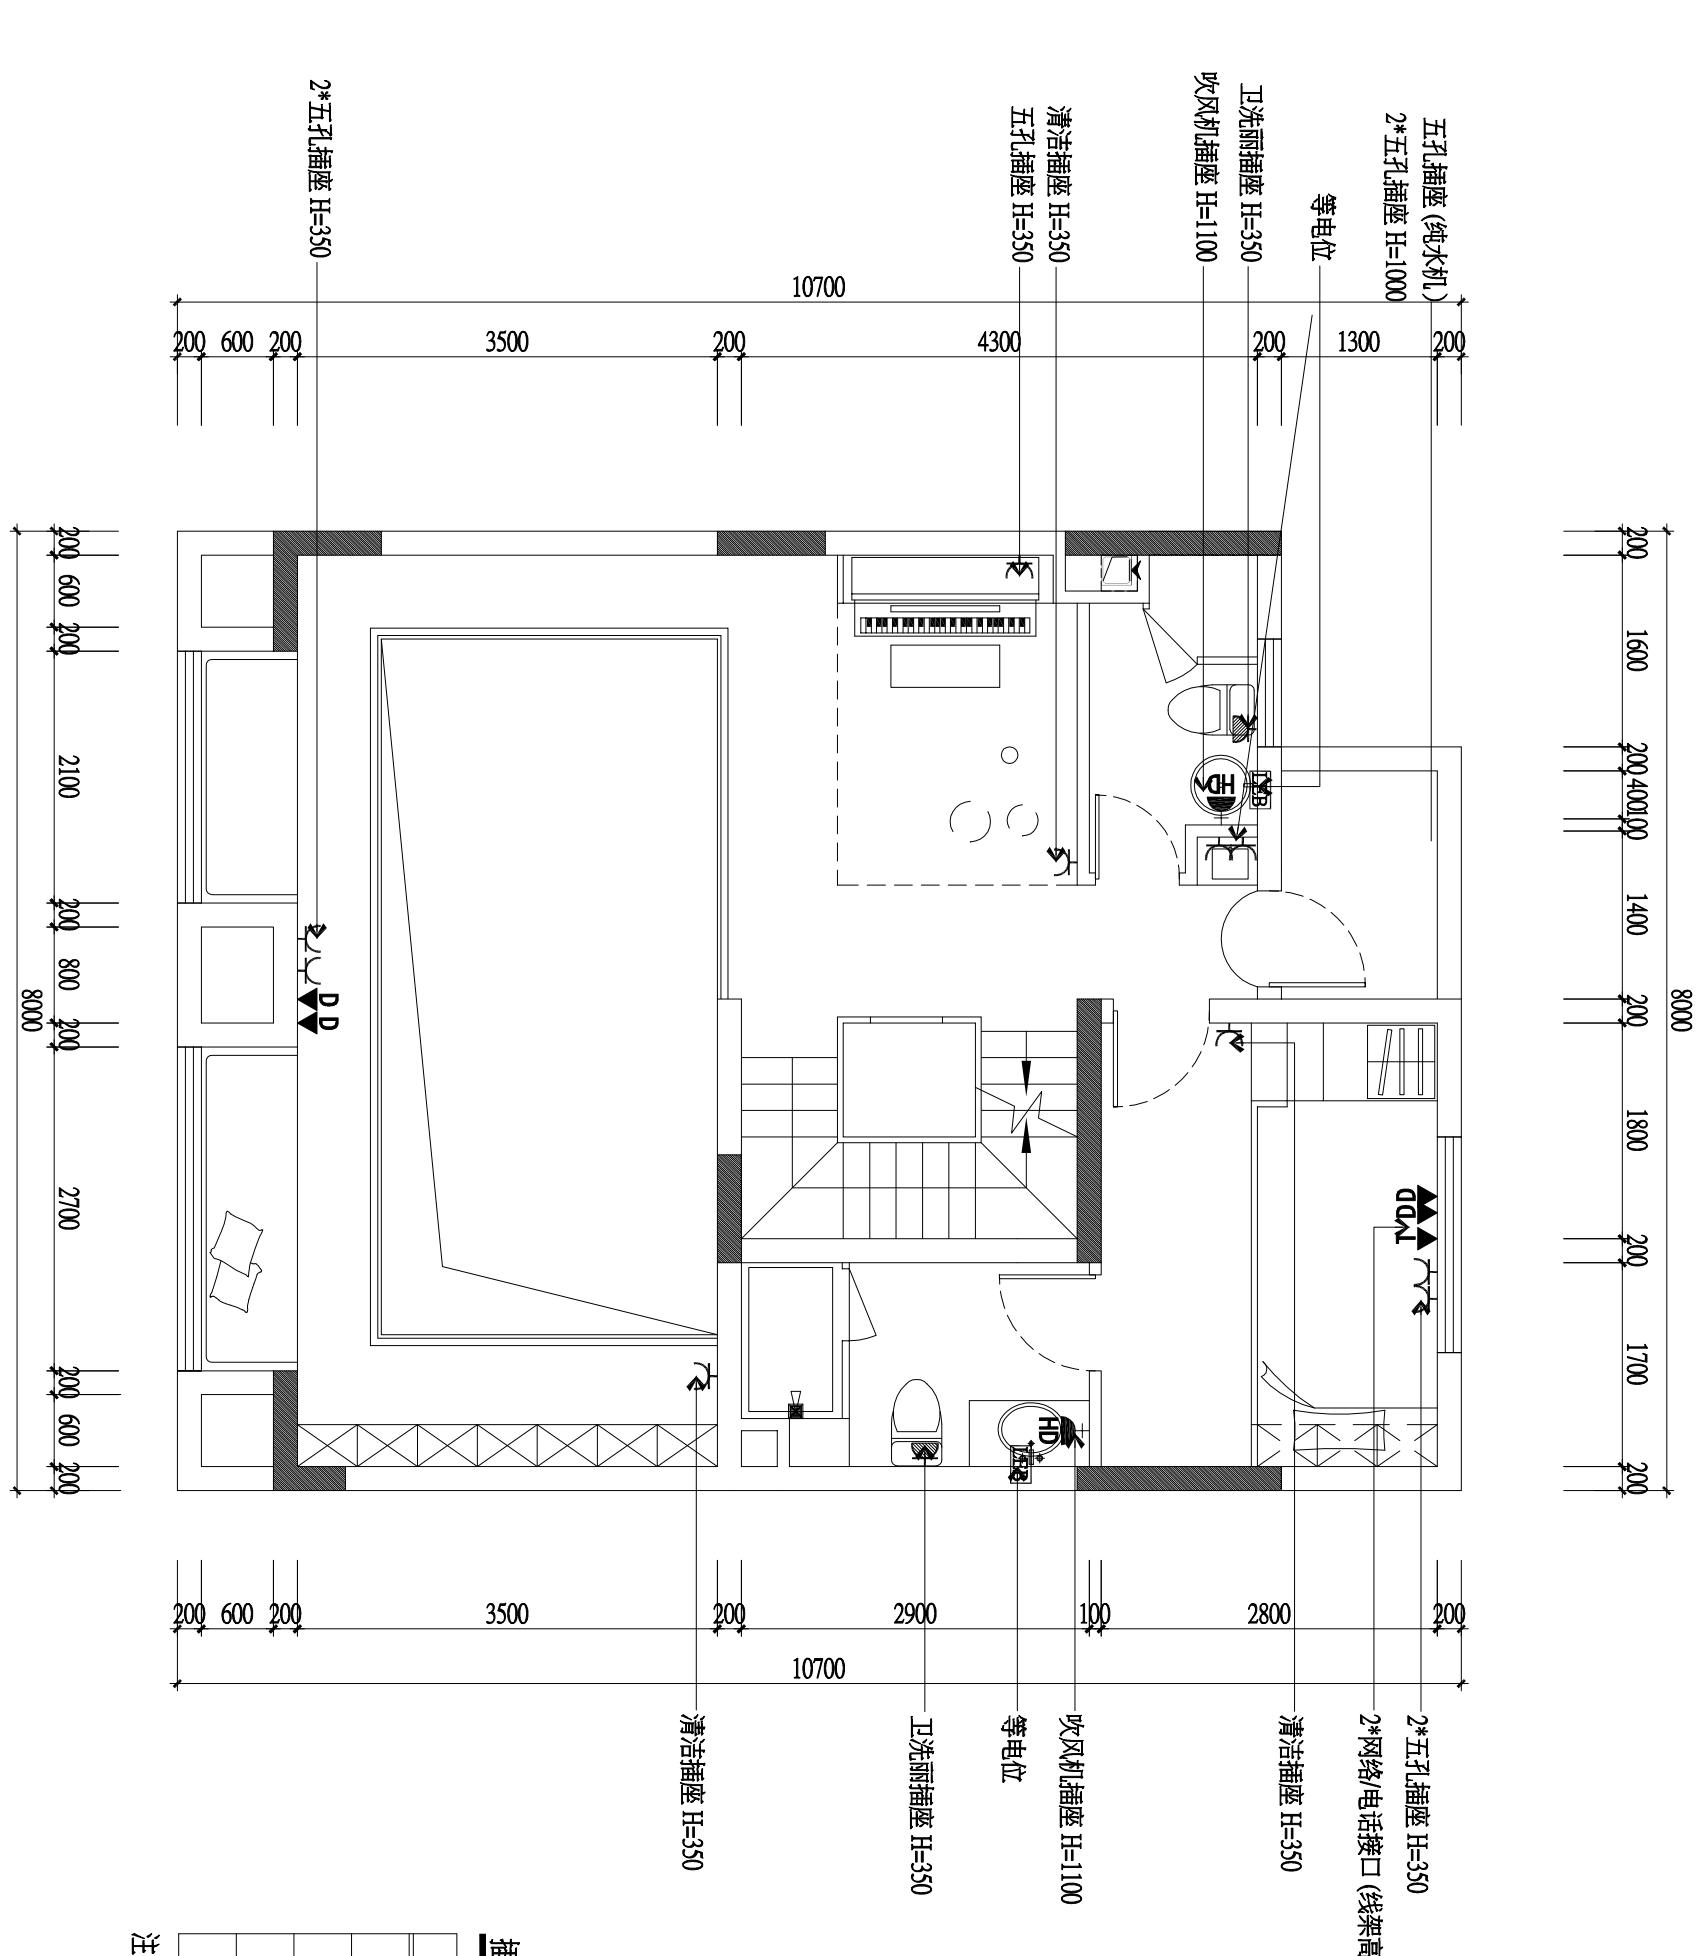

插座说明

图例	名称	图例	名称
△	一、二极单相组合安全插座	□	防水插座
吉+	吹风机	□	地插
↓	电话接口	TV	电视接口
D	网络接口	LEB	等电位

注：开关盒面板间距20mm;所有标高为重心距地

NOTE

□在未经同意前，不得复制图纸及其设计  
任何部分。  
□所有图纸尺寸标注须在实际工地上复核及  
量度。  
□图例按比例量度图纸，应采用已标明的  
尺寸。

是境  
設計

备  
注  
NOTE

□本图版必须和接线说明、合同条款及其  
他有关图纸，并使用，如发现图纸内容  
有不符之处，必须立刻通知设计者。

□所有图纸尺寸标注须在实际工地复核及  
量度。  
□请勿按比例量度图纸，应采用已标明的  
尺寸。

业  
主  
CLIENT

项  
目  
名  
称  
PROJECT

龙湖椿山

总  
负  
责  
人  
PRINCIPAL

设  
计  
师  
DESIGNER

绘  
图  
DRAWM BY

校  
对  
COLLATE

审  
核  
APPROVE

比  
例  
SCALE

日  
期  
DATE

图  
名  
DRAWING TITLE


2F开关布置图

图  
号  
SHEET NO

2F.P-10

图例	名称	图例	名称
● ↗	单联单控开关	↙ ●	单联双控+单联单控开关
● ↗ ↗	双联单控开关	↙ ↗ ●	双联双控开关
● ↗ ↗ ↗	三联单控开关	↙ ↗ ↗ ●	三联双控开关
↙ ↗ ↗ ↗	单联双控开关	■ AC	空调开关

注：开关盒面板间距20mm;所有标高为  
中心距地。

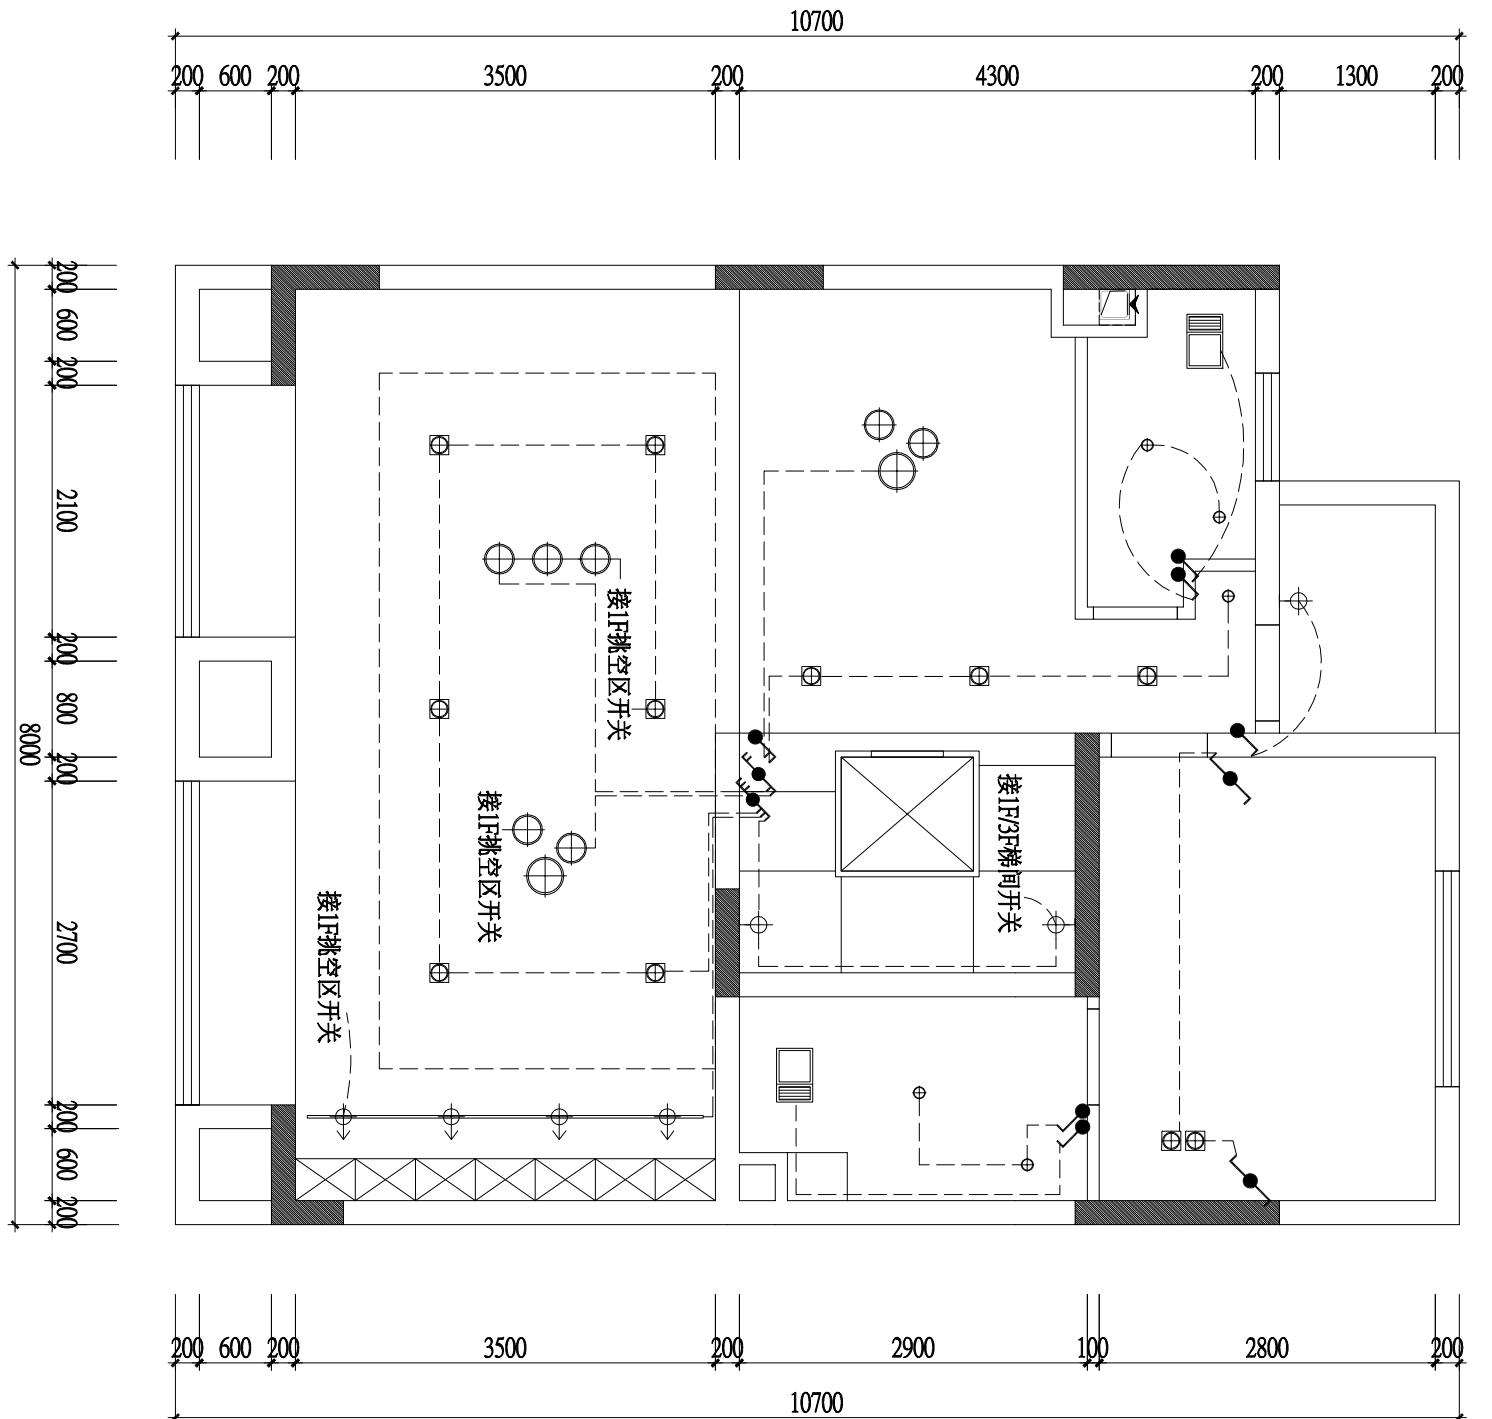


照明灯具说明：

是  
境  
設  
計

10 2F开关布置图  
SCALE:1:60

NOTE  
 ①本图版必须和总图说明、合同条款及其  
 其他有关图纸，并使用，如发现图纸内容  
 有不符之处，必须立刻通知设计者。  
 ②请勿比例量度图纸，应采用已标明的  
 尺寸。

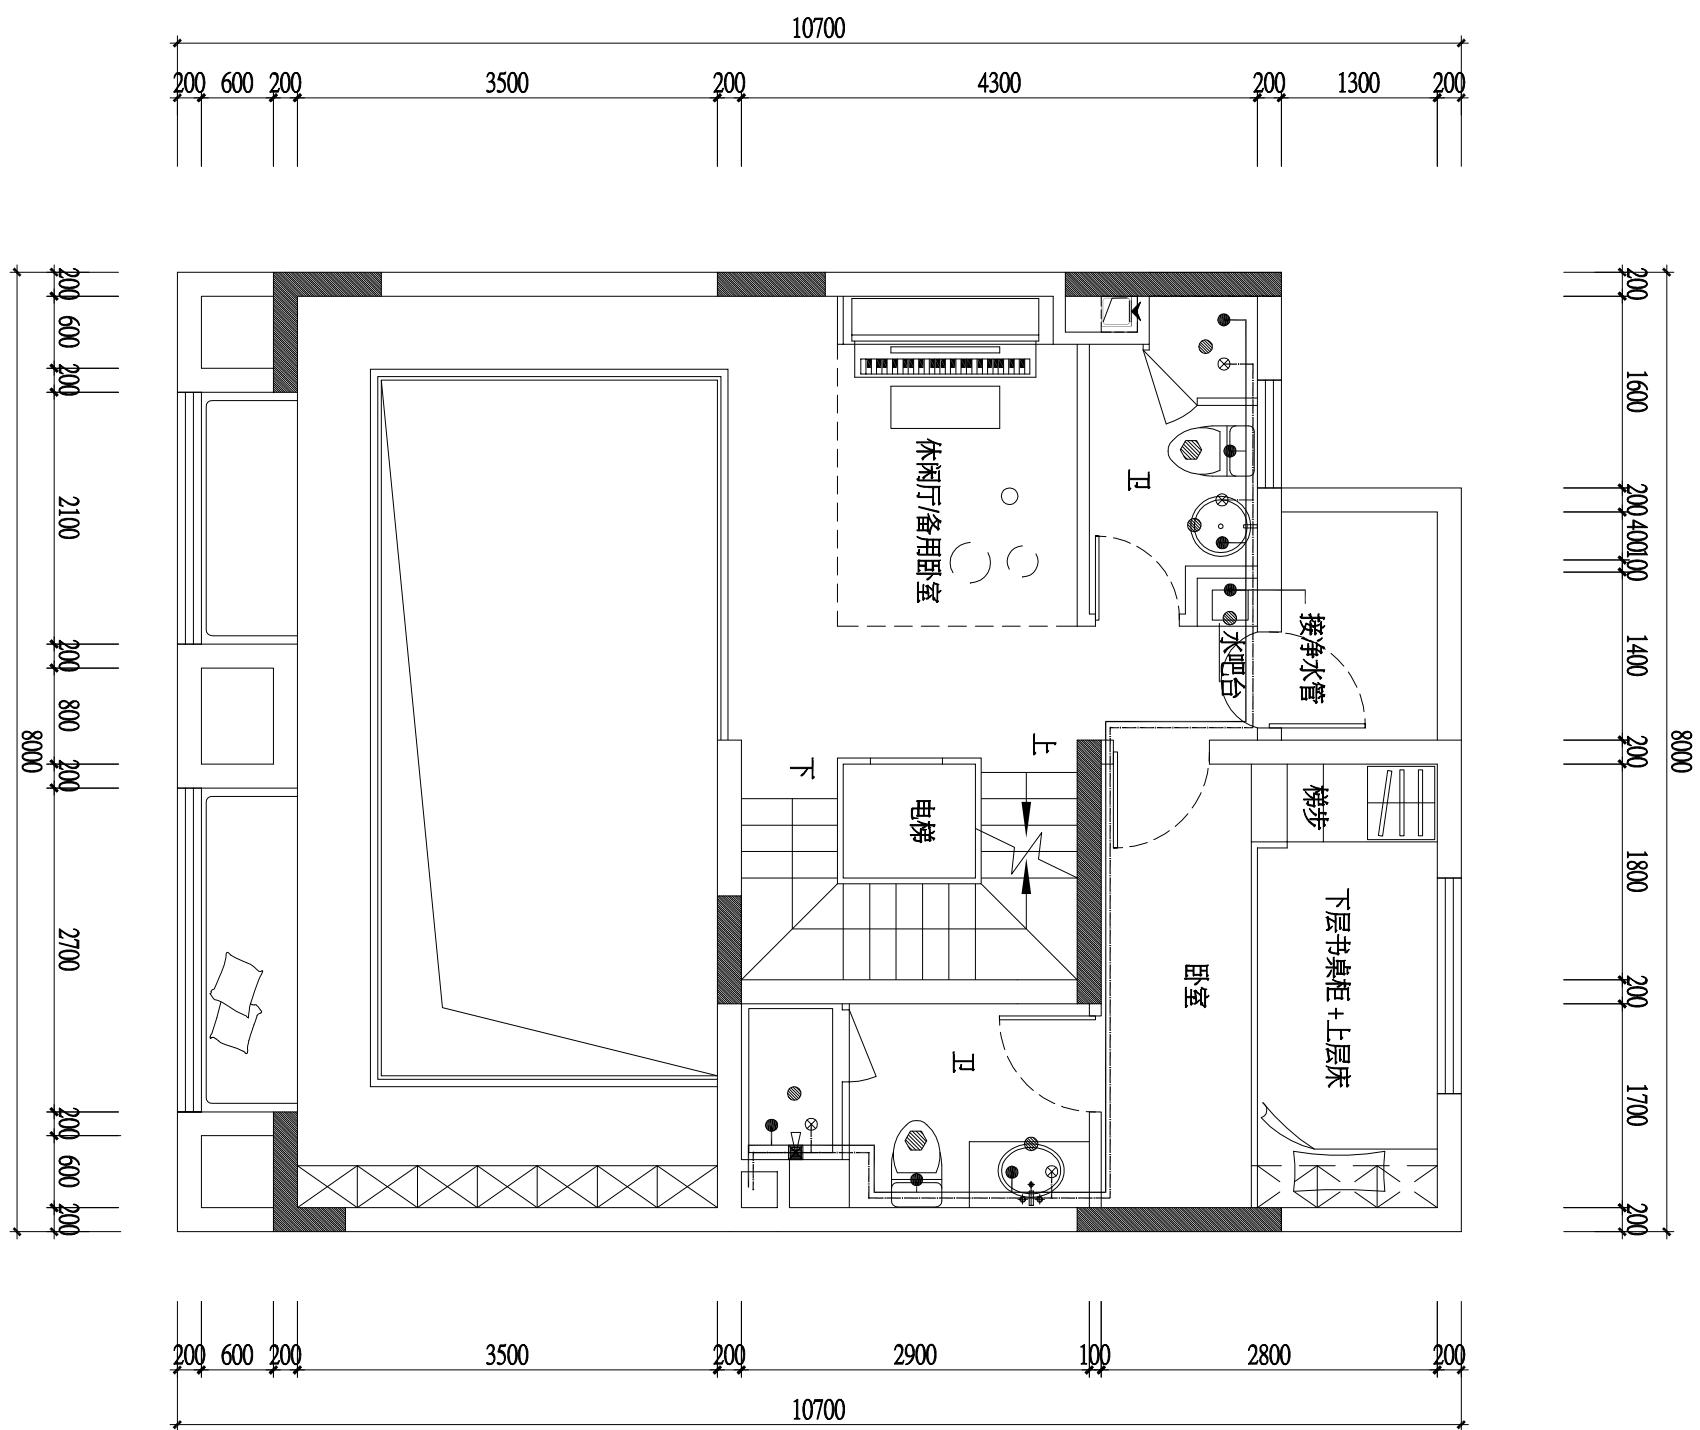

注：室内水管均从梁底最高处走，冷热水管直径25mm，排水管直径50mm。

给排水说明：

图例	名称	图例	名称
●	给水口	①	墙排水
⊗	热水上水口	——	热水管
●	排水口	——	给水管
◎	马桶排水口	□	热水器

2F水路布置图

图号  
SHEET NO  
2F.P-11

图名  
DRAWING TITLE

是境  
设计

11 2F水路布置图  
SCALE:1:60

备 注  
①本图版必须和总图说明、合同条款及其  
 其他有关图纸，并使用，如发现图纸内容  
 有不符之处，必须立刻通知设计者。  
 ②请勿比例量度图纸，应采用已标明的  
 尺寸。

□在未经同意前，不得复制图纸及其设计  
NOTE

在未经同意前，不得复制图纸及其设计任何部份。

□ 所有图纸尺寸标注须在实际工地复核及  
量度。  
□ 请勿按比例量度图纸，应采用已标明的  
尺寸。  
□ 本图纸必须和规格说明、合同条款及其  
他有关图纸，并使用，如发现图纸内容  
有不符之处，必须立刻通知设计院。

CL  
IE  
NT

项目名称  
PROJECT

总负

1

14

DRAWN BY

COLLATE

APPROVE

SCALE

日  
DATE

圖  
名

3F  
原版

---

1

SHEET N  
四

3E

1

---

1

1

1

三

三

五

This figure shows an architectural floor plan of a building section. The top horizontal dimension is 10700, divided into segments of 200, 1600, 200, 2500, 200, 1000, 200, 1600, 200, 1300, 1500, and 200. The left vertical dimension is 8000, with segments of 200, 4000, 100, 3500, and 200. The right vertical dimension is 8000, with segments of 200, 2500, 200, 3000, 200, 1700, and 200. The bottom horizontal dimension is 10700, divided into segments of 200, 2100, 100, 2100, 200, 400, 200, 2200, 200, 1300, 1500, and 200. The plan includes several rooms labeled in Chinese: 阳台 (Balcony) on the left, 卫生间 (Bathroom) below it, 衣帽间 (Closet) next to the bathroom, 卧室 (Bedroom) at the top left, 储物 (Storage) in the center, and 露台 (Terrace) on the far right. A staircase is located in the lower center. Dark shaded areas represent structural elements or walls.


00 - 3F 原始平面图  
SCALE:1/60

□在未经同意前，不得复制图纸及其设计  
NOTE

④所有图纸尺寸标注须在实际工地上复核及量度。


業主  
CLIENT

项 目 名 称 PROJECT	龙 湖 镇 山		
总 负 责 PRINCIPAL	设 计 DESIGNER	绘 图 DRAWN BY	校 对 COLLATE
审 核 APPROVE	比 例 SCALE	日 期 DATE	图 名 DRAWING TITLE
3F墙 体 打 除 [图]	1 : 60	2020.07	3F.P-01
图 号 SHEET NO			

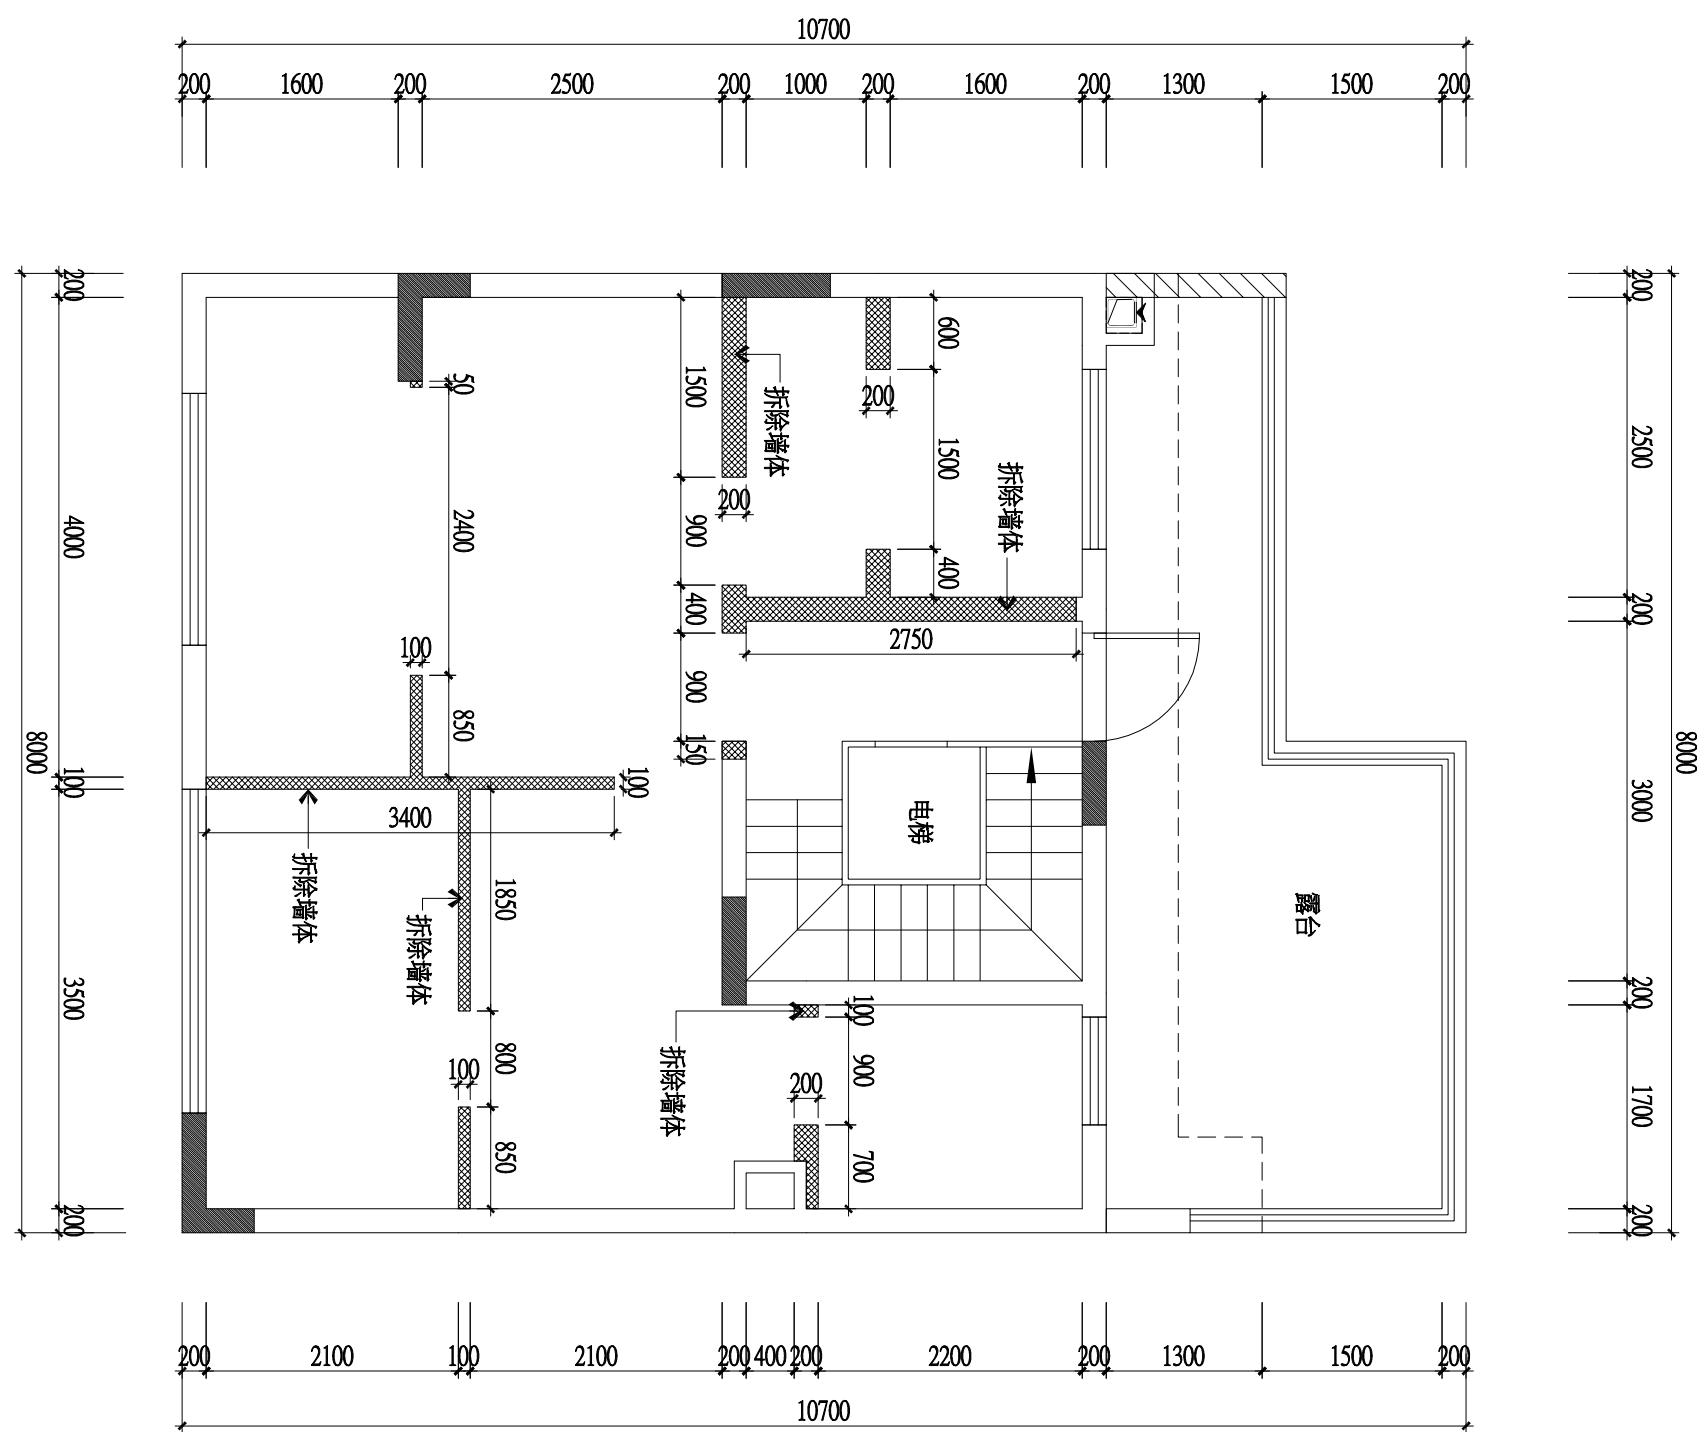

01  
3F墙体拆除图  
SCALE:1/60

备注	
□本图版必须和箱格说明、合同条款及其 附件部分。不得复制图纸及其设计 任何部分。	
□所有图纸尺寸标注须在实际工地复核及 量度。	
□请勿按比例量度图纸，应采用已标明的 尺寸。	
□本图纸必须和箱格说明、合同条款及其 附件部分。不得复制图纸及其设计 任何部分。	
□所有图纸尺寸标注须在实际工地复核及 量度。	
□请勿按比例量度图纸，应采用已标明的 尺寸。	

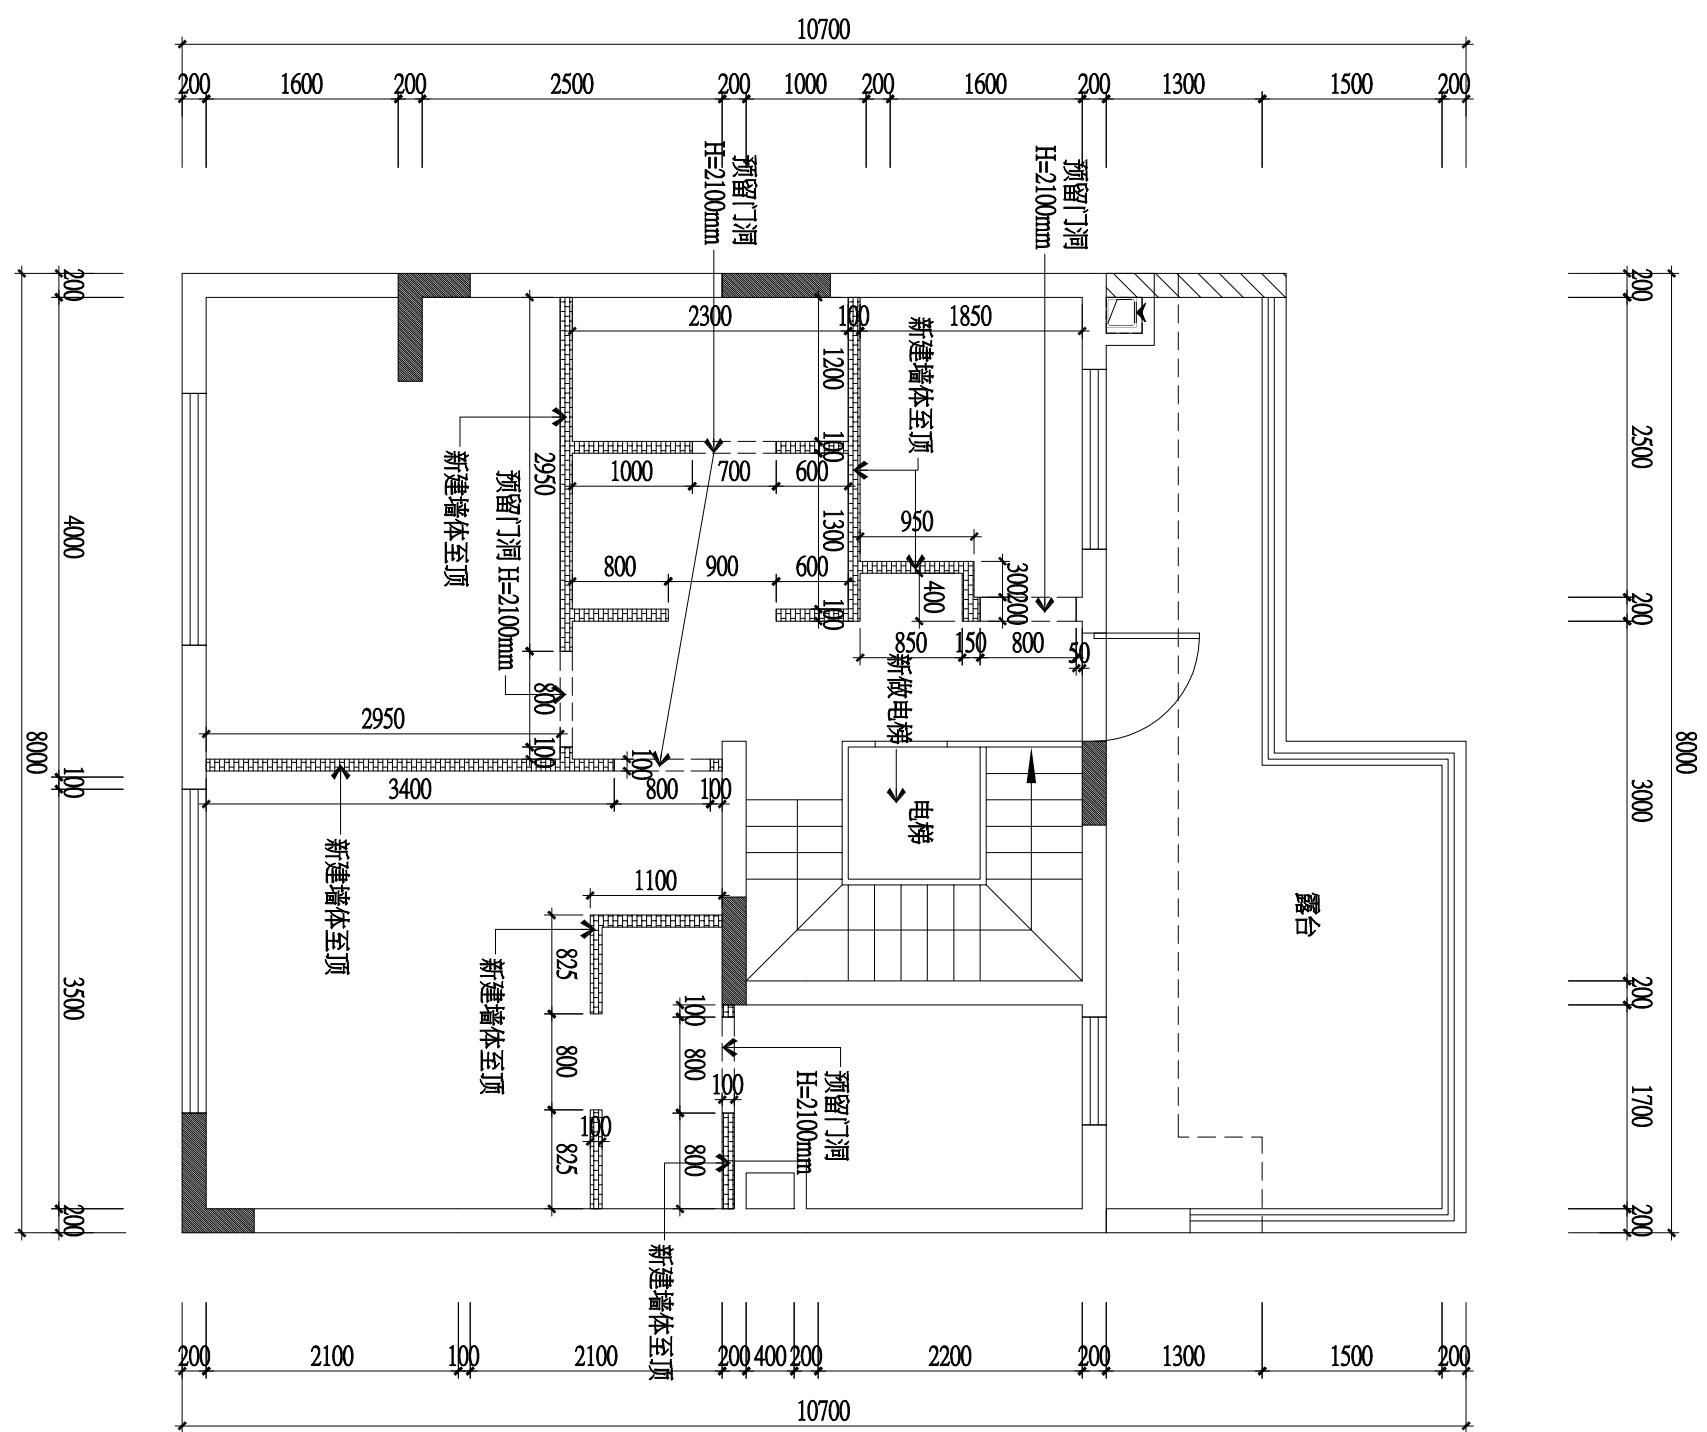

02 3F墙体新建图  
SCALE:1:60

是境  
设计  
语言

图  
号

SHEET NO

3F.P-02

图  
名

DRAWING TITLE

3F墙体新建图

备 注  
NOTE  
□在未经同意前，不得复制图纸及其设计  
任何部分。  
□所有图纸尺寸标注须在实际工地上复核及  
量度。  
□请勿按比例量度图纸，应采用已标明的  
尺寸。

□本图纸必须和规格说明、合同条款及其  
他有关图纸，并使用《建筑制图标准》内  
容有不符之处，必须立刻通知设计者。

业 主	CLIENT
项 目 名 称	PROJECT

龙湖椿山

总 负 责  
PRINCIPAL

设 计  
DESIGNER

绘 图  
DRAWN BY

校 对  
COLLATE

审 核  
APPROVE

比 例  
SCALE

1 : 60

日 期  
DATE


2020.07

DRAWING TITLE

3F平面布置图

图 号  
SHEET NO

3F.P-03

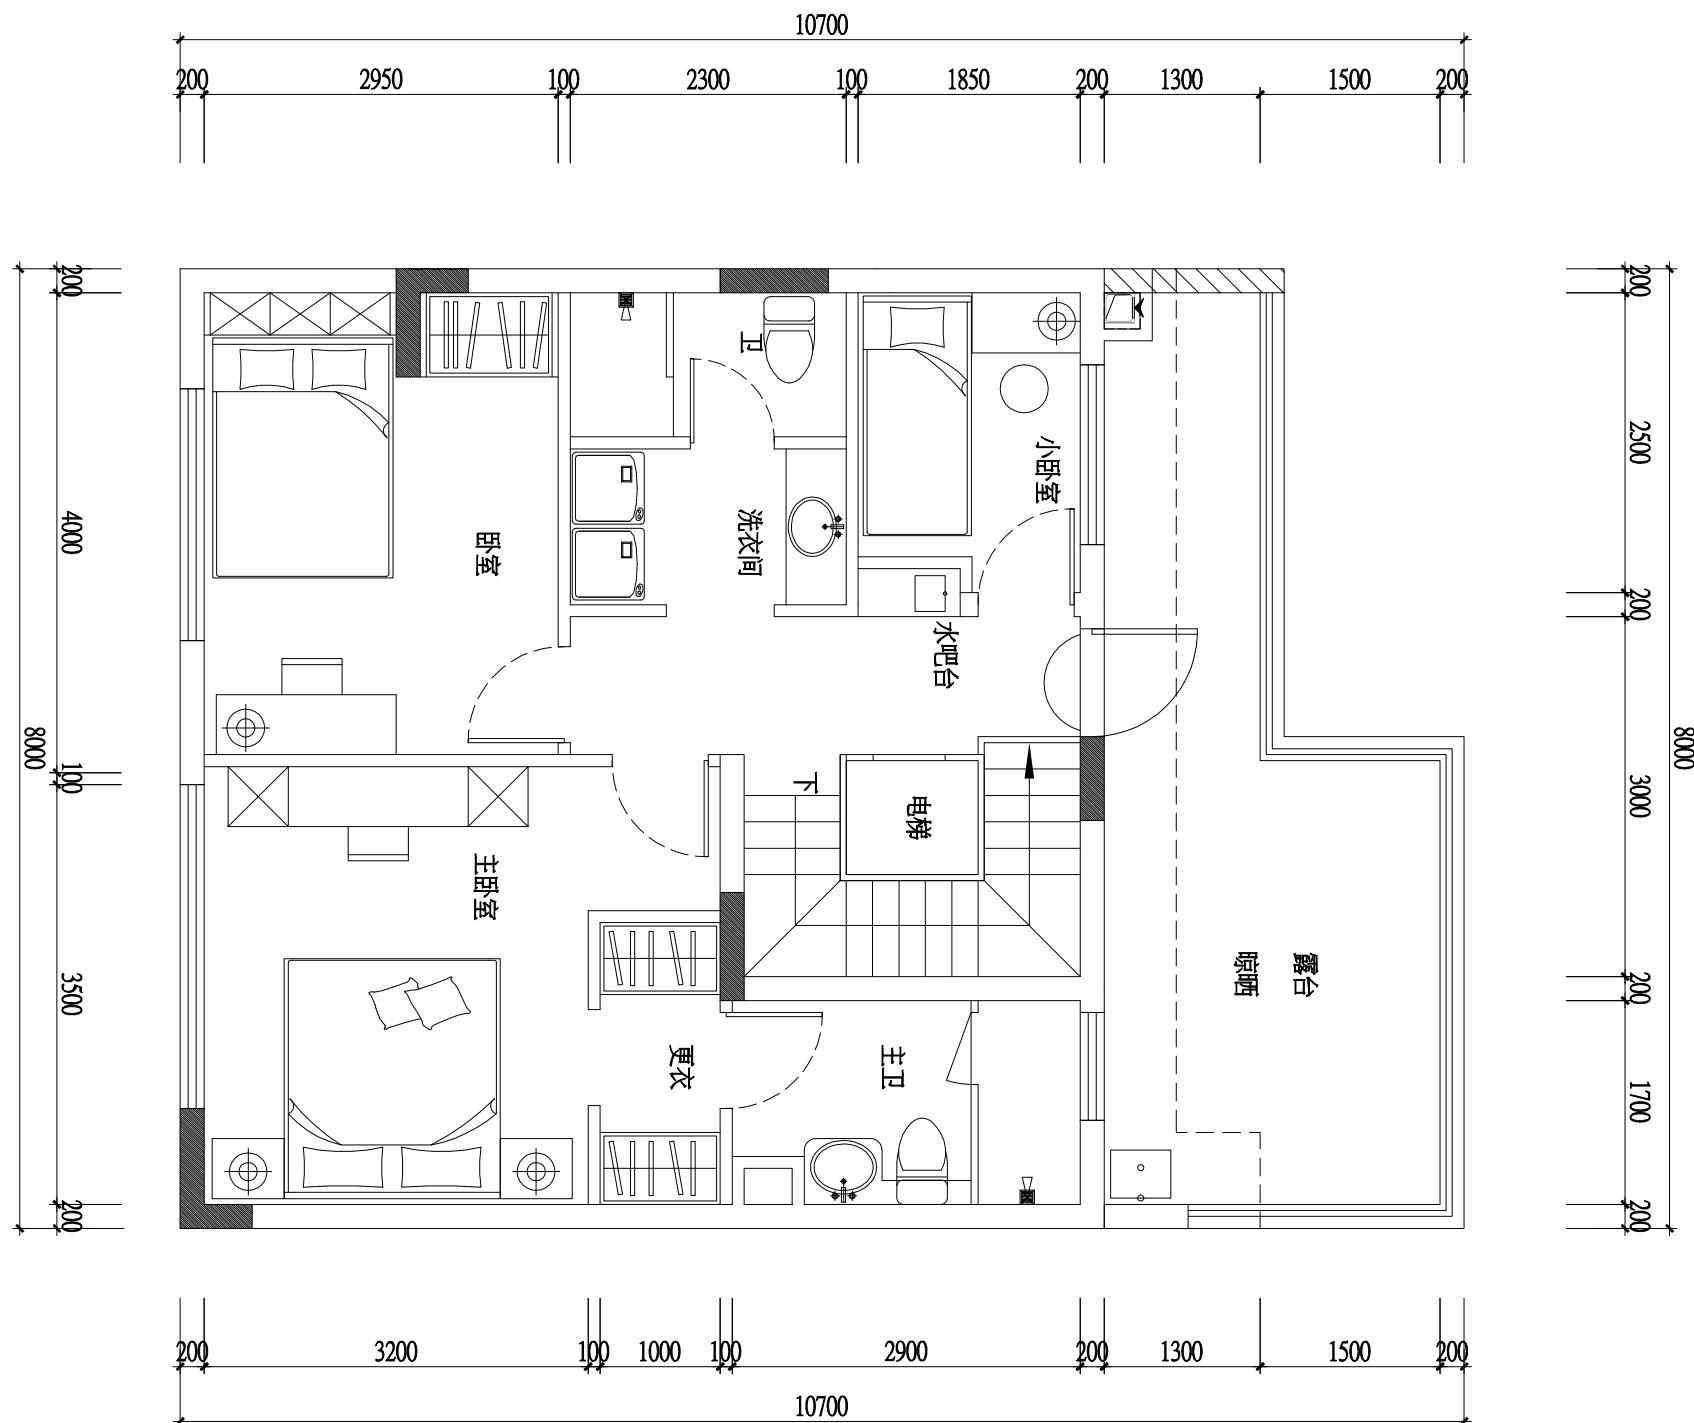


备注

□在未经同意前，不得复制图纸及其设计  
任何部份。

□所有图纸尺寸标注须在实际工地上复核及量度。  
□请按比例量度图纸，应采用已标明的尺寸。

业主  
CLIENT

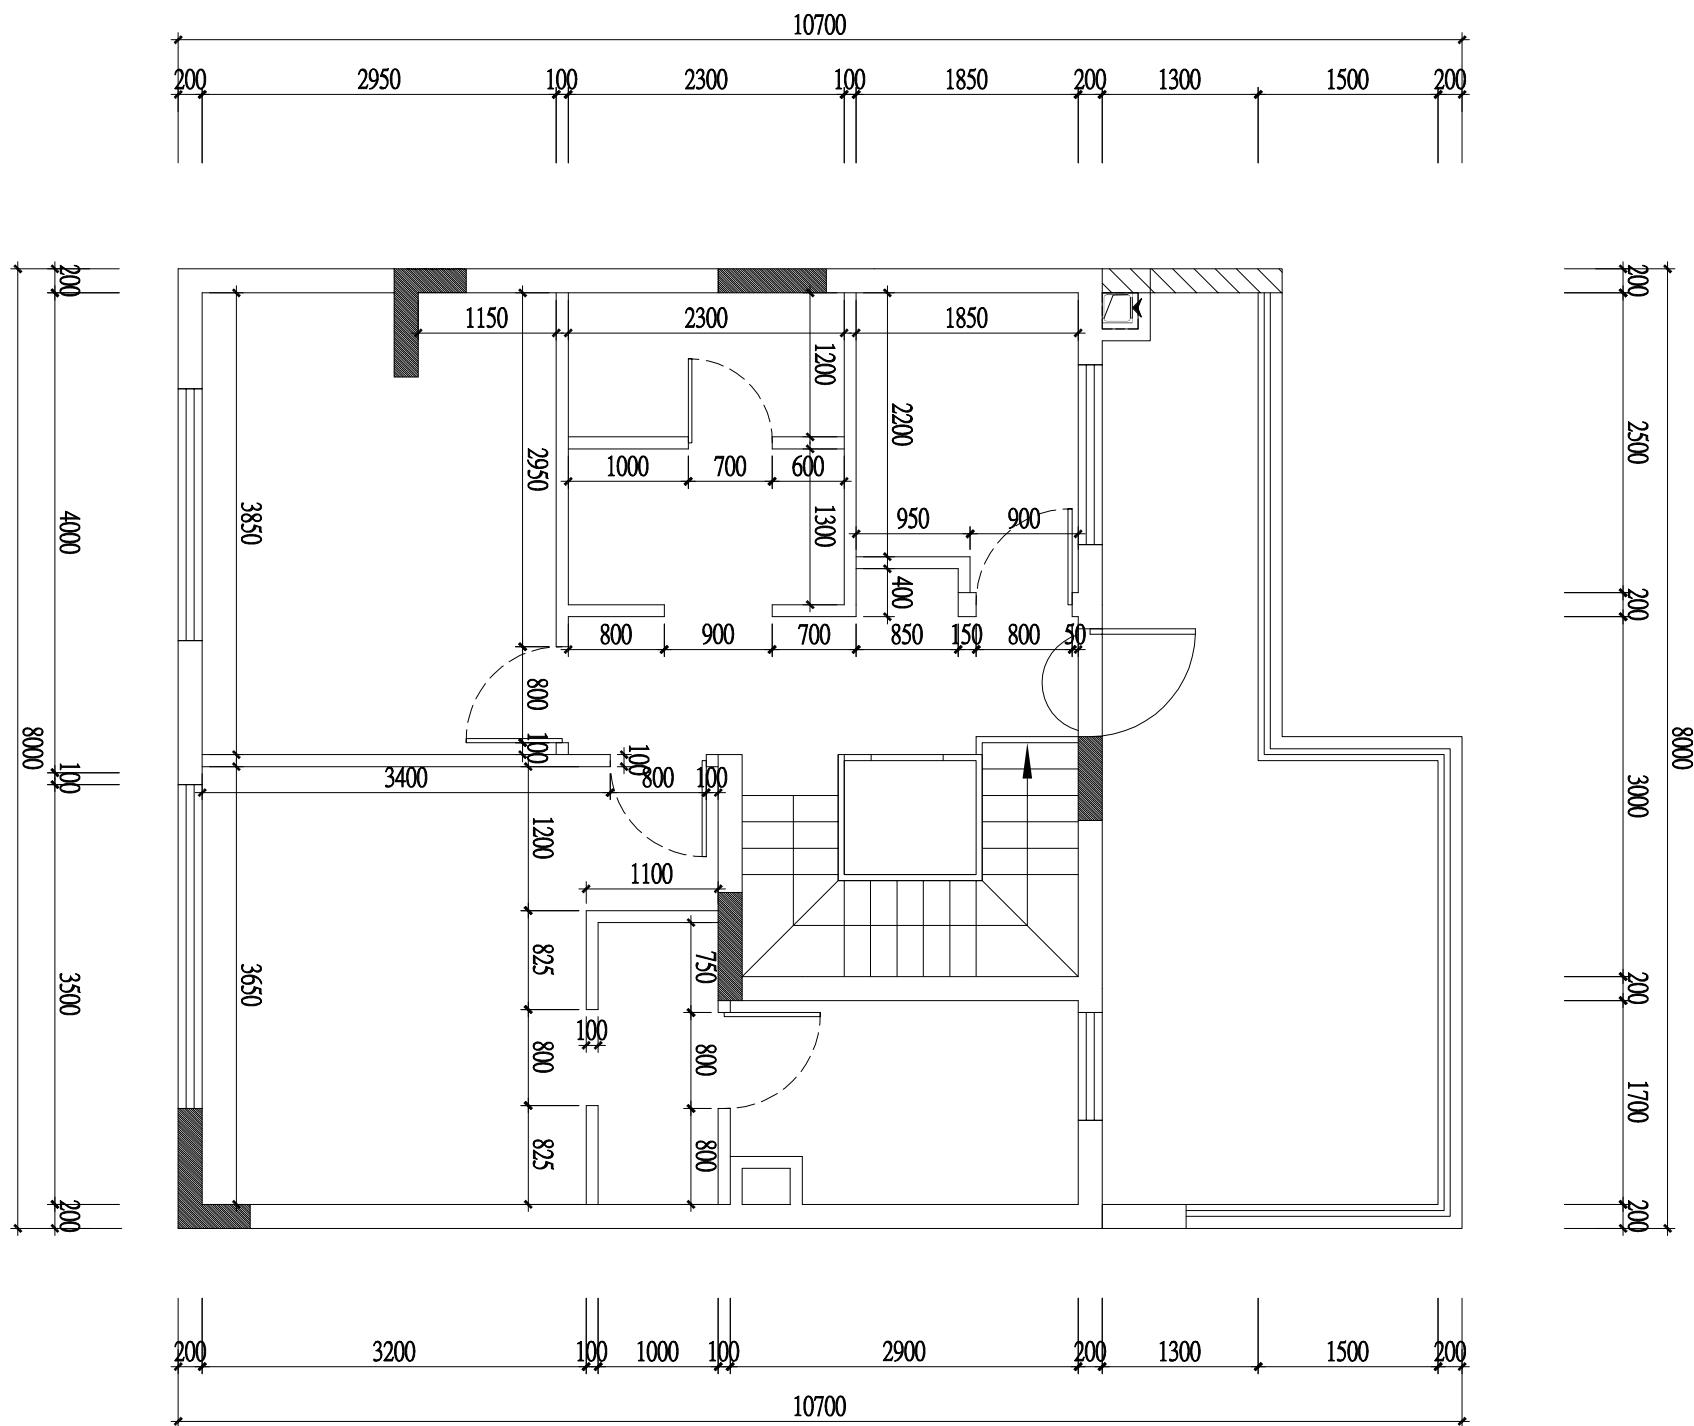


04  
3F隔墙尺寸图  
SCALE:1/60

是境設計

备  
注  
NOTE

□在未经同意前，不得复制图纸及其设计  
任何部分。  
□所有图纸尺寸标注须在实际工地上复核及  
量度。  
□请勿按比例量度图纸，应采用已标明的  
尺寸。  
□本图纸必须和规格说明、合同条款及其  
他有关图纸，并使用《建筑及装饰工程图示  
内容与表示方法》规定图纸内容  
有不符之处，必须立刻通知设计者。

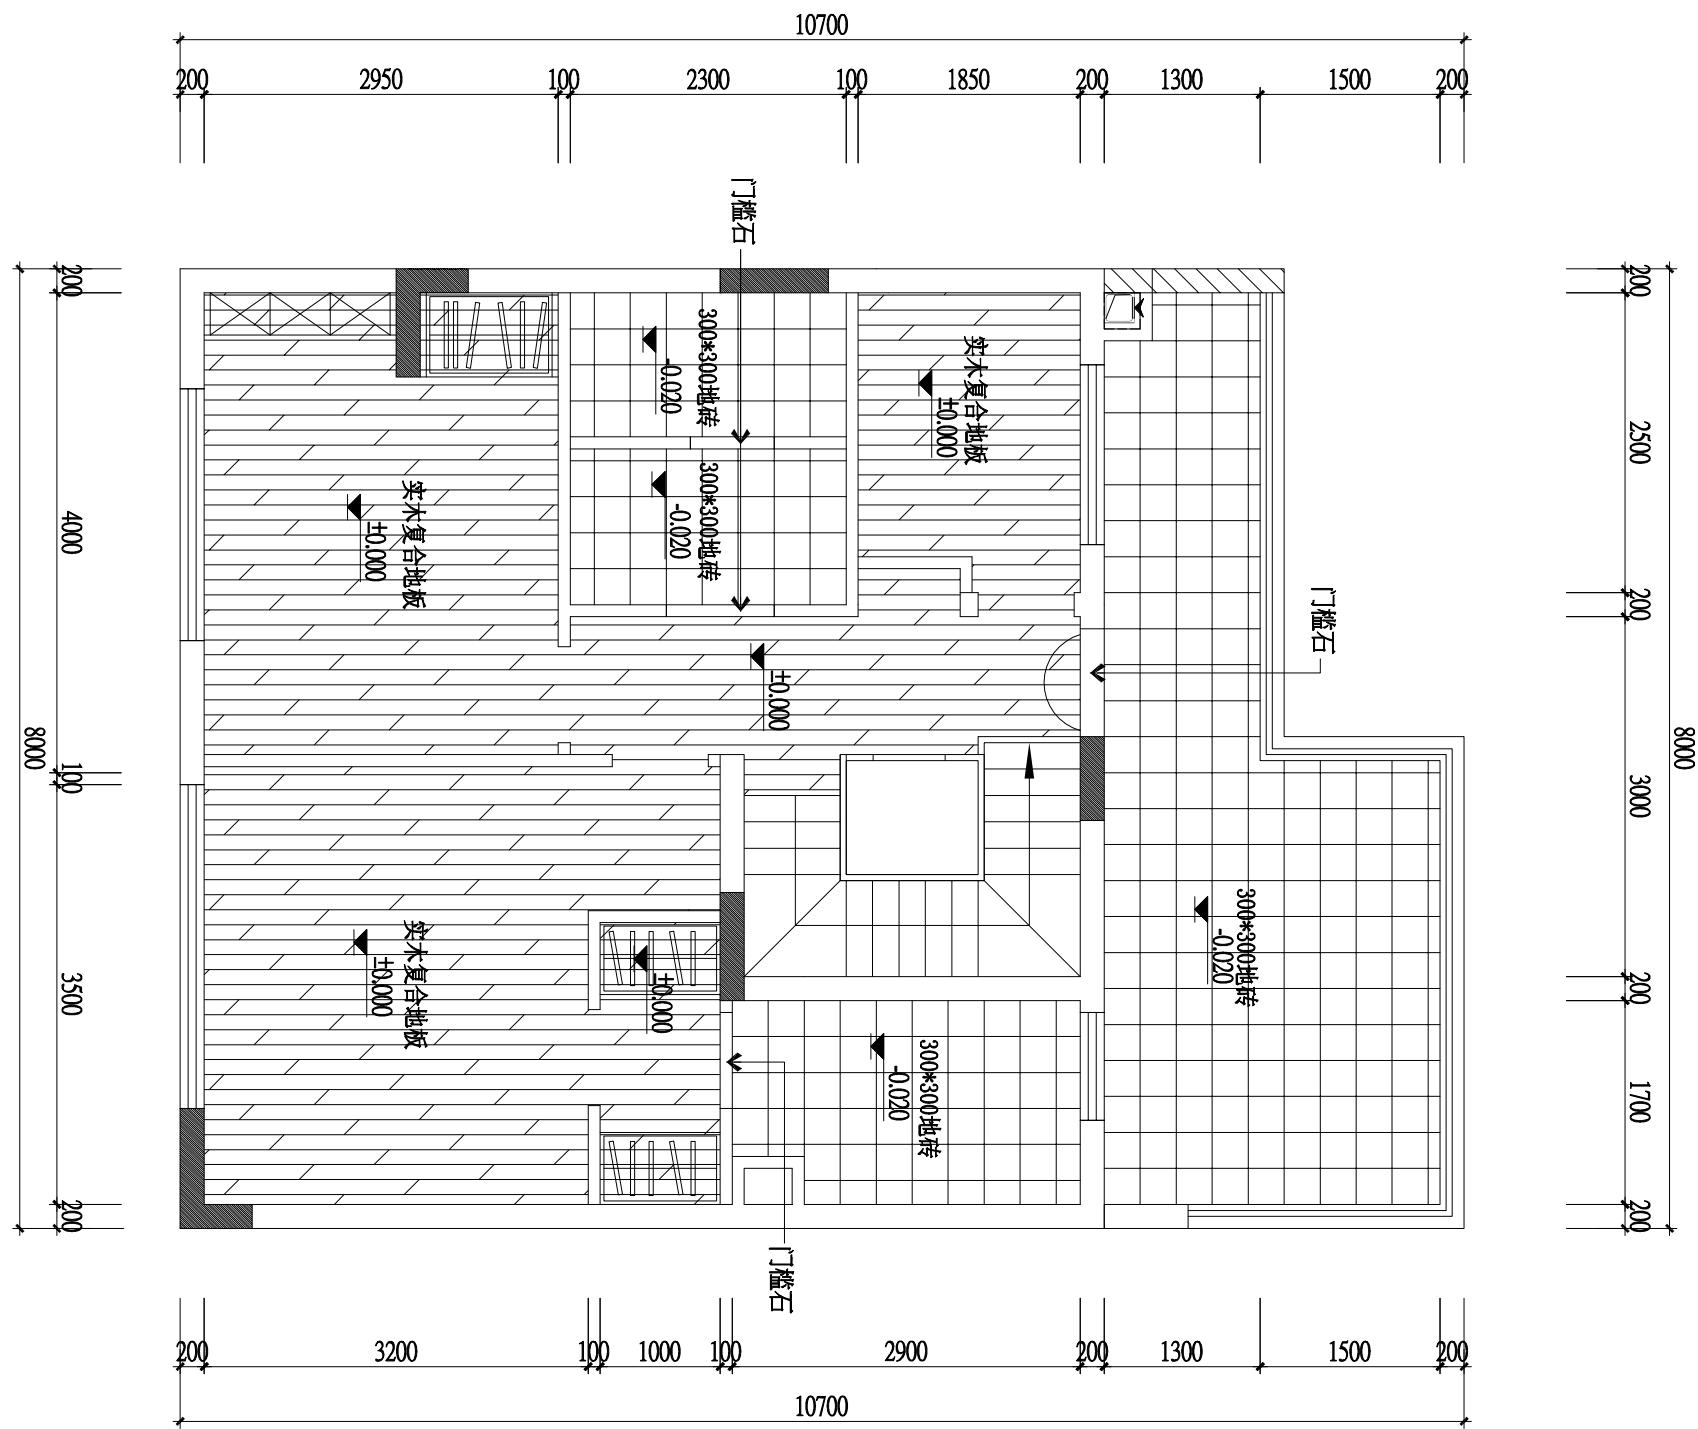

05  
3F地面材质图  
SCALE:1:60

是  
境  
設  
計

3F地面材质图  
图号  
SHEET NO

3F.P-05

业 主	CLIENT
项 目 名 称	PROJECT
总 负 责	PRINCIPAL
设 计	DESIGNER
绘 图	DRAWN BY
校 对	COLLATE
审 核	APPROVE
比 例	SCALE 1 : 60
日 期	DATE 2020.07
图 名	DRAWING TITLE

备 注  
NOTE  
□在未经同意前，不得复制图纸及其设计  
任何部分。  
□所有图纸尺寸标注须在实际工地上复核及  
量度。  
□请勿按比例量度图纸，应采用已标明的  
尺寸。

□本图纸必须和规格说明、合同条款及其  
他有关图纸，并使用《建筑制图标准》内  
容有不符之处，必须立刻通知设计者。

业 主  
CLIENT

项 目 名 称  
PROJECT

龙湖椿山

总 负 责  
PRINCIPAL

设 计  
DESIGNER

绘 图  
DRAWN BY

校 对  
COLLATE

审 核  
APPROVE

比 例  
SCALE

1 : 60

日 期  
DATE

2020.07


图 名  
DRAWING TITLE

3F立面索引图

图 号  
SHEET NO


3F.P-06

是 境  
設 計

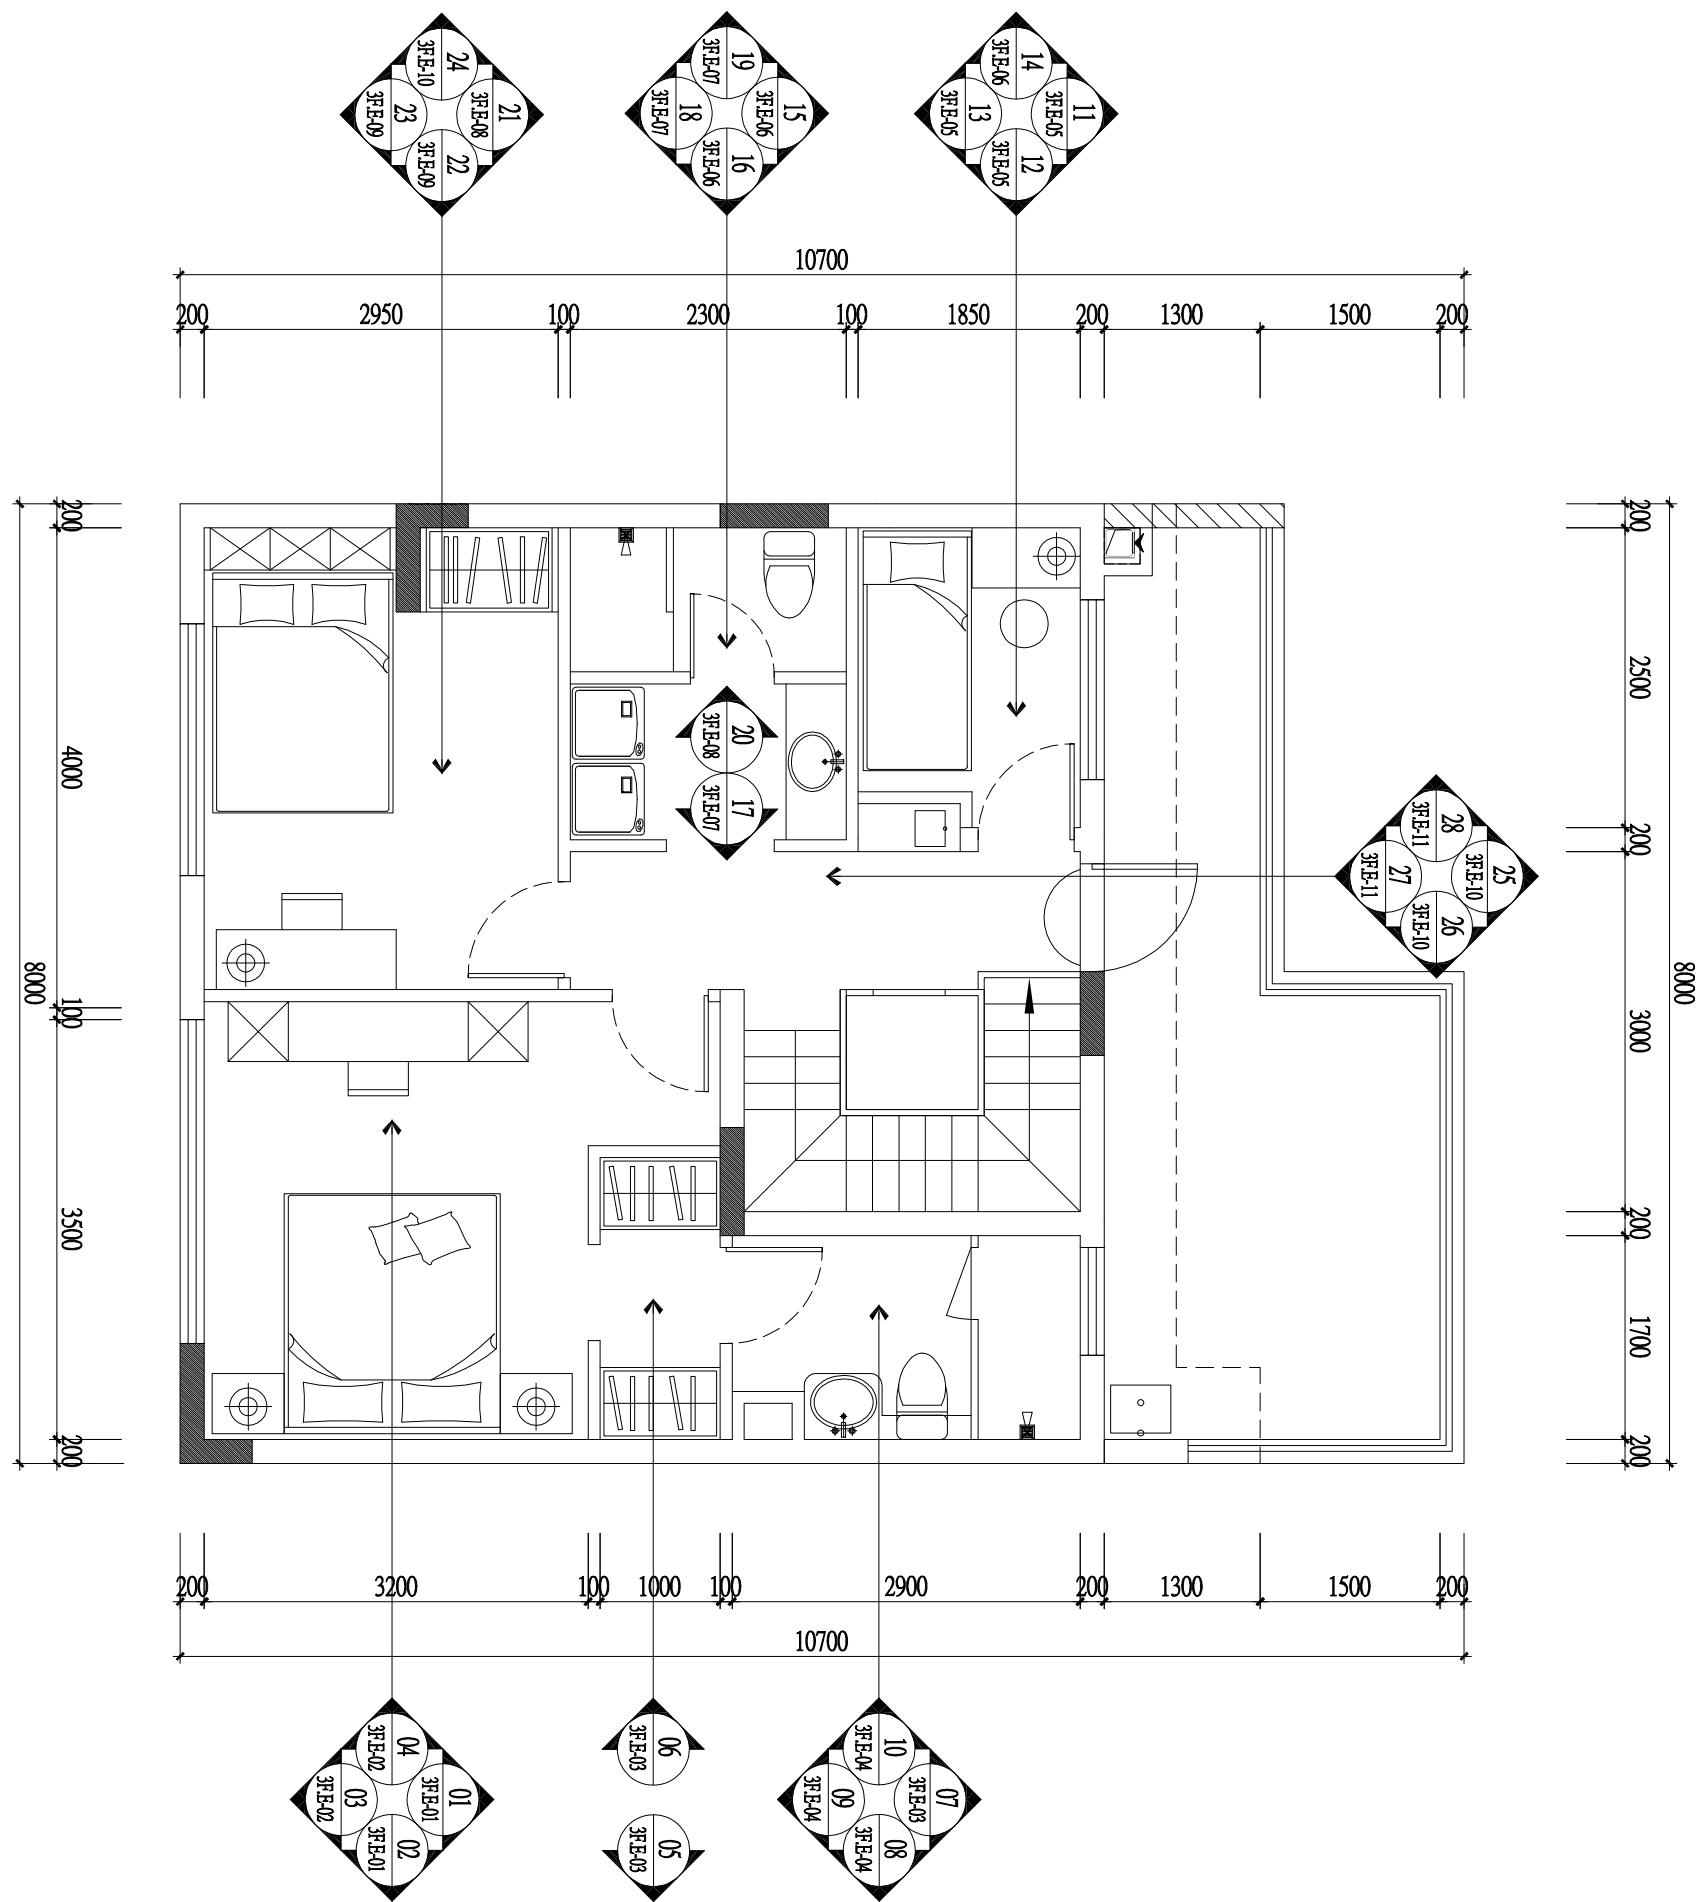

备  
注  
NOTE  
□在未经同意前，不得复制图纸及其设计  
任何部分。  
□所有图纸尺寸标注须在实际工地复核及  
量度。  
□请勿按比例量度图纸，应采用已标明的  
尺寸。

□本图纸必须和规格说明、合同条款及其  
他有关图纸，并使用《建筑及装饰工程图示  
内容与表示方法》之规定，必须立刻通知设计  
师。

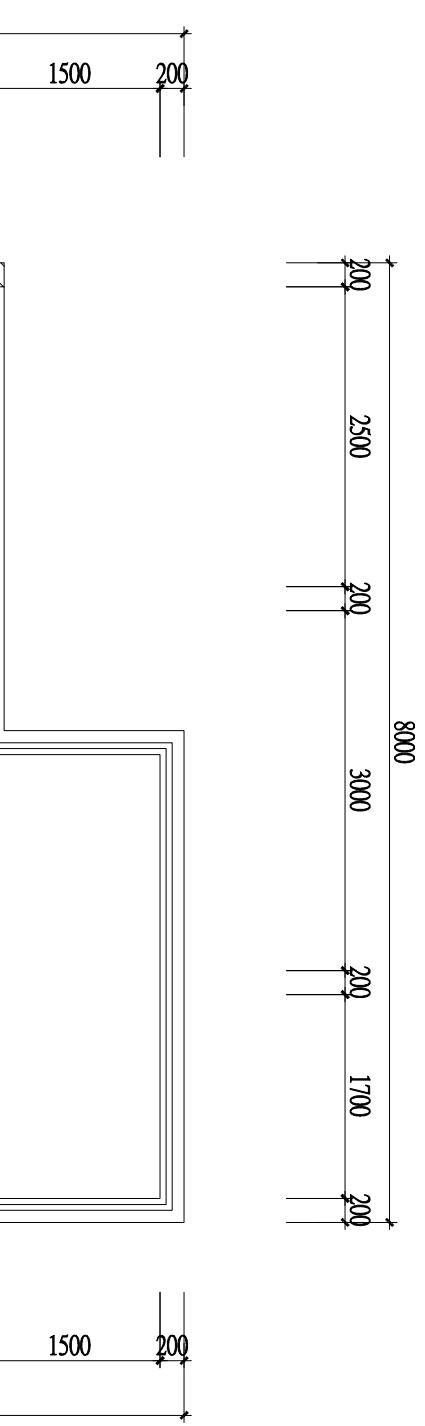

### 照明灯具说明：

图例	名称	图例	名称
⊕	明装筒灯	——	暗藏LED灯带
⊕	防潮筒灯	⊕	壁灯
↑	轨道射灯	⊕⊕	艺术吊灯
⊕	嵌入式筒灯	串	吸顶灯

### 3F天花布置图


图号 SHEET NO  
3F.P-07

是境  
设计


07 3F天花布置图  
SCALE:1:60

备 注  
NOTE  
□在未经同意前，不得复制图纸及其设计  
任何部分。  
□所有图纸尺寸标注须在实际工地复核及  
量度。  
□请勿按比例量度图纸，应采用已标明的  
尺寸。

□本图纸必须和规格说明、合同条款及其  
他有关图纸，并使用，如发现图纸内容  
有不符之处，必须立刻通知设计师。

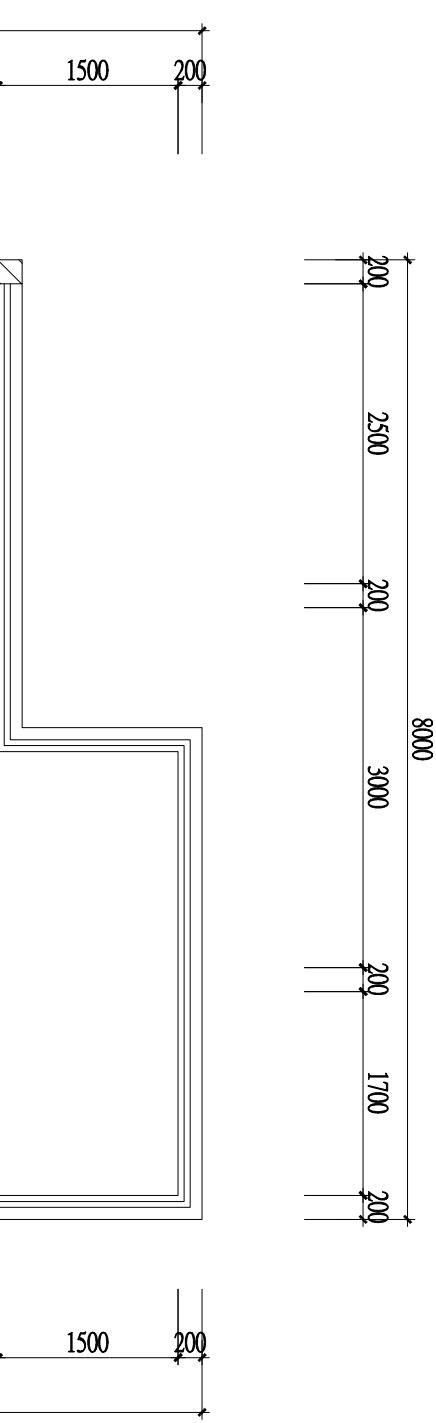

10700

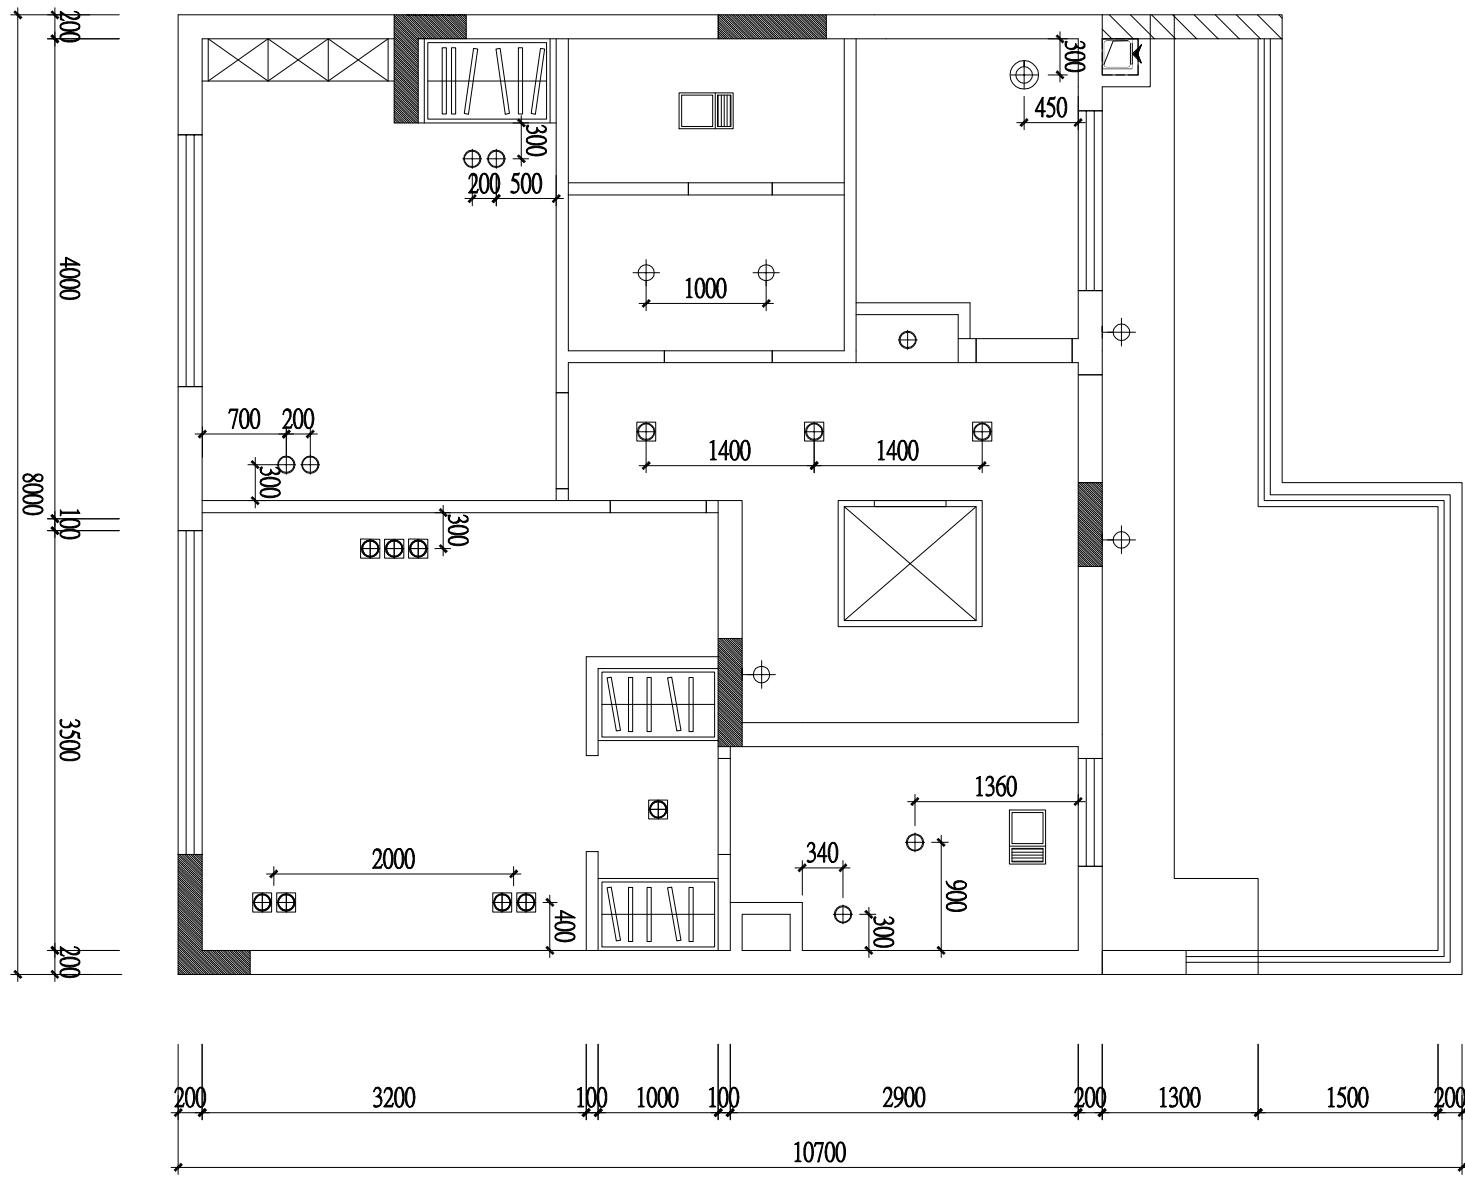

10700

照明灯具说明：

图例	名称	图例	名称
□	明装筒灯	——	暗藏筒灯带
⊕	防潮筒灯	⊕	壁灯
↑	轨道射灯	⊕⊕	艺术吊灯
⊕	嵌入式筒灯	串	吸顶灯

3F天花尺寸图

图 号  
SHEET NO  
3F.P-08


是 境  
設 計

08 3F天花尺寸图  
SCALE:1:60



备注  
NOTE  
□本图版必须和箱格说明、合同条款及其设计任同部分。  
□所有图纸尺寸标注须在实际工地复核及量度。  
□请勿按比例量度图纸，应采用已标明的尺寸。

□本图版必须和箱格说明、合同条款及其设计任同部分，并使用。如发现图纸内容有不符之处，必须立刻通知设计者。

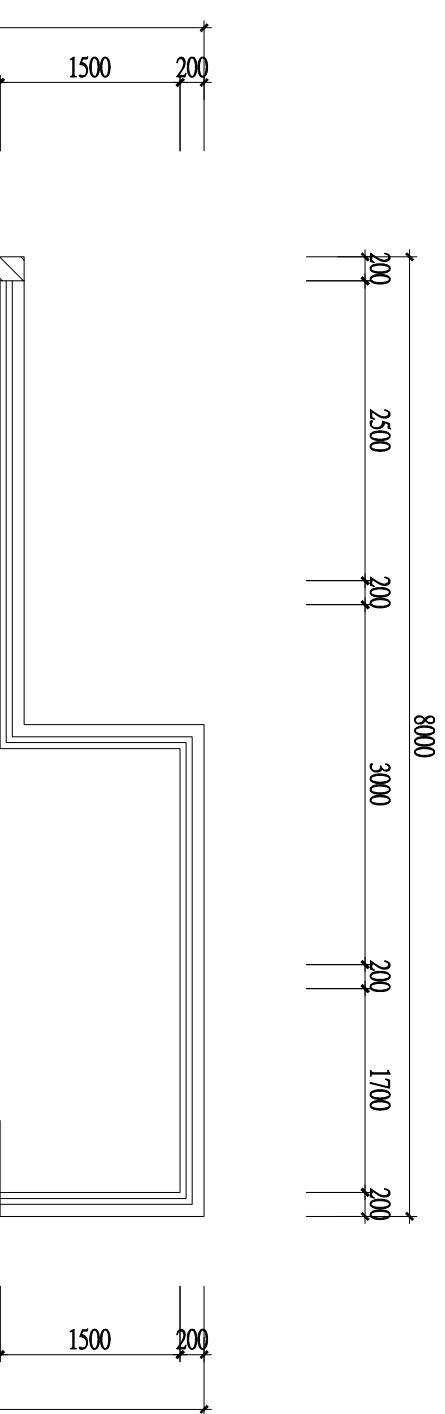

### 照明灯具说明：

图例	名称	图例	名称
● ↗	单联单控开关	↙ ●	单联双控+单联单控开关
● ↗ ↗	双联单控开关	↙ ↗ ●	双联双控开关
● ↗ ↗ ↗	三联单控开关	↙ ↗ ↗ ●	三联双控开关
↙ ↗	单联双控开关	■ AC	空调开关

注：开关盒面板间距20mm;所有标高为中距地。

### 3F开关布置图

图号 SHEET NO  
3F.P-10

是境  
设计

备注  
NOTE  
□本图未经同意，不得复制图纸及其设计任一部分。  
□所有图纸尺寸标注须在实际工地复核及量度。  
□请勿按比例量度图纸，应采用已标明的尺寸。

□本图纸必须和报批说明、合同条款及其他有关图纸，并使用《建筑制图标准》规定的内容有不符之处，必须立刻通知设计单位。

业主 主  
CLIENT

项目名称  
PROJECT

龙湖椿山

总负责  
PRINCIPAL

设计师  
DESIGNER

绘图  
DRAWN BY

校对  
COLLATE

审核  
APPROVE

核对  
COLLATE

比倒  
SCALE

例 1 : 60

日期  
DATE


2020.07

图名  
DRAWING TITLE

3F水路布置图

图号  
SHEET NO

3F.P-11

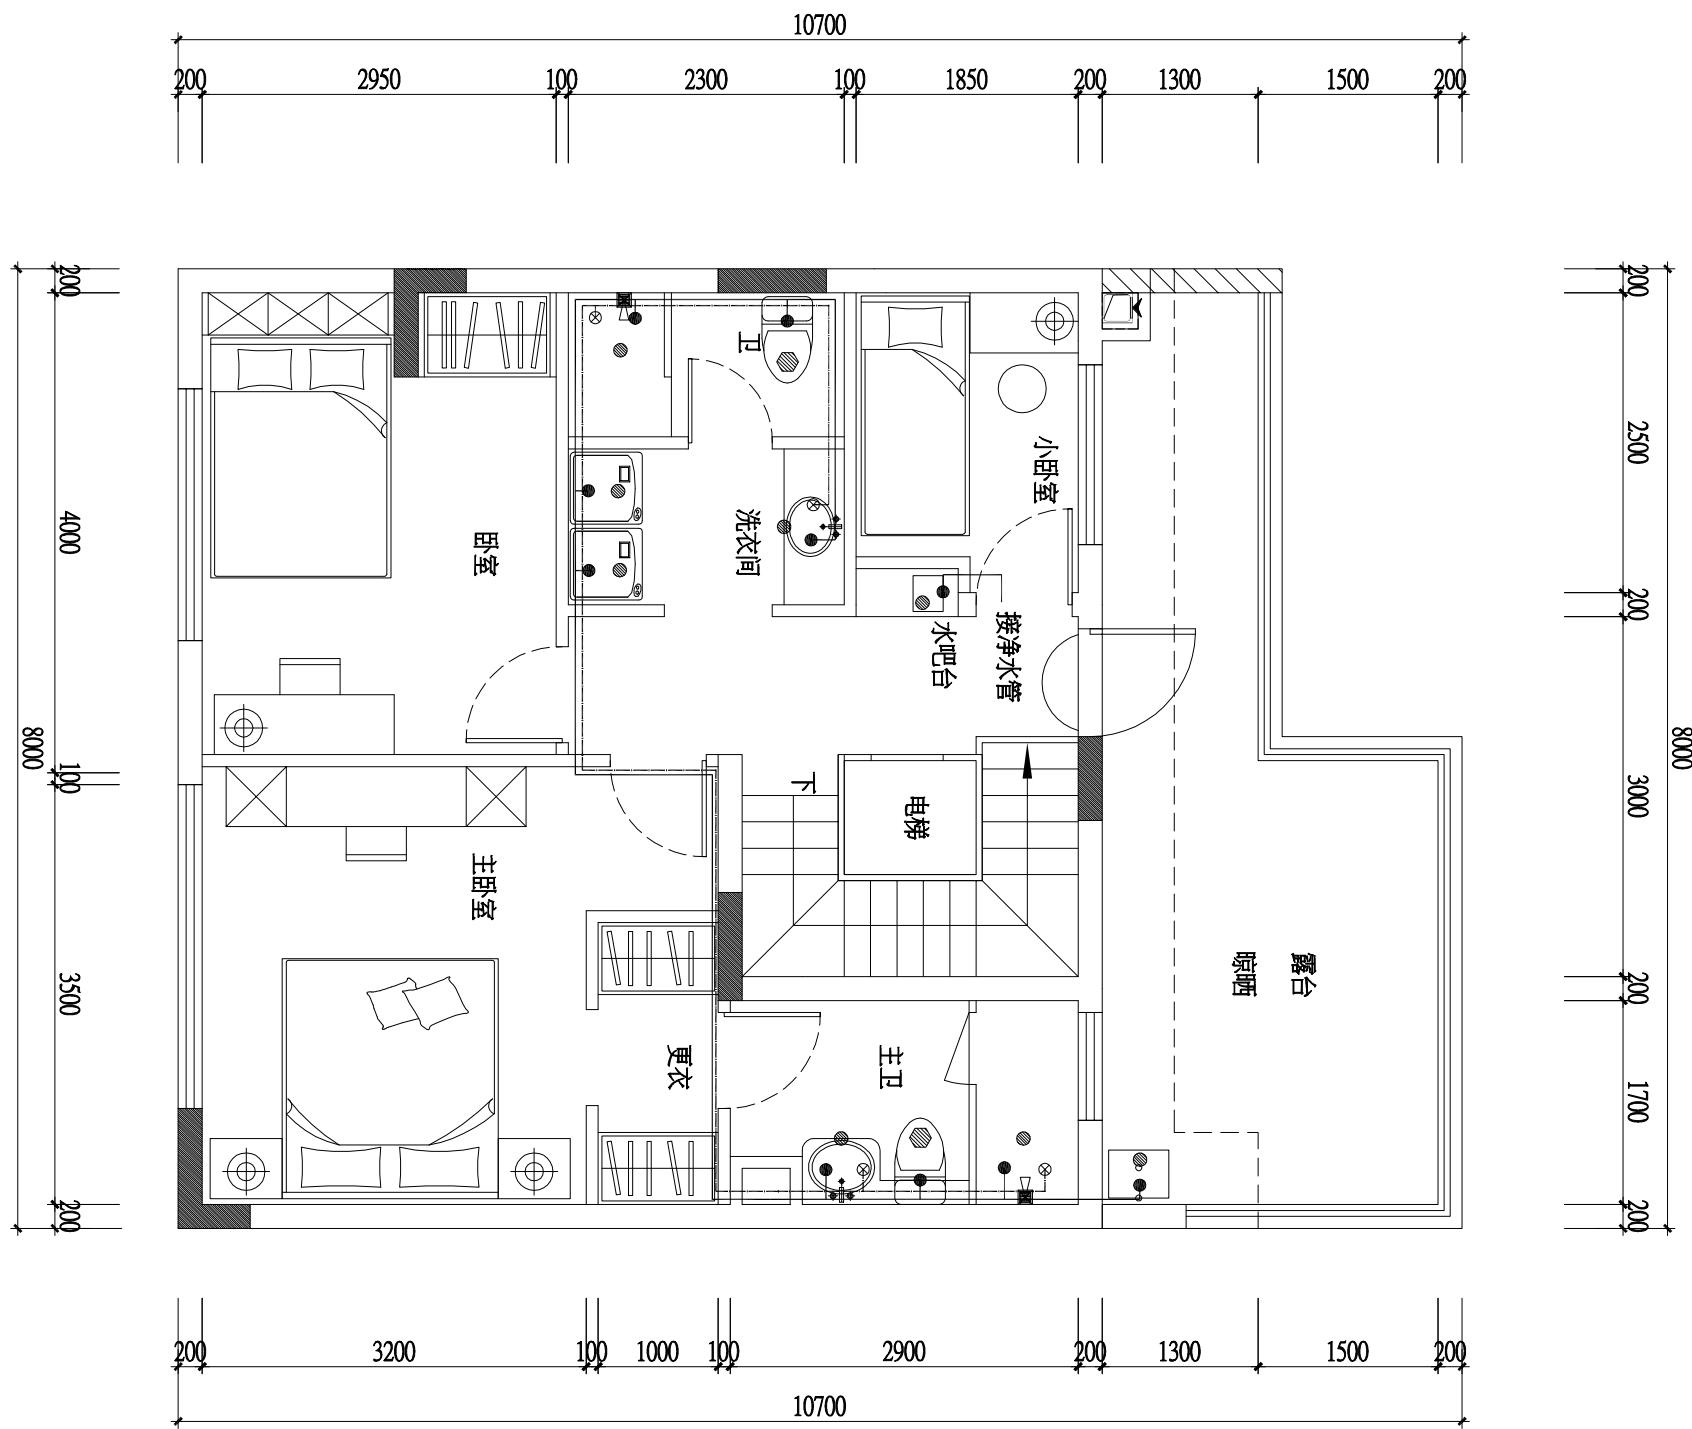

给排水说明：

图例	名称	图例	名称
●	给水口	①	墙排水
⊗	热水上水口	——	热水管
●	排水口	——	给水管
◎	马桶排水口	△	热水器