

黑色方钢


绳网

裸黑色钢架
黑色金属栏杆扶手

白色涂料
灰色涂料

木门套

备注
□本图未经同意，不得复制图纸及其设计
任何部分。
□有图纸尺寸标注须在实际工地复核及
量度。
□勿按比例量度图纸，应采用已标明的
尺寸。
□本图纸必须和规格说明、合同条款及其
他有关图纸，并使用《建筑制图统一标准》
的规定图线、图例及图框。图线粗细、图例
及图框尺寸均按GB/T10619—89执行。
□本图必须和规格说明、合同条款及其
他有关图纸，并使用《建筑制图统一标准》
的规定图线、图例及图框。图线粗细、图例
及图框尺寸均按GB/T10619—89执行。
□本图必须和规格说明、合同条款及其
他有关图纸，并使用《建筑制图统一标准》
的规定图线、图例及图框。图线粗细、图例
及图框尺寸均按GB/T10619—89执行。

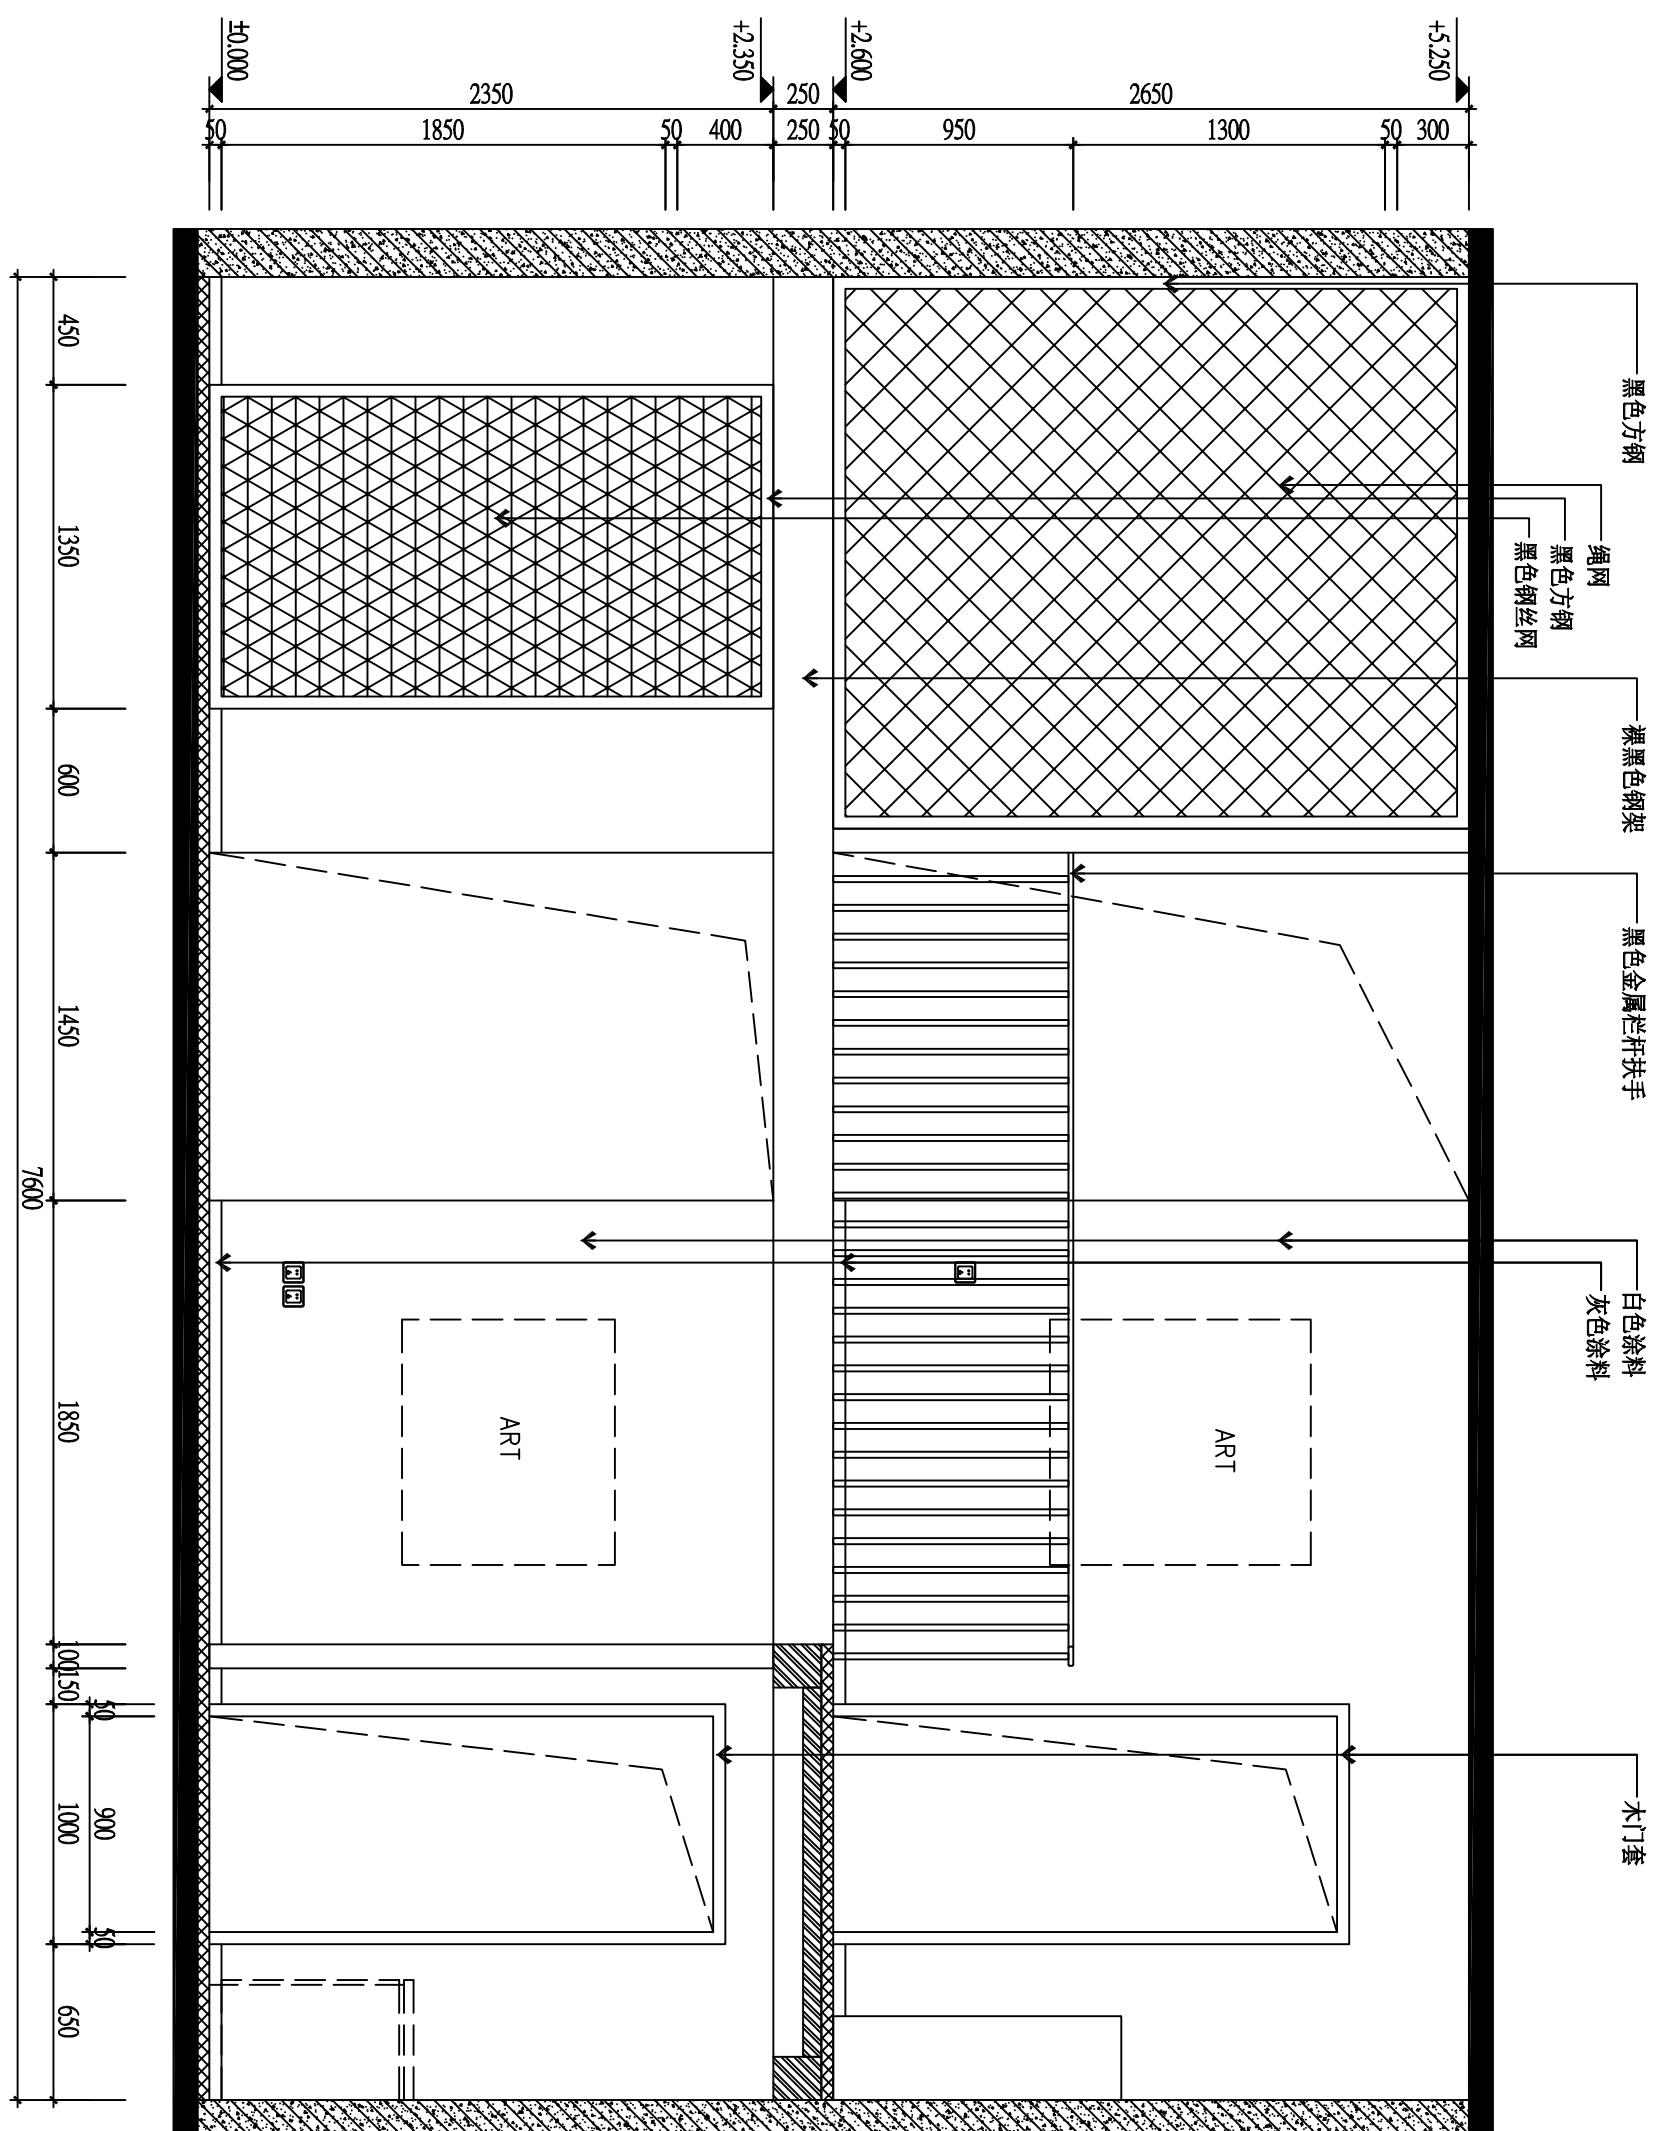

是境
設計

01-1F/BF 健身区立面图
SCALE:1:100

审 批 人	核 批 人
APPROVE BY	APPROVE BY
比 例	1: 30
SCALE	DATE
图 名 称	DRAWING TITLE

-1F/BF 立面布置图
图号
SHEET NO
-1F/BF.E-01

备注

- 在未经同意前，不得复制图纸及其设计任何部份。
- 所有图纸尺寸标注须在实际工地上复核及量度。
- 请勿接比例量度图纸，应采用已标明的尺寸。
- 本图必须和规格说明、合同条款及其有关图纸一并使用，如发现图纸内容有不符之处，必须通知设计单位。

1

项目名称
PROJECT

龙湖椿山

总负责
PRINCIPAL

设计

DESIGNER

22
DRAWN BY


校对

审核
APPROVE

A
APPROVE

SCALE
1:

日期
20
DATE

图名

DRAWING ILLUS.

-1F/BF立面布置图

卷之三

SHEET NO

-LL/BL.L-02

This architectural floor plan diagram illustrates a building section with the following key features and dimensions:

- Vertical Dimensions:** The top horizontal dimension is +5.250. Below it is +2.600, followed by +2.350, 2650, 1650, 950, 50, 2050, 2350, 50, 2000, 250, 50, 250, 50, 2050, 2350, 50, and ±0.000.
- Horizontal Dimensions:** The left vertical axis shows 800, 1200, 40, 700, 40, 800, 40, 200, 7300, 60, 850, 20, 740, 20, 800, and 2000.
- Rooms and Components:** The diagram shows multiple rooms labeled ART, which likely represent study or office areas. It also includes a staircase, a central entrance area, and various doors and windows.
- Material Specifications:** A legend on the right side provides material details:
 - 整体电梯 (由专业厂家定制)
 - 清水混凝土面
 - 白色涂料
 - 木门套
 - 灰色涂料
 - 石材台面
 - 木饰面
 - 白色涂料
 - 成品书架
 - 白色涂料
 - 镜面
- Annotations:** Arrows point from labels like "调色" (color adjustment) and "白色涂料" (white paint) to specific parts of the plan.

是境

白色涂料

白色涂料

黑色方钢

裸黑色钢丝网

黑色金属栏杆扶手

备注
NOTE

□本图未经同意，不得复制图纸及其设计任何部分。
□本图纸尺寸标注须在实际工地复核及量度。
□勿按比例量度图纸，应采用已标明的尺寸。
□本图纸必须和规格说明、合同条款及其有关图纸，并使用，如发现图纸内容有不符之处，必须立刻通知设计者。

业主
CLIENT

项目名称
PROJECT

龙湖椿山

总负责
PRINCIPAL

设计师
DESIGNER

绘图
DRAWN BY

校对
COLLATE

审核
APPROVE

比例
SCALE

例 1: 30

日期
DATE


2020.07

图名
DRAWING TITLE

-1F/BF立面布置图


图号
SHEET NO

-1F/BF.E-03

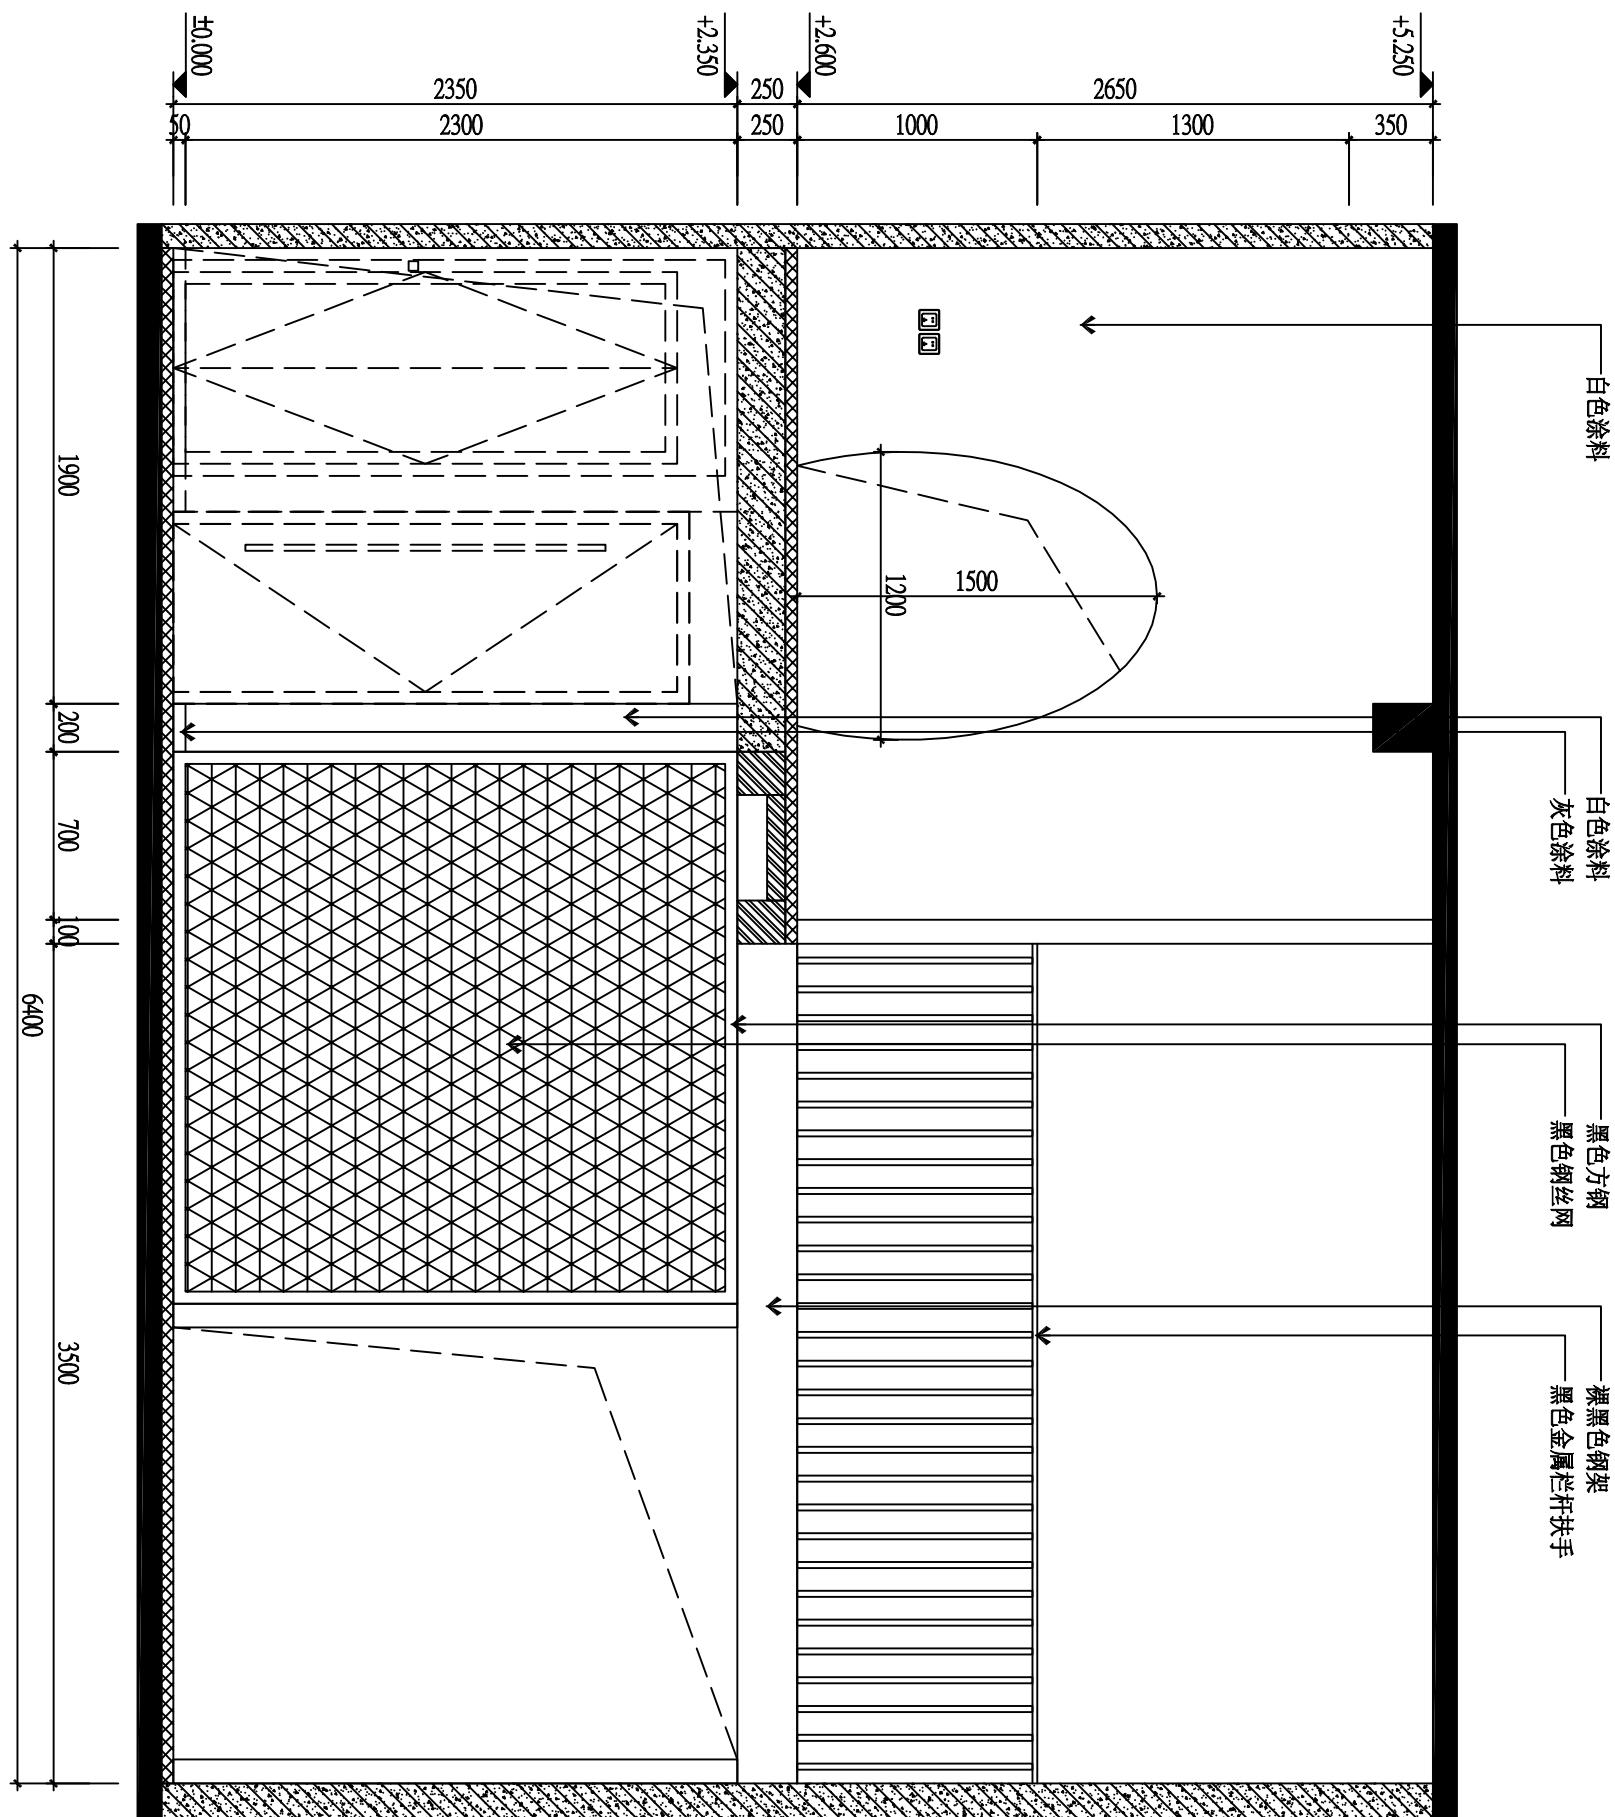

03-1F/BF 健身区立面图
SCALE:1:30

是境
设计

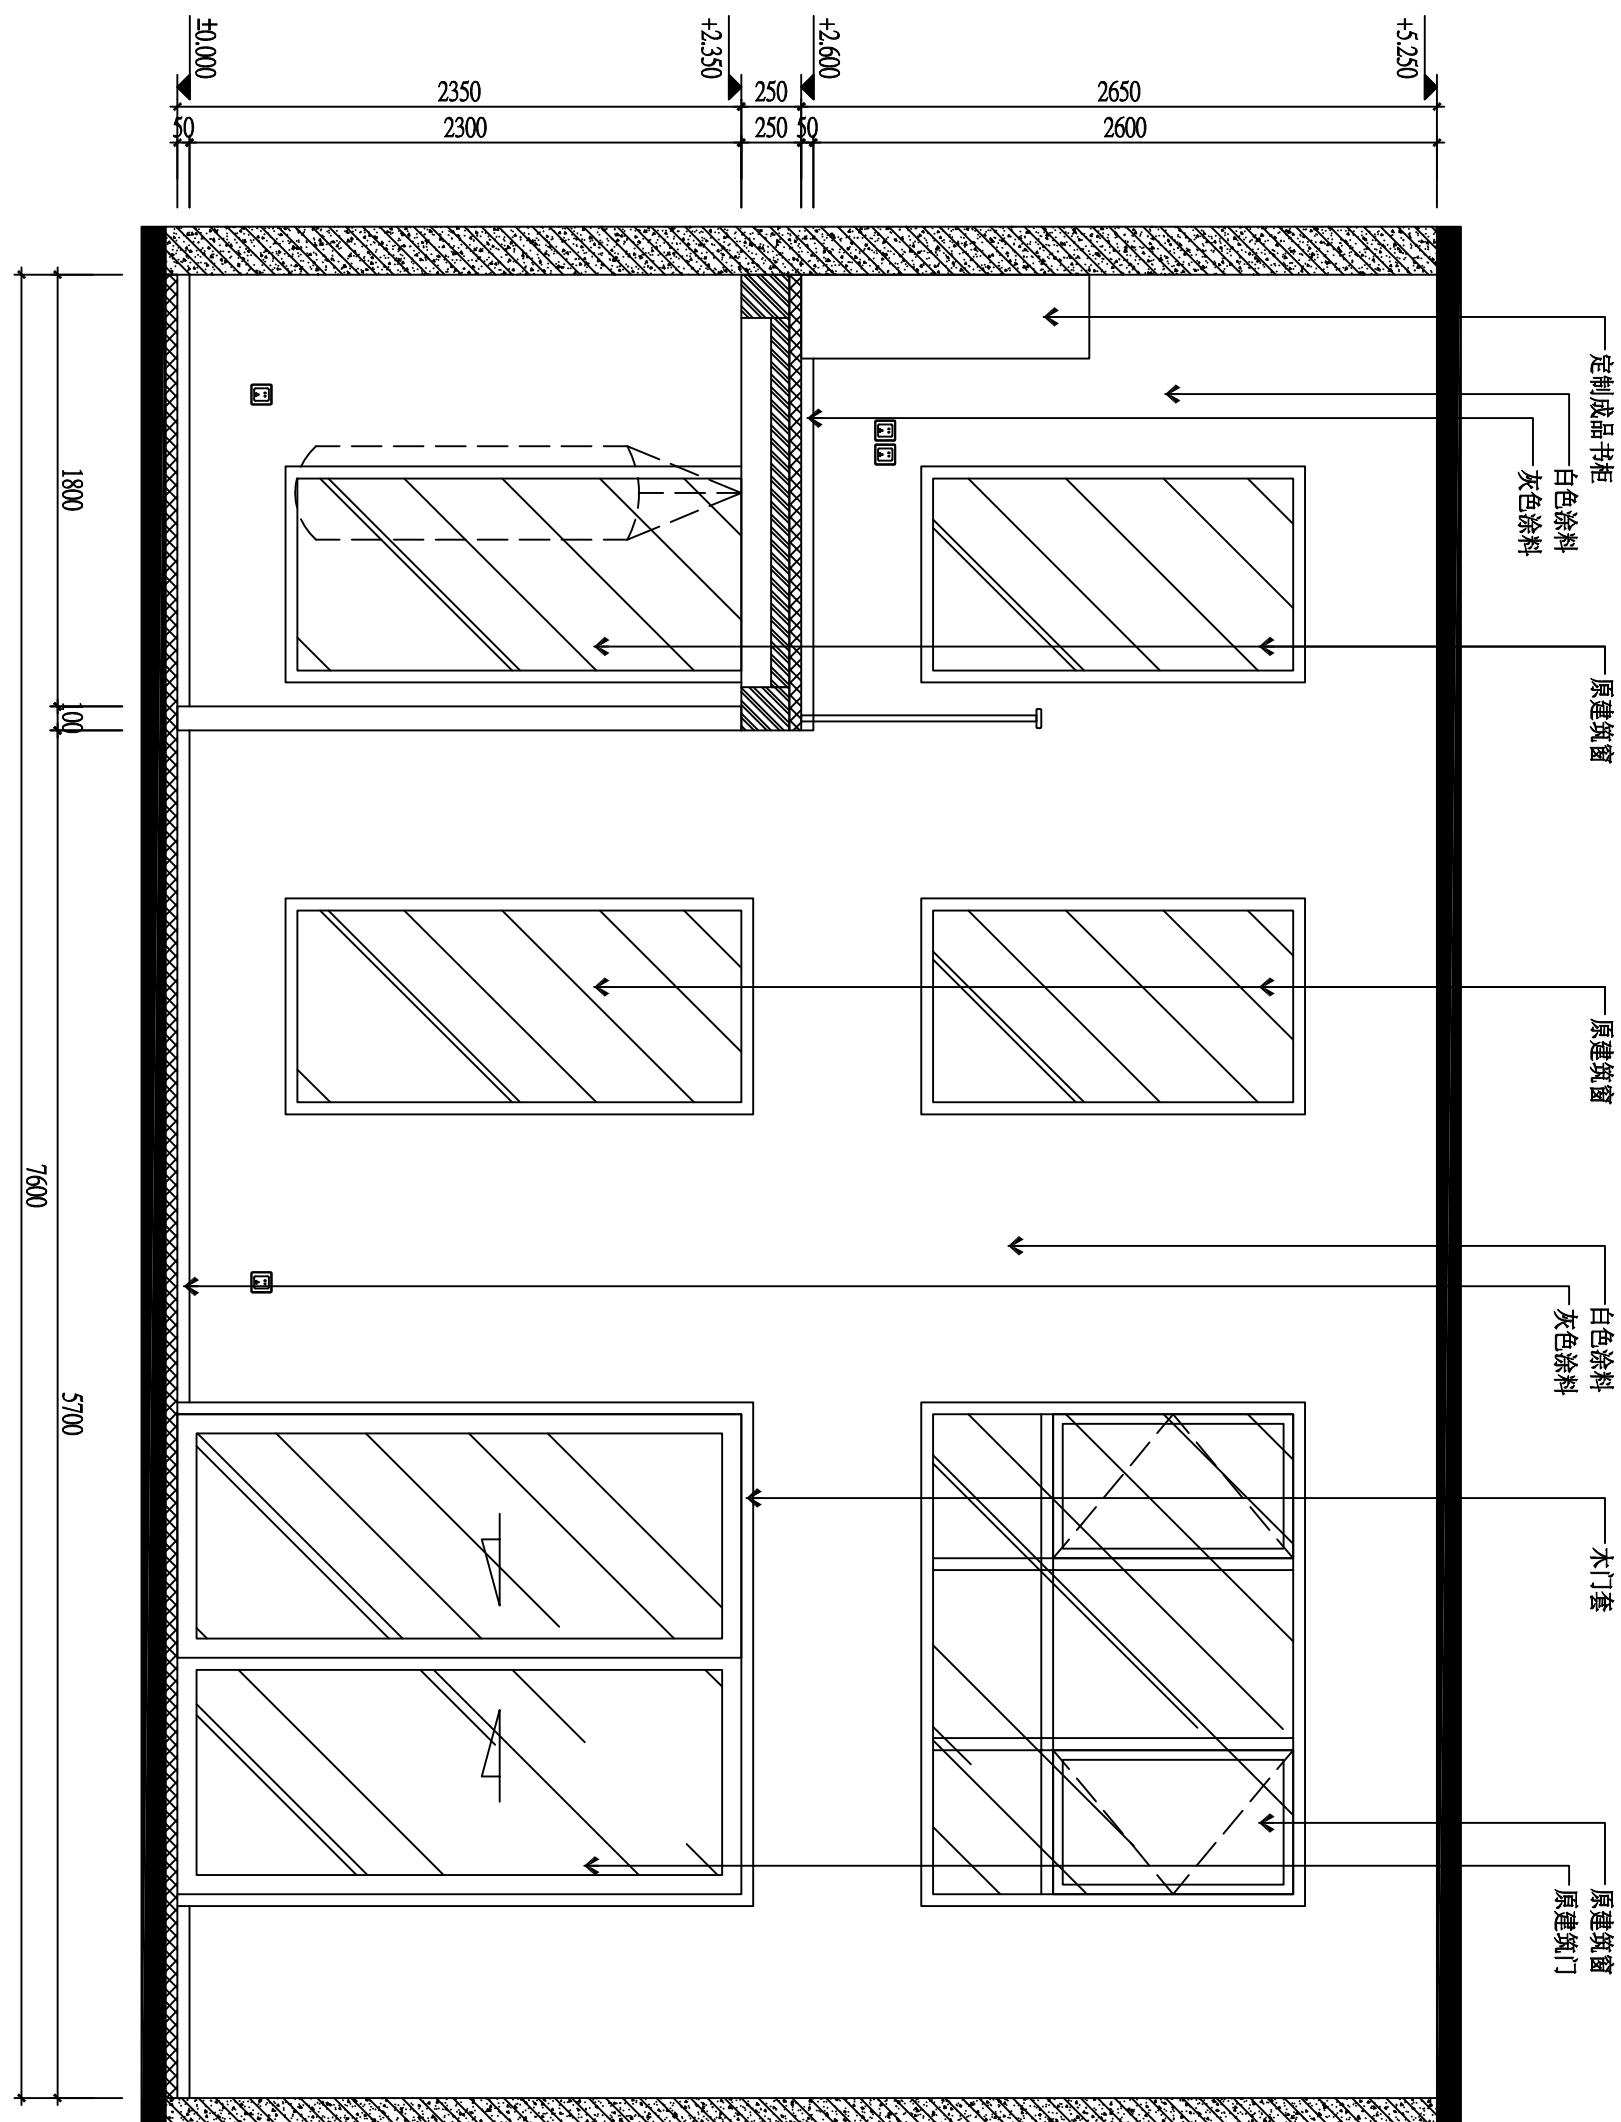

备 案

- 在未经同意前，不得复制图纸及其设计任何部份。
- 所有图纸尺寸标注须在实际工地上复核及量度。
- 请按比例量度图纸，应采用已制好的尺寸。
- 本图集必须和规格说明、合同条款及其他有关图一并使用，如发现图面内容有不妥之处，必须立即通知设计师。

业 主 CLIENT	项目名称 PROJECT
总 负 责 PRINCIPAL	龙湖春山
设 计 DESIGNER	
绘 图 DRAWN BY	
校 对 COLLATE	

-1F/BF立面布置图

圖號
SHEET NO

-1F/BF.E-04

是境

白色涂料
灰色涂料
定制壁挂篮球框

定制玄关鞋柜
调色涂料
灰色涂料
白色涂料

备注
NOTE
□本图未经同意，不得复制图纸及其设计
任何部分。
□所有图纸尺寸标注须在实际工地复核及
量度。
□勿按比例量度图纸，应用已标明的
尺寸。
□本图纸必须和现场说明、合同条款及其
他有关图纸，并使用，如发现图纸内容
有不符之处，必须立刻通知设计者。

+5.250

2650
2600

+2.600
250
150
250
50

2350
2150

+2.350
50

3500

6400

800

200

400

1100

400

10.000

150



550

530

965

1165

ART

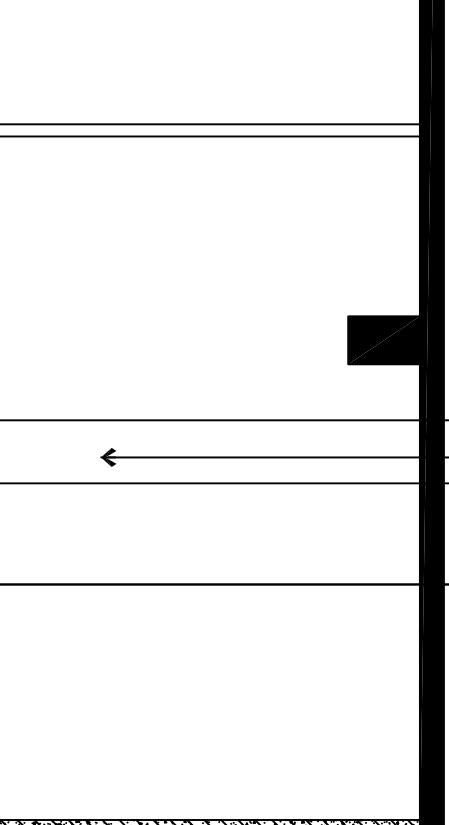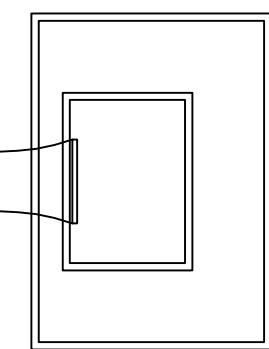

-1F/BF立面布置图
-1F/BF.E-05

图名	DRAWING TITLE
图号	SHEET NO
日期	DATE
比例	SCALE
审核	APPROVE
设计	DESIGNER
绘图	DRAWN BY
校对	COLLATE
审核	APPROVE
设计	DESIGNER
绘图	DRAWN BY
校对	COLLATE

05-1F/BF健身区立面图
E-05
SCALE:1:30

是境
设计

白色涂料
灰色涂料
定制壁挂篮球框

白色涂料
灰色涂料

备注
NOTE
□本图未经同意，不得复制图纸及其设计
任何部分。
□有图尺寸标注须在实际工地复核及
量度。
□勿按比例量度图纸，应采用已标明的
尺寸。
□本图纸必须和现场说明、合同条款及其
他有关图纸，并使用，如发现图纸内容
有不符之处，必须立刻通知设计者。

业主
CLIENT

项目名称
PROJECT
龙湖椿山

总负责人
PRINCIPAL

设计师
DESIGNER

绘图
DRAWN BY

校对
COLLATE


审核
APPROVE

比例
SCALE
1: 30

日期
DATE
2020.07


图名
DRAWING TITLE
-1F/BF立面布置图

图号
SHEET NO
-1F/BF.E-06

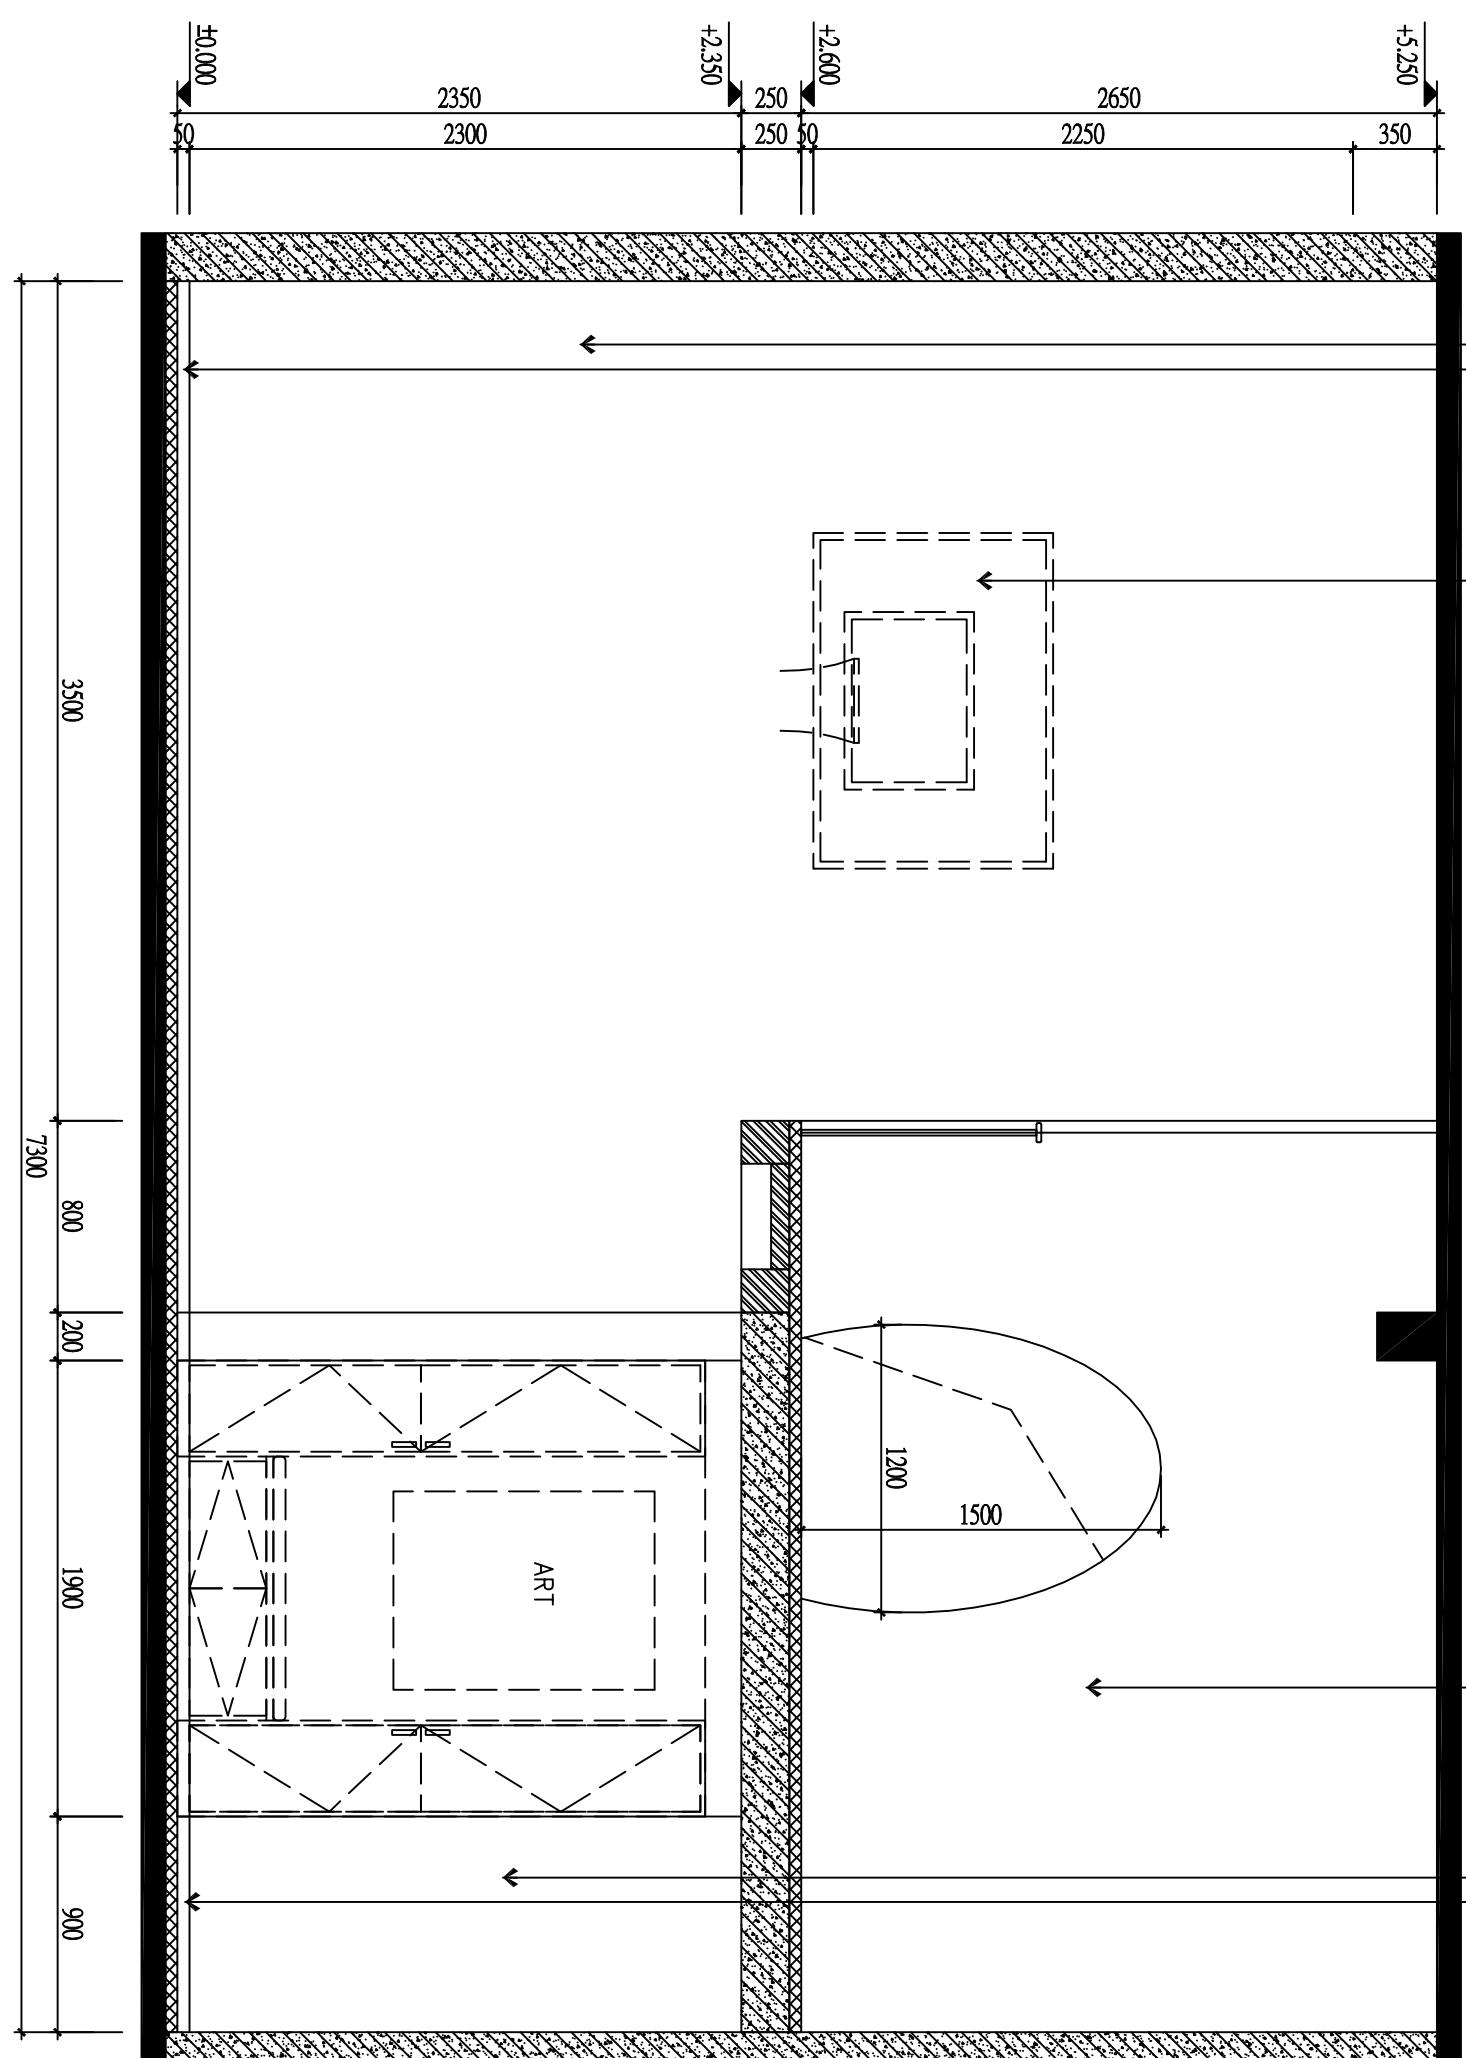

备注
NOTE

□本图样未经同意，不得复制或用其设计任何部分。
□本图样尺寸标注须在实际工地上复核及量度。
□勿按比例量度图纸，应采用已标明的尺寸。
□本图样必须和规格说明、合同条款及其他有关图样，并使用，如发现图纸内容有不符之处，必须立刻通知设计者。

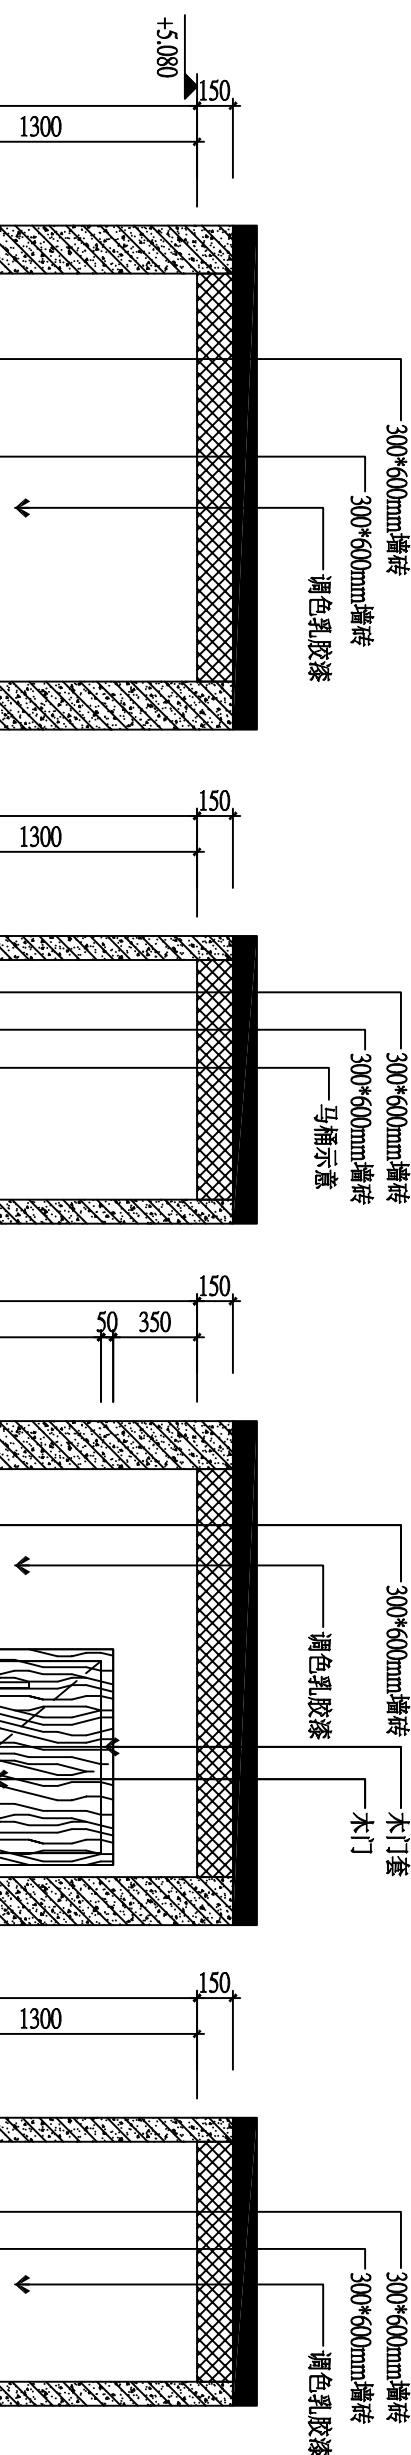


审 核	APPROVE
比 例	SCALE 1: 30
日 期	DATE 2020.07
图 名	DRAWING TITLE -1F/BF.E-07
图 号	SHEET NO

是境
设计

备 注
NOTE

- 本图未经同意，不得复制图纸及其设计任何部分。
- 所有图纸尺寸标注须在实际工地复核及量度。
- 请勿按比例量度图纸，应采用已标明的尺寸。
- 本图纸必须和规格说明、合同条款及其他有关图纸，并使用《建筑制图统一标准》有不符之处，必须立刻通知设计者。

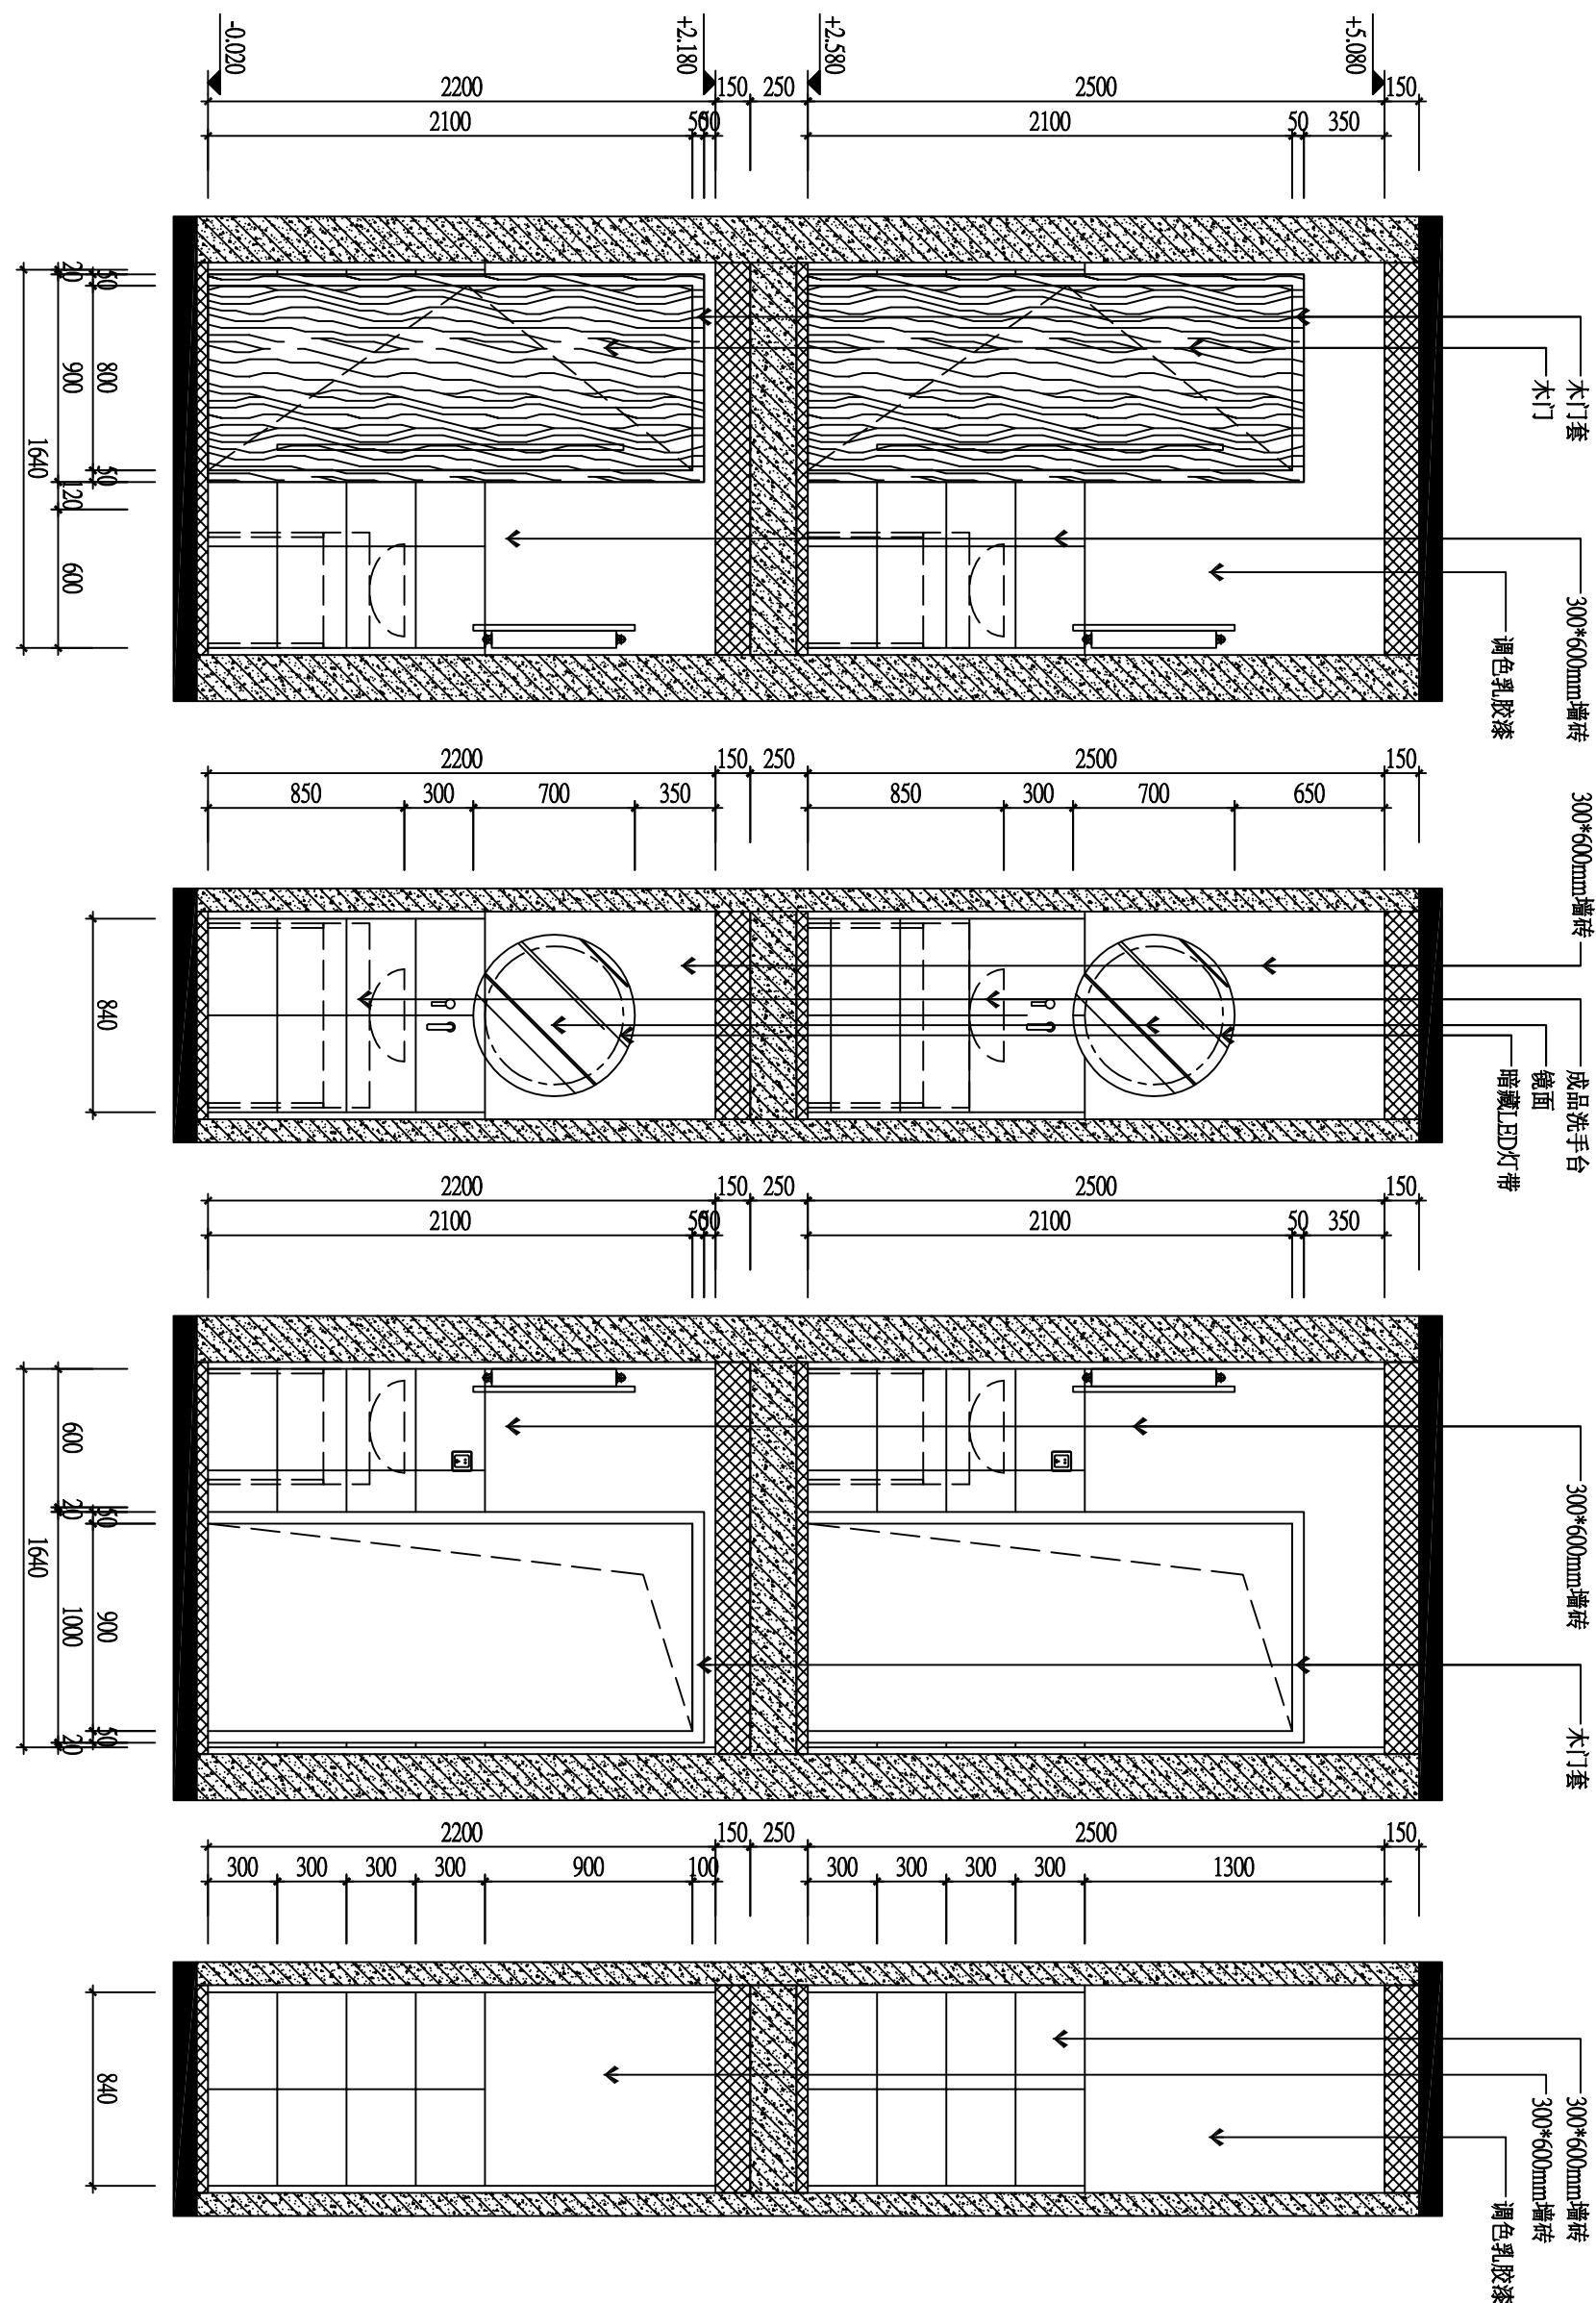

11-1F/BF卫生间立面图
SCALE:1:30
JFP-06

12-2F/BF卫生间立面图
SCALE:1:30
JFP-06

13-3F/BF卫生间立面图
SCALE:1:30
JFP-06

14-4F/BF卫生间立面图
SCALE:1:30
JFP-06

是境
設計


-1F/BF立面布置图

图 号
SHEET NO


-1F/BF.E-08

備注
NOTE


- 本图未经同意，不得复制图纸及其设计任何部分。
- 所有图纸尺寸标注须在实际工地复核及量度。
- 请勿按比例量度图纸，应采用已标明的尺寸。
- 本图纸必须和规格说明、合同条款及其他有关图纸，并使用《建筑制图统一标准》有不符之处，必须立刻通知设计者。

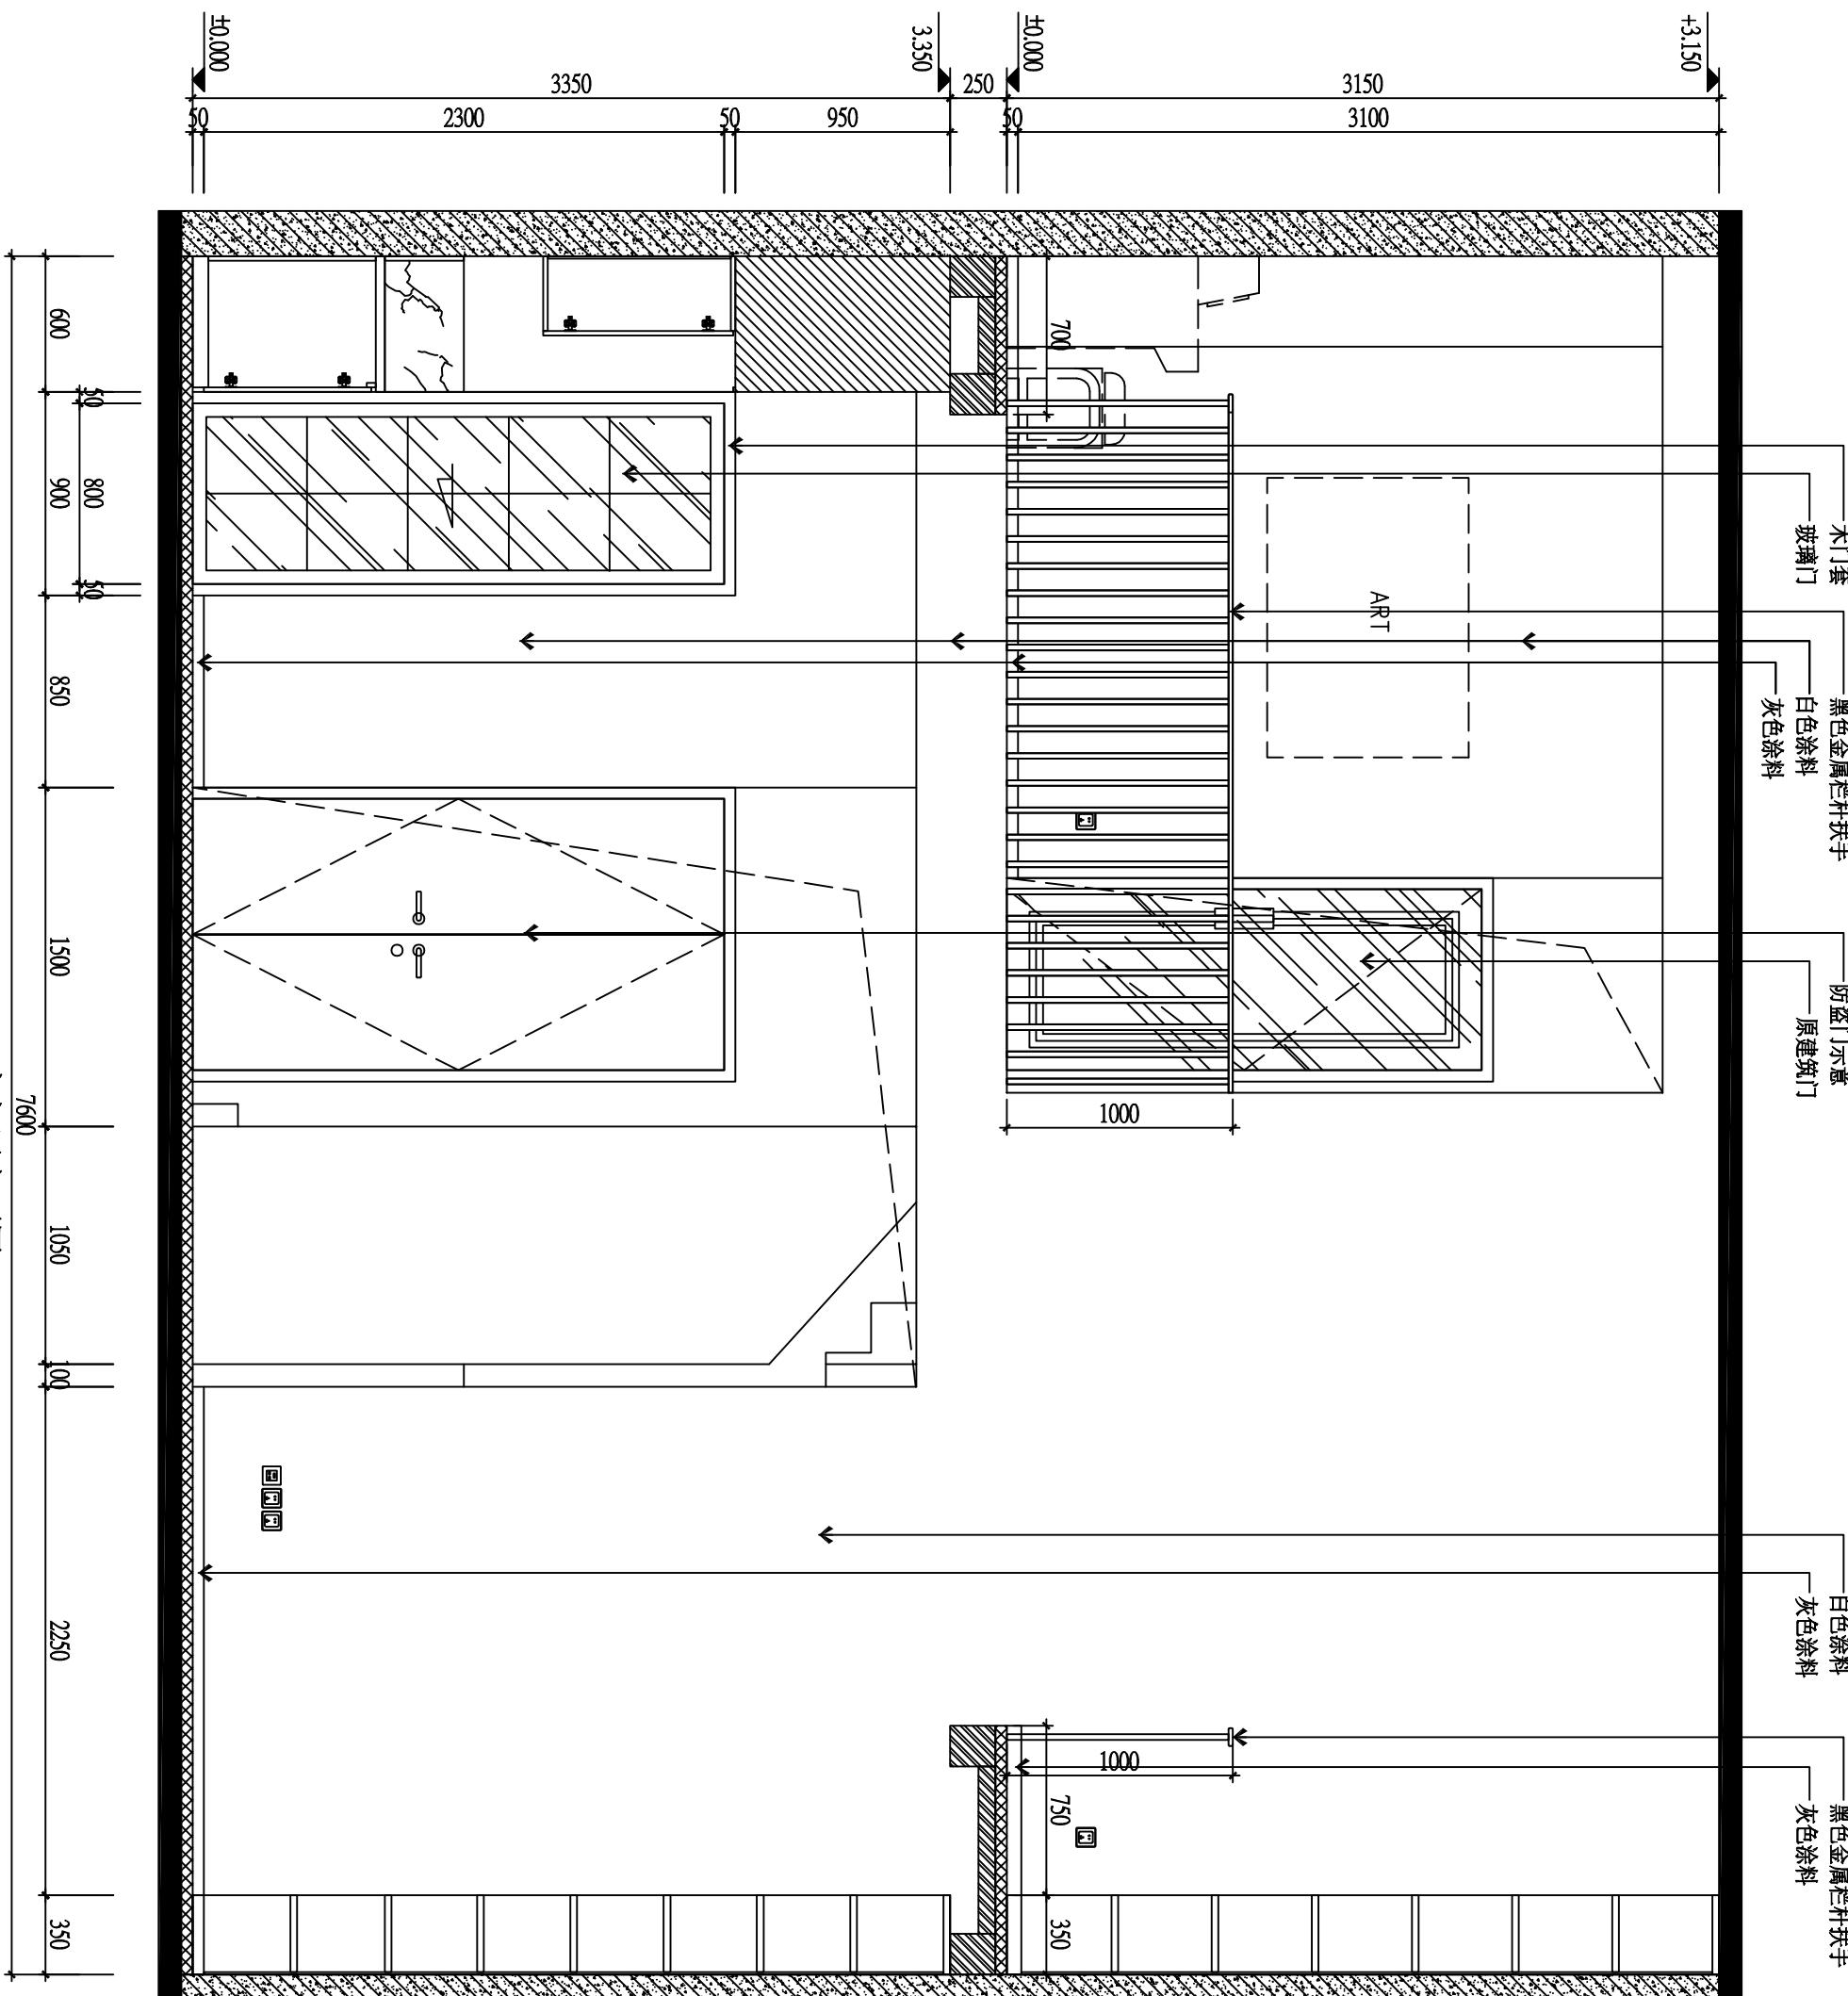

是
境
設
計

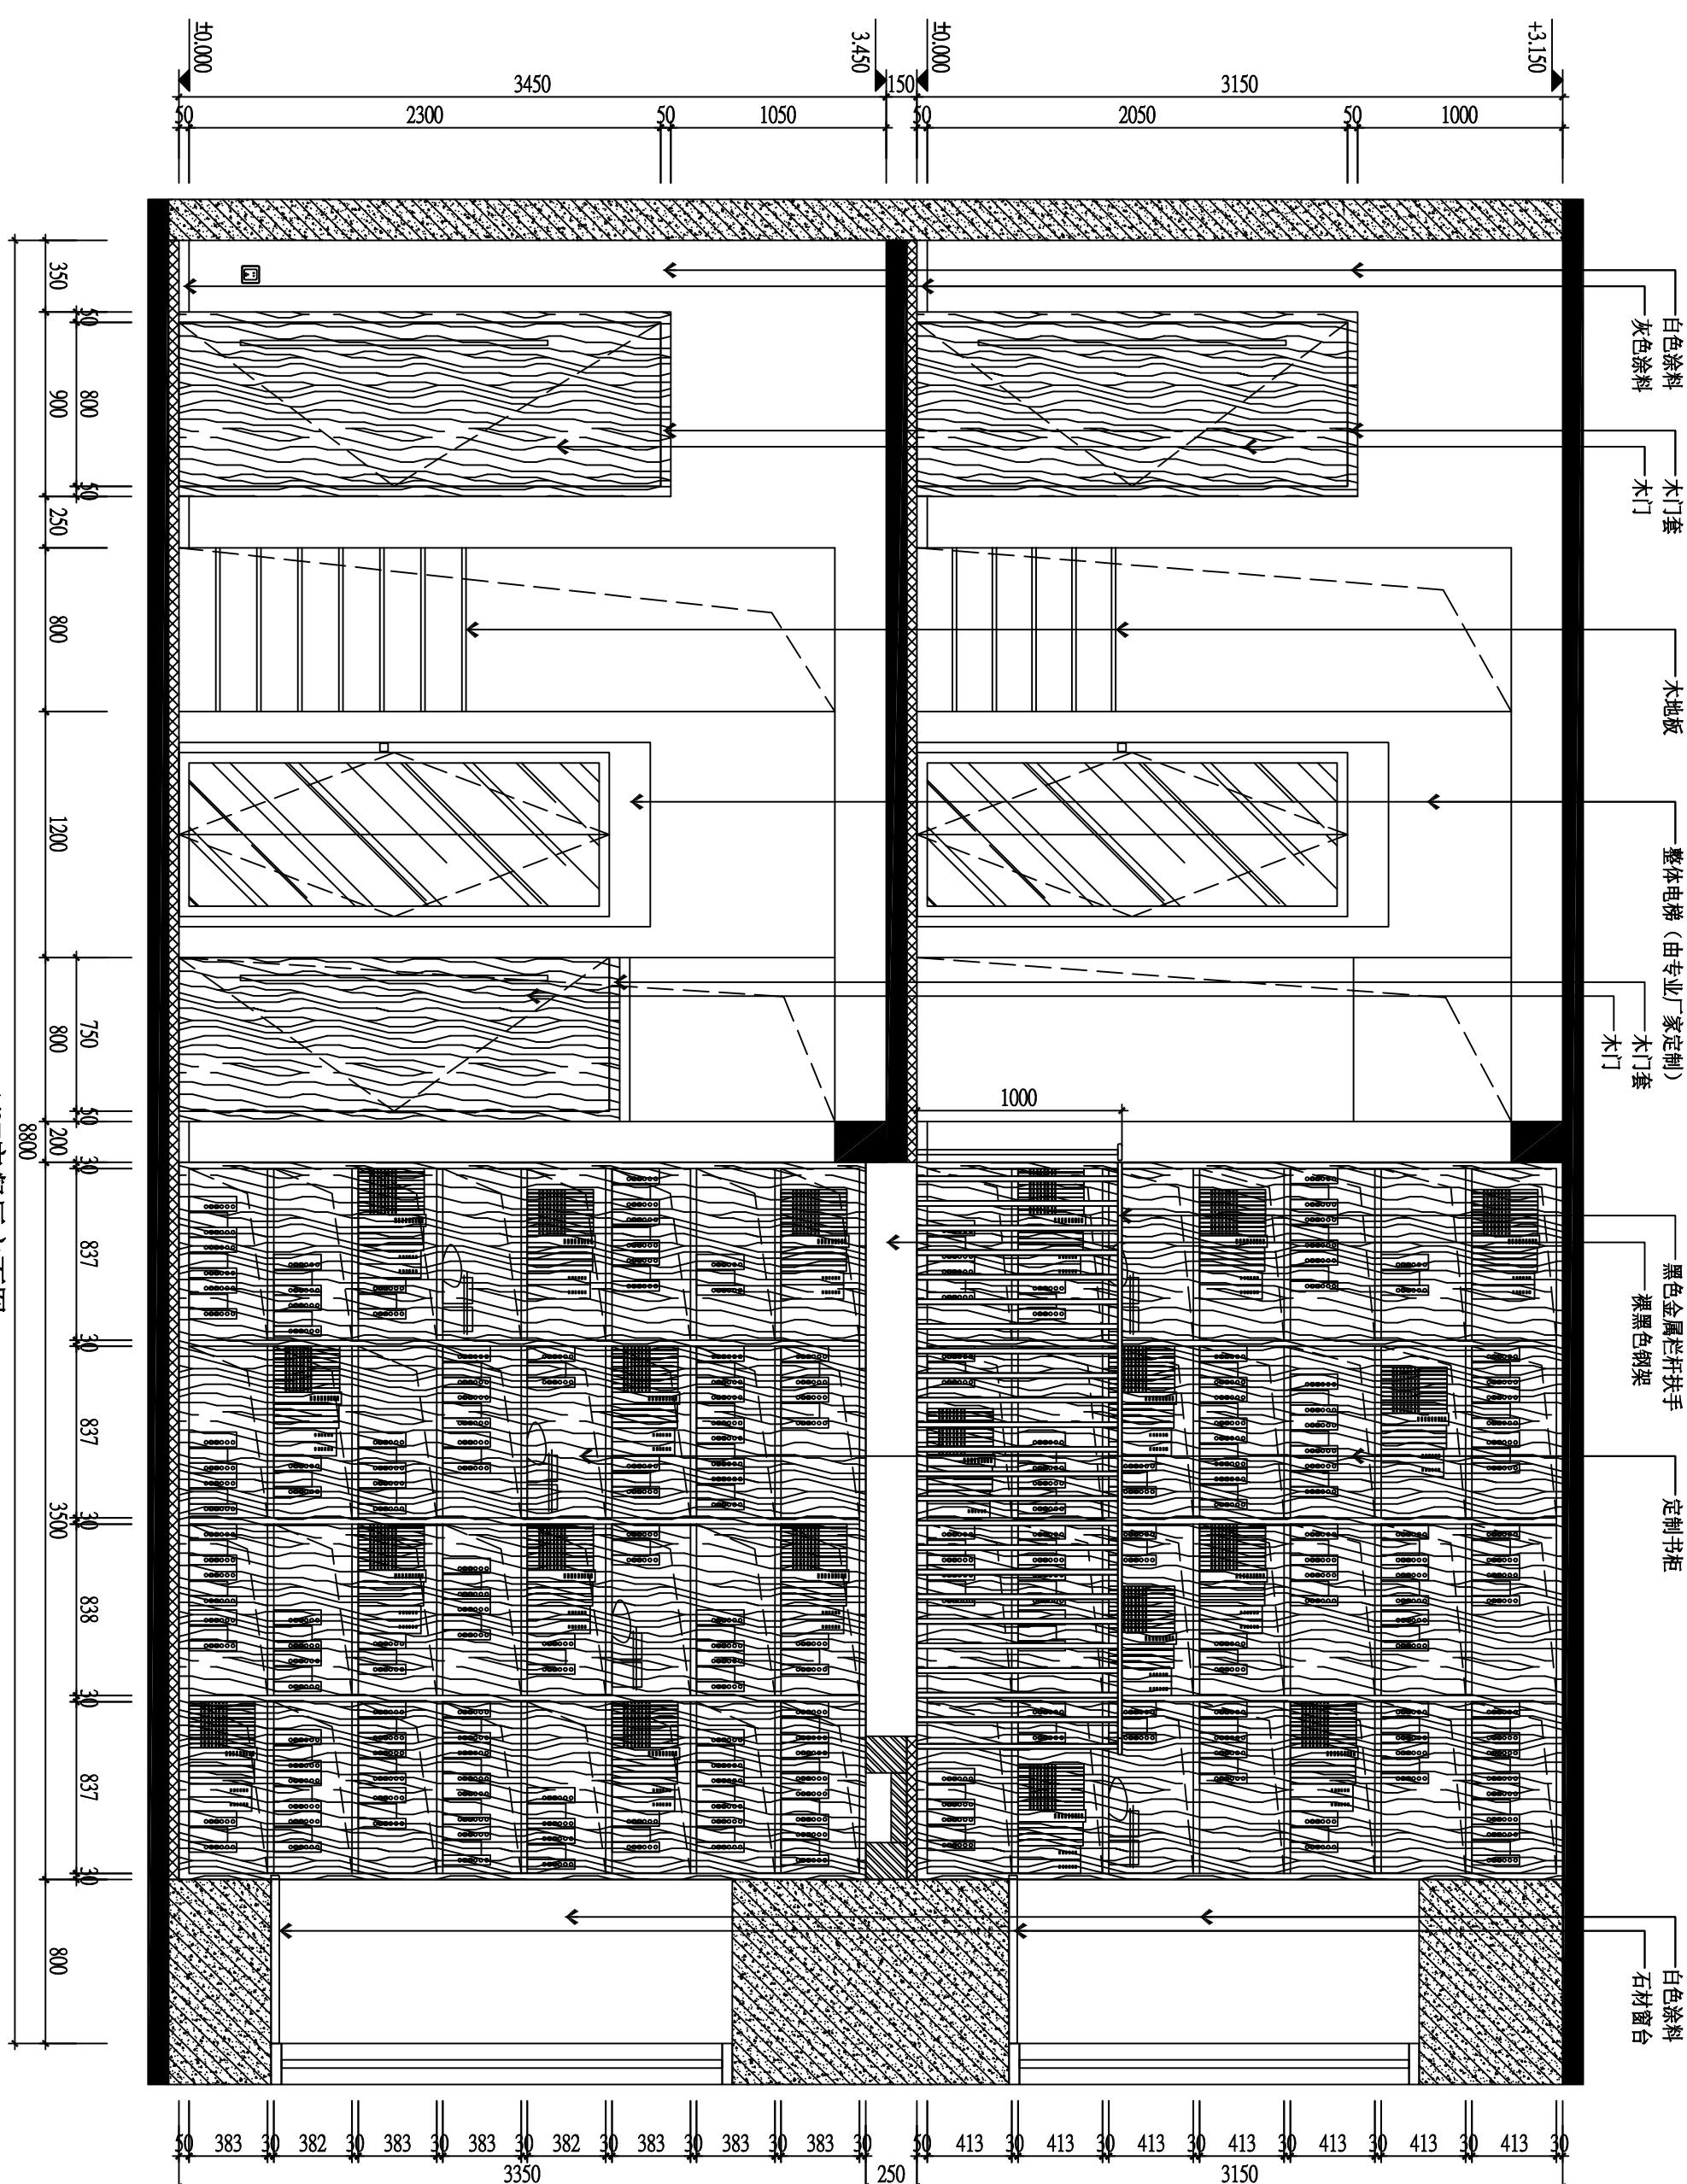


是
計
境

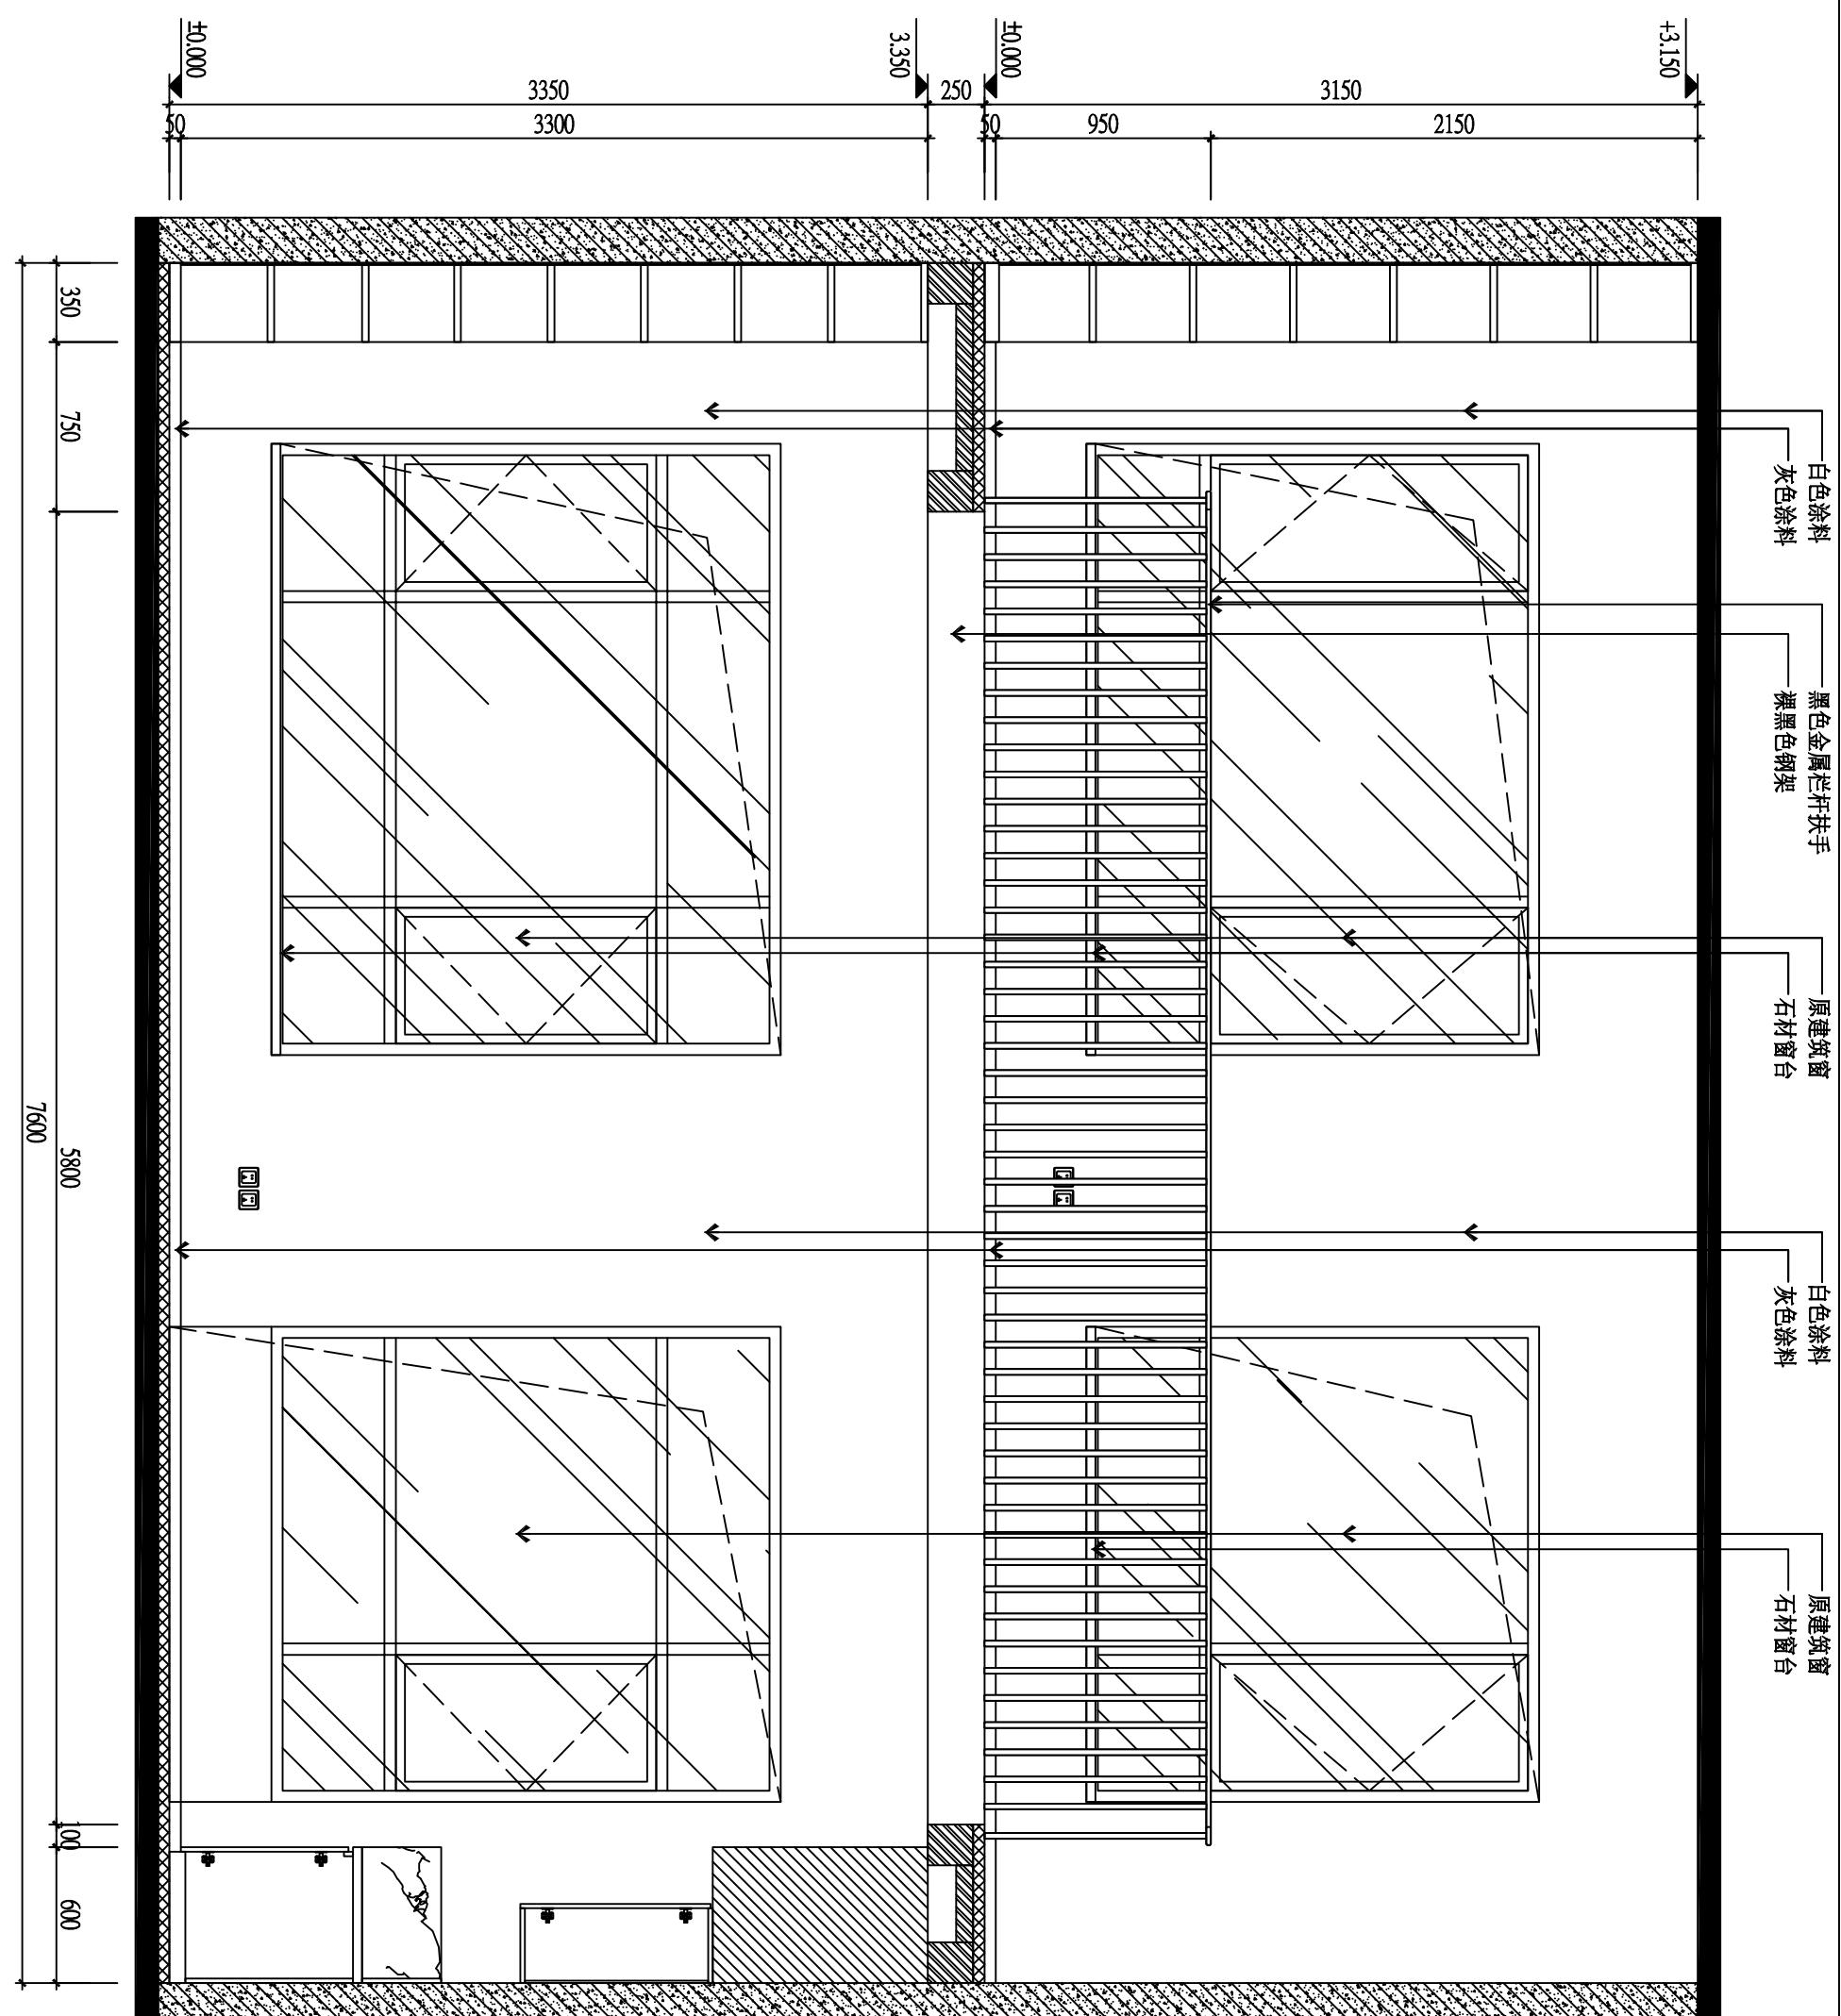

03 1/F 餐厅立面图
EPC-06 SCALE:1:30

是境
设计

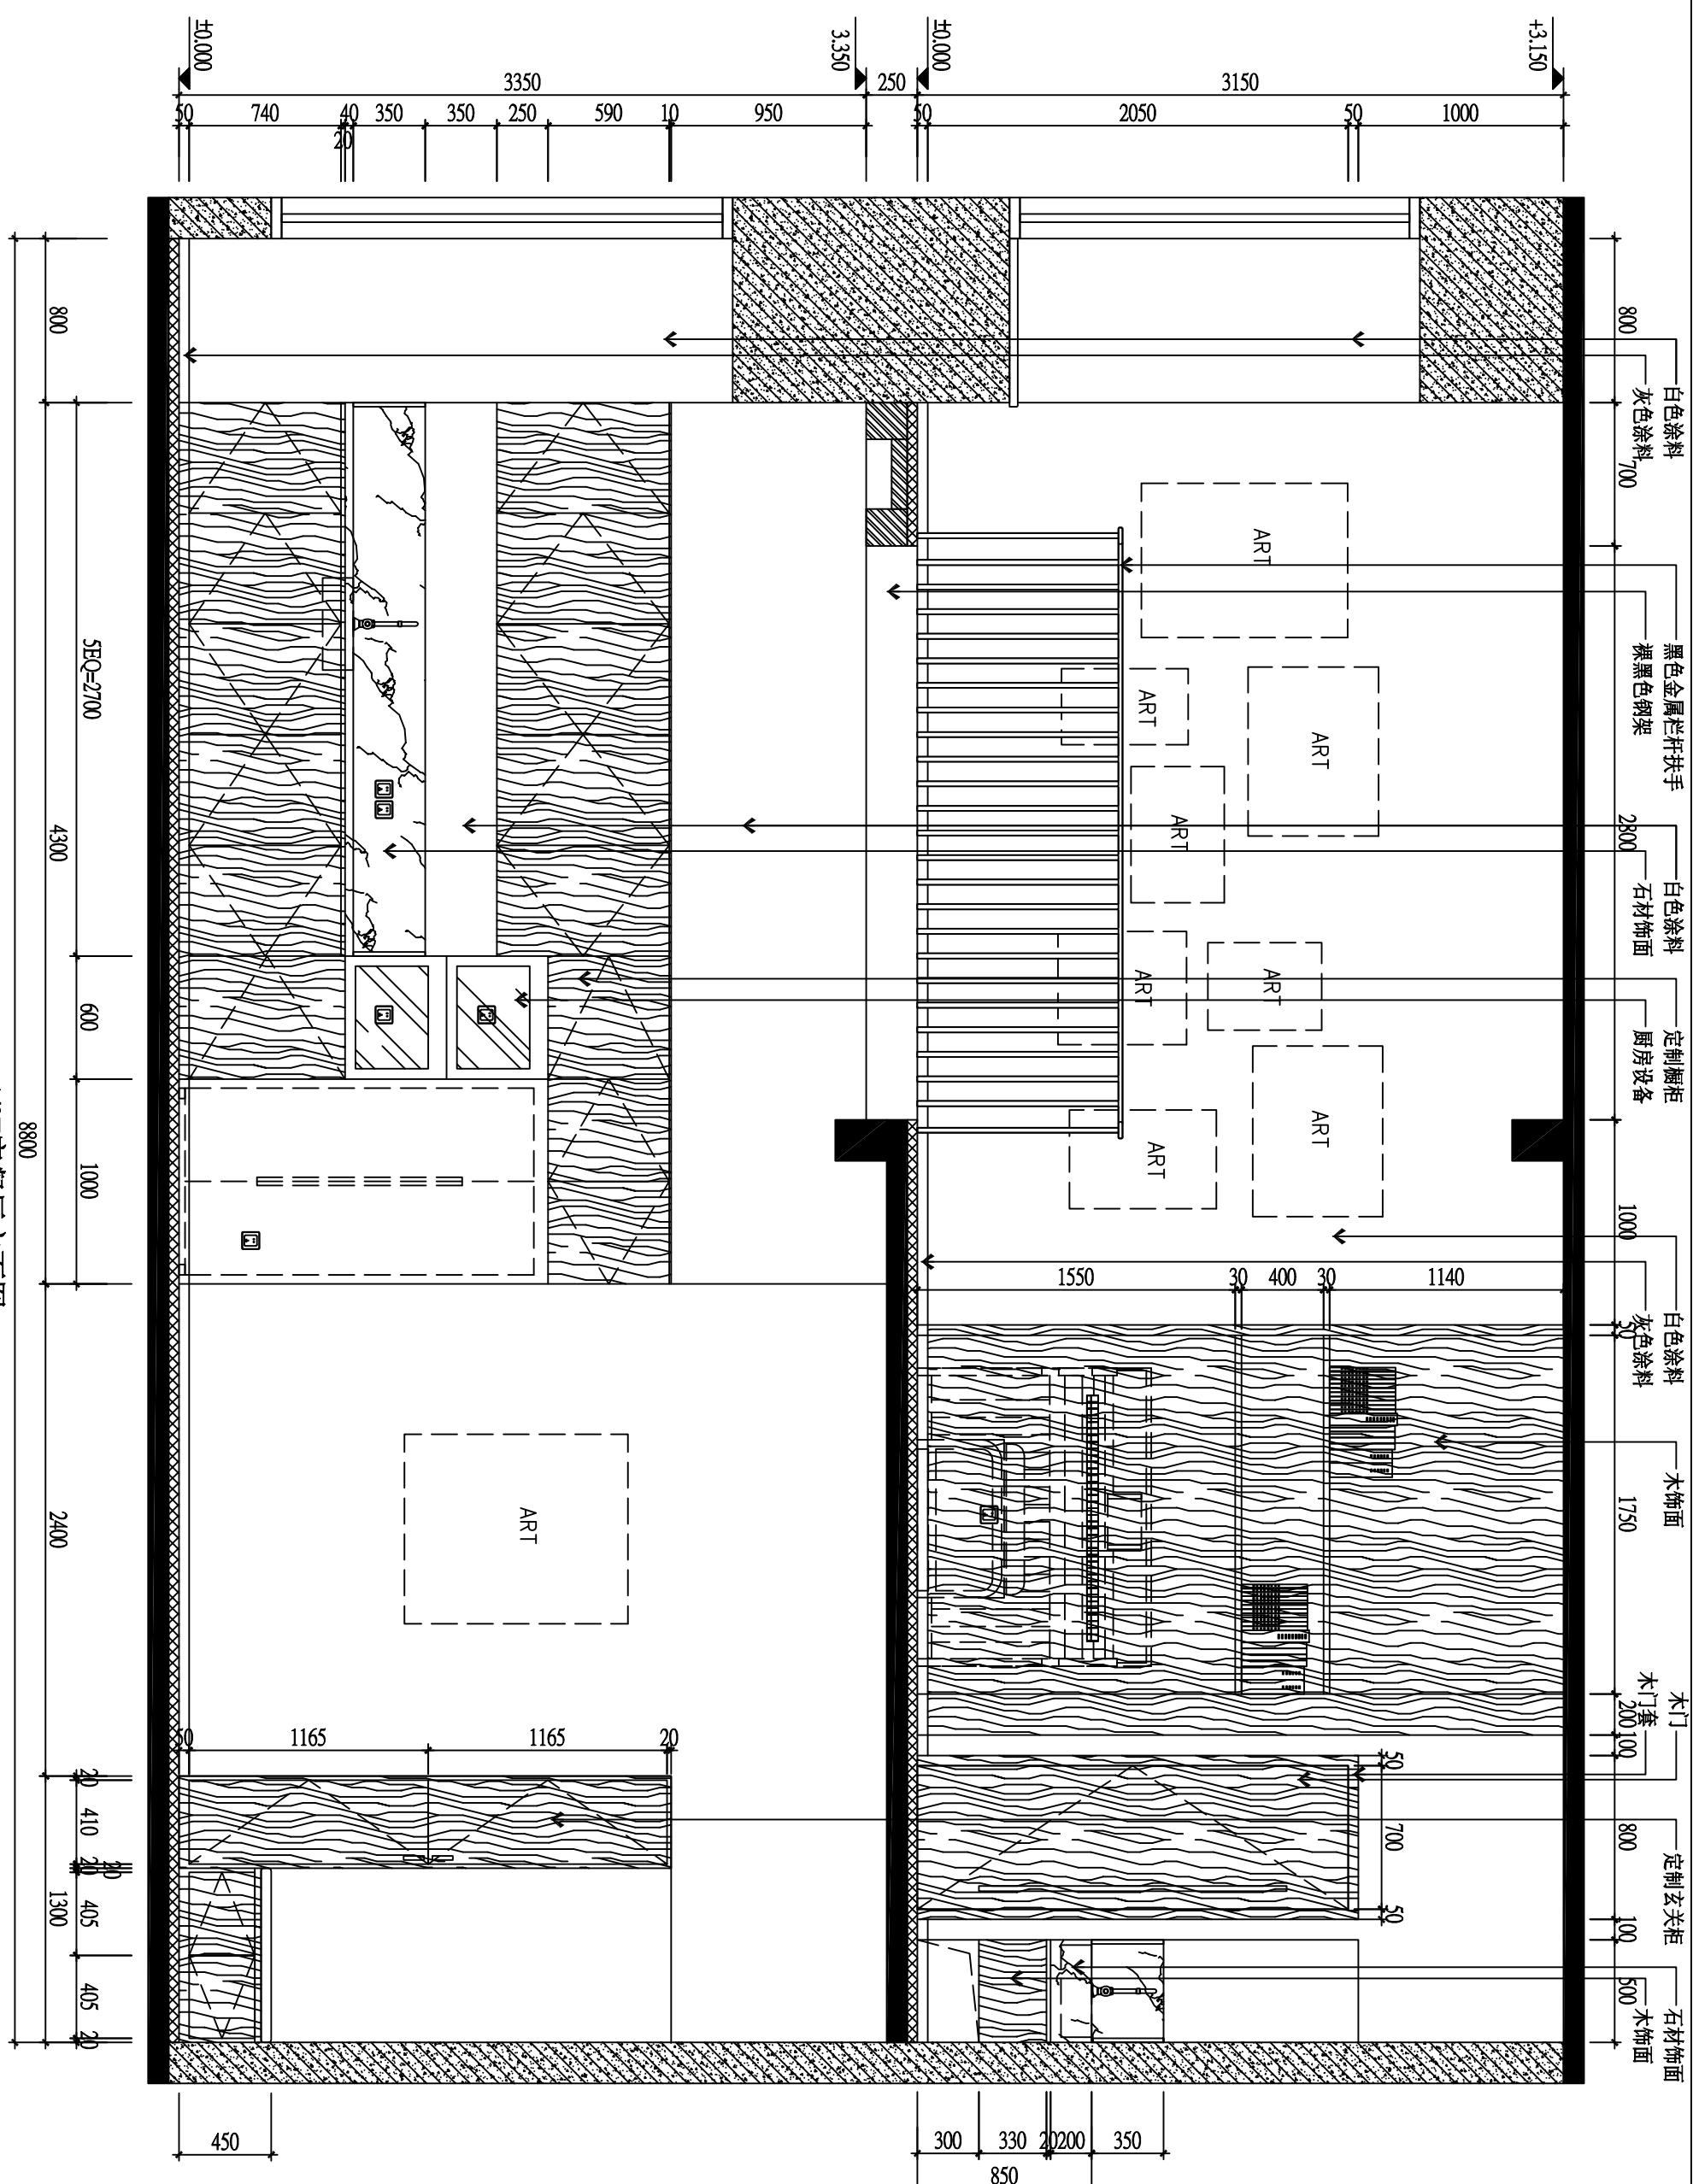

是境
設計

备 注
NOTE
□本图未经同意，不得复制图纸及其设计任一部分。
□本图尺寸标注须在实际工地复核及量度。
□请勿按比例量度图纸，应采用已标明的尺寸。

□本图纸必须和现场说明、合同条款及其他有关图纸，并使用，如发现图纸内容有不符之处，必须立刻通知设计师。

业 主
CLIENT

项 目 名 称
PROJECT
龙湖椿山

总 负 责
PRINCIPAL

设 计
DESIGNER

绘 图
DRAWN BY

校 对
COLLATE

审 核
APPROVE

比 例
SCALE 1: 30



日 期
DATE 2020.07

图 名
DRAWING TITLE

1F 立面布置图

图 号
SHEET NO

1F.E-05

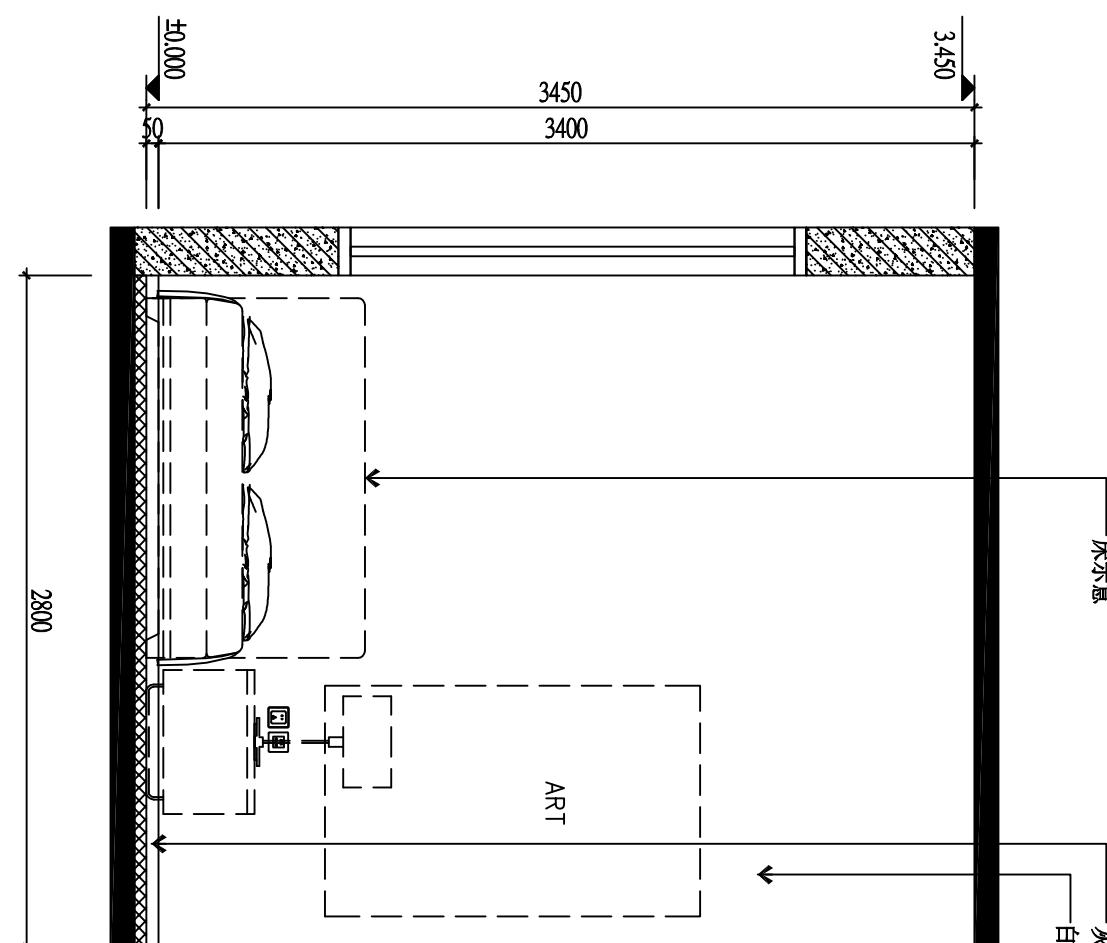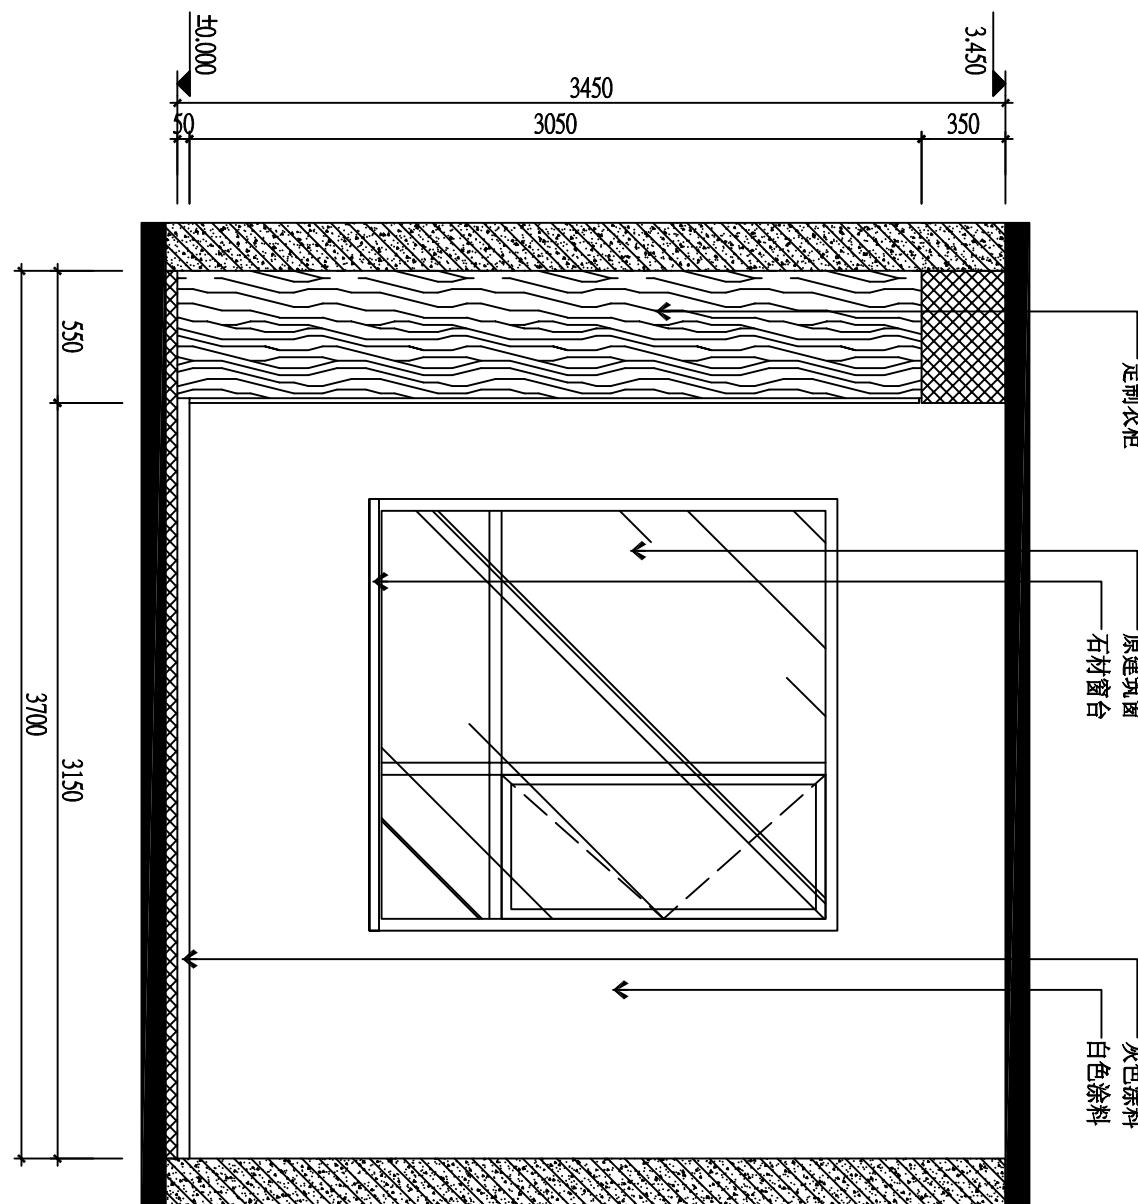

05 1F-E室立面图
IFP-05 SCALE:1/30

06 1F-E室立面图
IFP-06 SCALE:1/30

是 境
設 計

备注

□ 在未经同意前，不得复制图纸及其设计任何部份。

- 所有图纸尺寸标注须在实际工地上复核及量度。
- 请勿按比例量度图纸，应采用已标明的尺寸。
- 本图纸必须和规格说明、合同条款及其有关图纸一并使用，如发现图纸内容有不符之处，必须立刻通知设计院。

业主
CLIENT

项目名称
PROJECT
龙湖椿山

PRINCIPAL
设计
DESIGNER
绘图
DRAWN BY

校
COLLATE 对

SCALE
1: 50

1F立面布置图

1F.E-06

This figure displays two architectural floor plans of a room, each featuring a central wavy patterned area. The top plan shows the room with white-painted walls and a wooden door frame. The bottom plan shows the room with white-painted walls and a dark-colored cabinet. Both plans include dimensions for the room's width (3450), depth (2300), and various internal partitions (50, 700, 350). The height of the room is indicated as ±0.000 at the top left and 3.450 at the top right. The left side of the top plan shows vertical dimensions of 770, 50, 900, and 3700 from bottom to top. The right side of the top plan shows horizontal dimensions of 2030 and 350 from left to right. The right side of the bottom plan shows horizontal dimensions of 350 and 1500 from left to right.

This architectural floor plan illustrates two sections of a room, each featuring a central rectangular area with wavy lines representing wood grain. The top section has a total width of 3450 units, with a 50-unit gap at the left end and 350-unit gaps at the right end. The bottom section also has a total width of 3450 units, with a 50-unit gap at the left end and 350-unit gaps at the right end. Both sections include vertical dimensions on the left side: 770, 50, 900, 50, 3700, 2030, 50, 800, 50, 900, 50, 350, and 2800. The right side of the plan includes a legend with the following entries:

- 木门套 (Door frame)
- 木门 (Wood door)
- 白色涂料 (White paint)
- 灰色涂料 (Grey paint)
- 定制衣柜 (Customized wardrobe)

是境設計

备
注
NOTE

- 本图未经同意，不得复制图纸及其设计任何部分。
- 有图纸尺寸标注须在实际工地复核及量度。
- 请勿按比例量度图纸，应采用已标明的尺寸。
- 本图纸必须和规格说明、合同条款及其他有关图纸，并使用，如发现图纸内容有不符之处，必须立刻通知设计师。

业
主
CLIENT

项
目
名
称
PROJECT
龙湖椿山

总
负
责
人
PRINCIPAL

设
计
师
DESIGNER

绘
图
DRAWN BY

校
对
COLLATE

审
核
APPROVE

比
例
SCALE


日
期
DATE

图
名
DRAWING TITLE

1F立面布置图

图
号
SHEET NO

1F.E-07

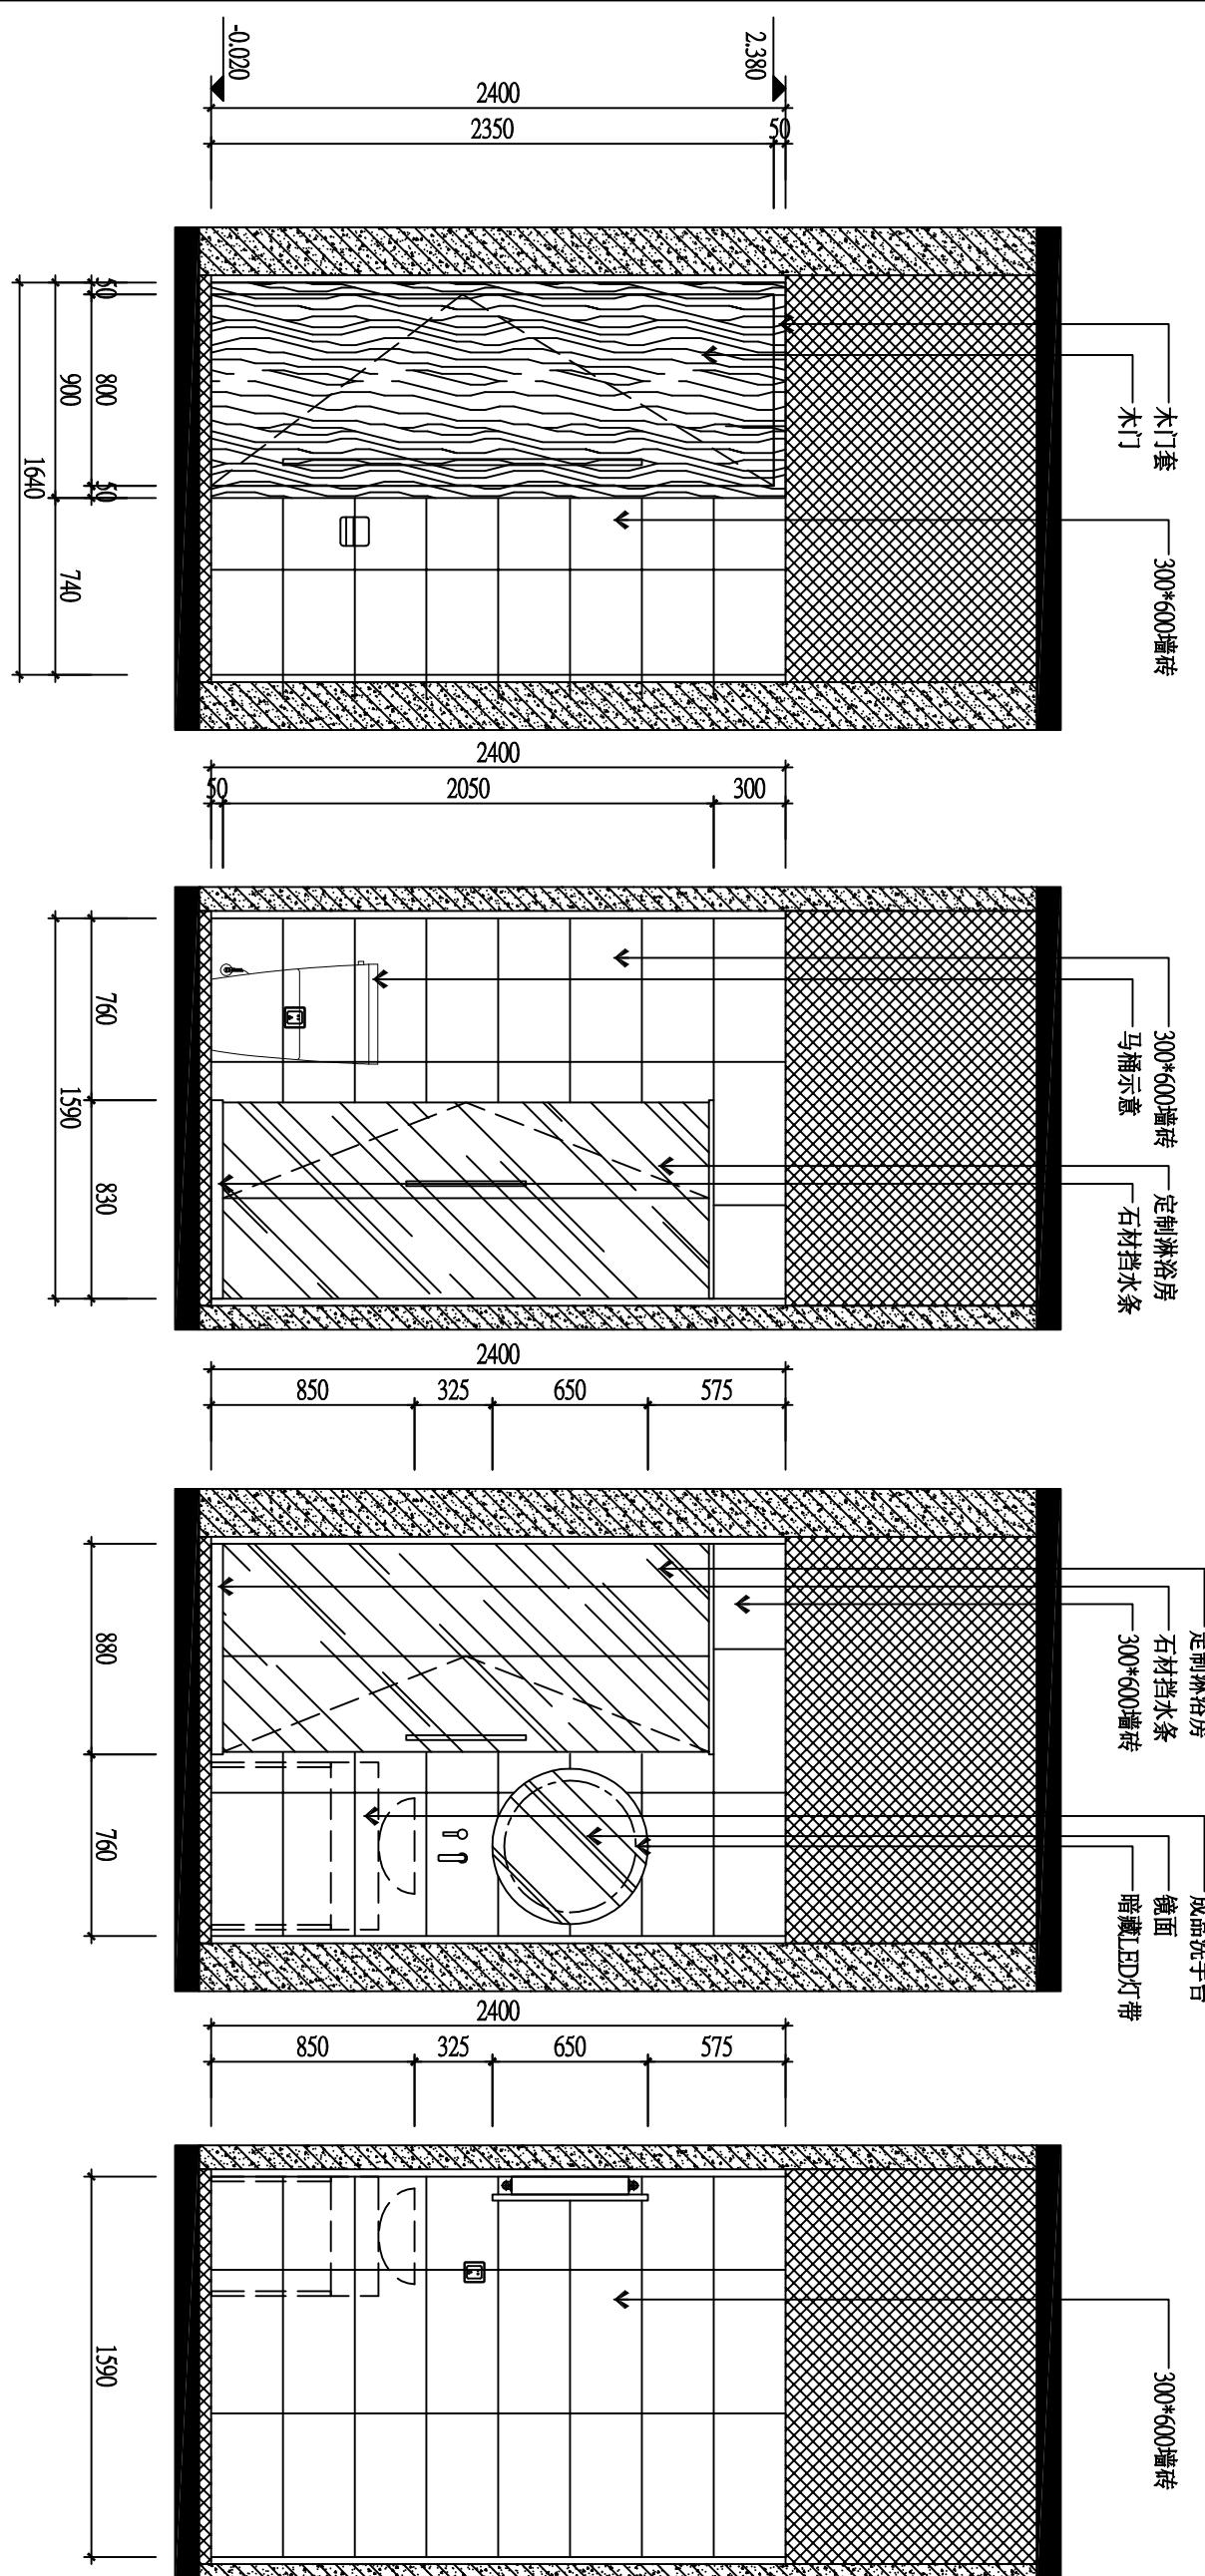

09 1F卫生间立面图
IFP-06 SCALE:1:30

10 1F卫生间立面图
IFP-06 SCALE:1:30

11 1F卫生间立面图
IFP-06 SCALE:1:30

12 1F卫生间立面图
IFP-06 SCALE:1:30

是
境
設
計

备
注
NOTE

- 本图未经同意，不得复制图纸及其设计任何部分。
- 所有图纸尺寸标注须在实际工地上复核及量度。
- 请勿按比例量度图纸，应采用已标明的尺寸。
- 本图纸必须和规格说明、合同条款及其有关图纸，并使用，如发现图纸内容有不符之处，必须立刻通知设计师。

业
主
CLIENT

项
目
名
称
PROJEC

总
负
责
人
PRINCIPAL

设
计
师
DESIGNER

绘
图
DRA

校
对
COLLATE

审
核
APPROVE


比
例
SCALE

日
期
DATE

图
名
DRAWING TITLE

图
号
SHEET NO

1F.E-08

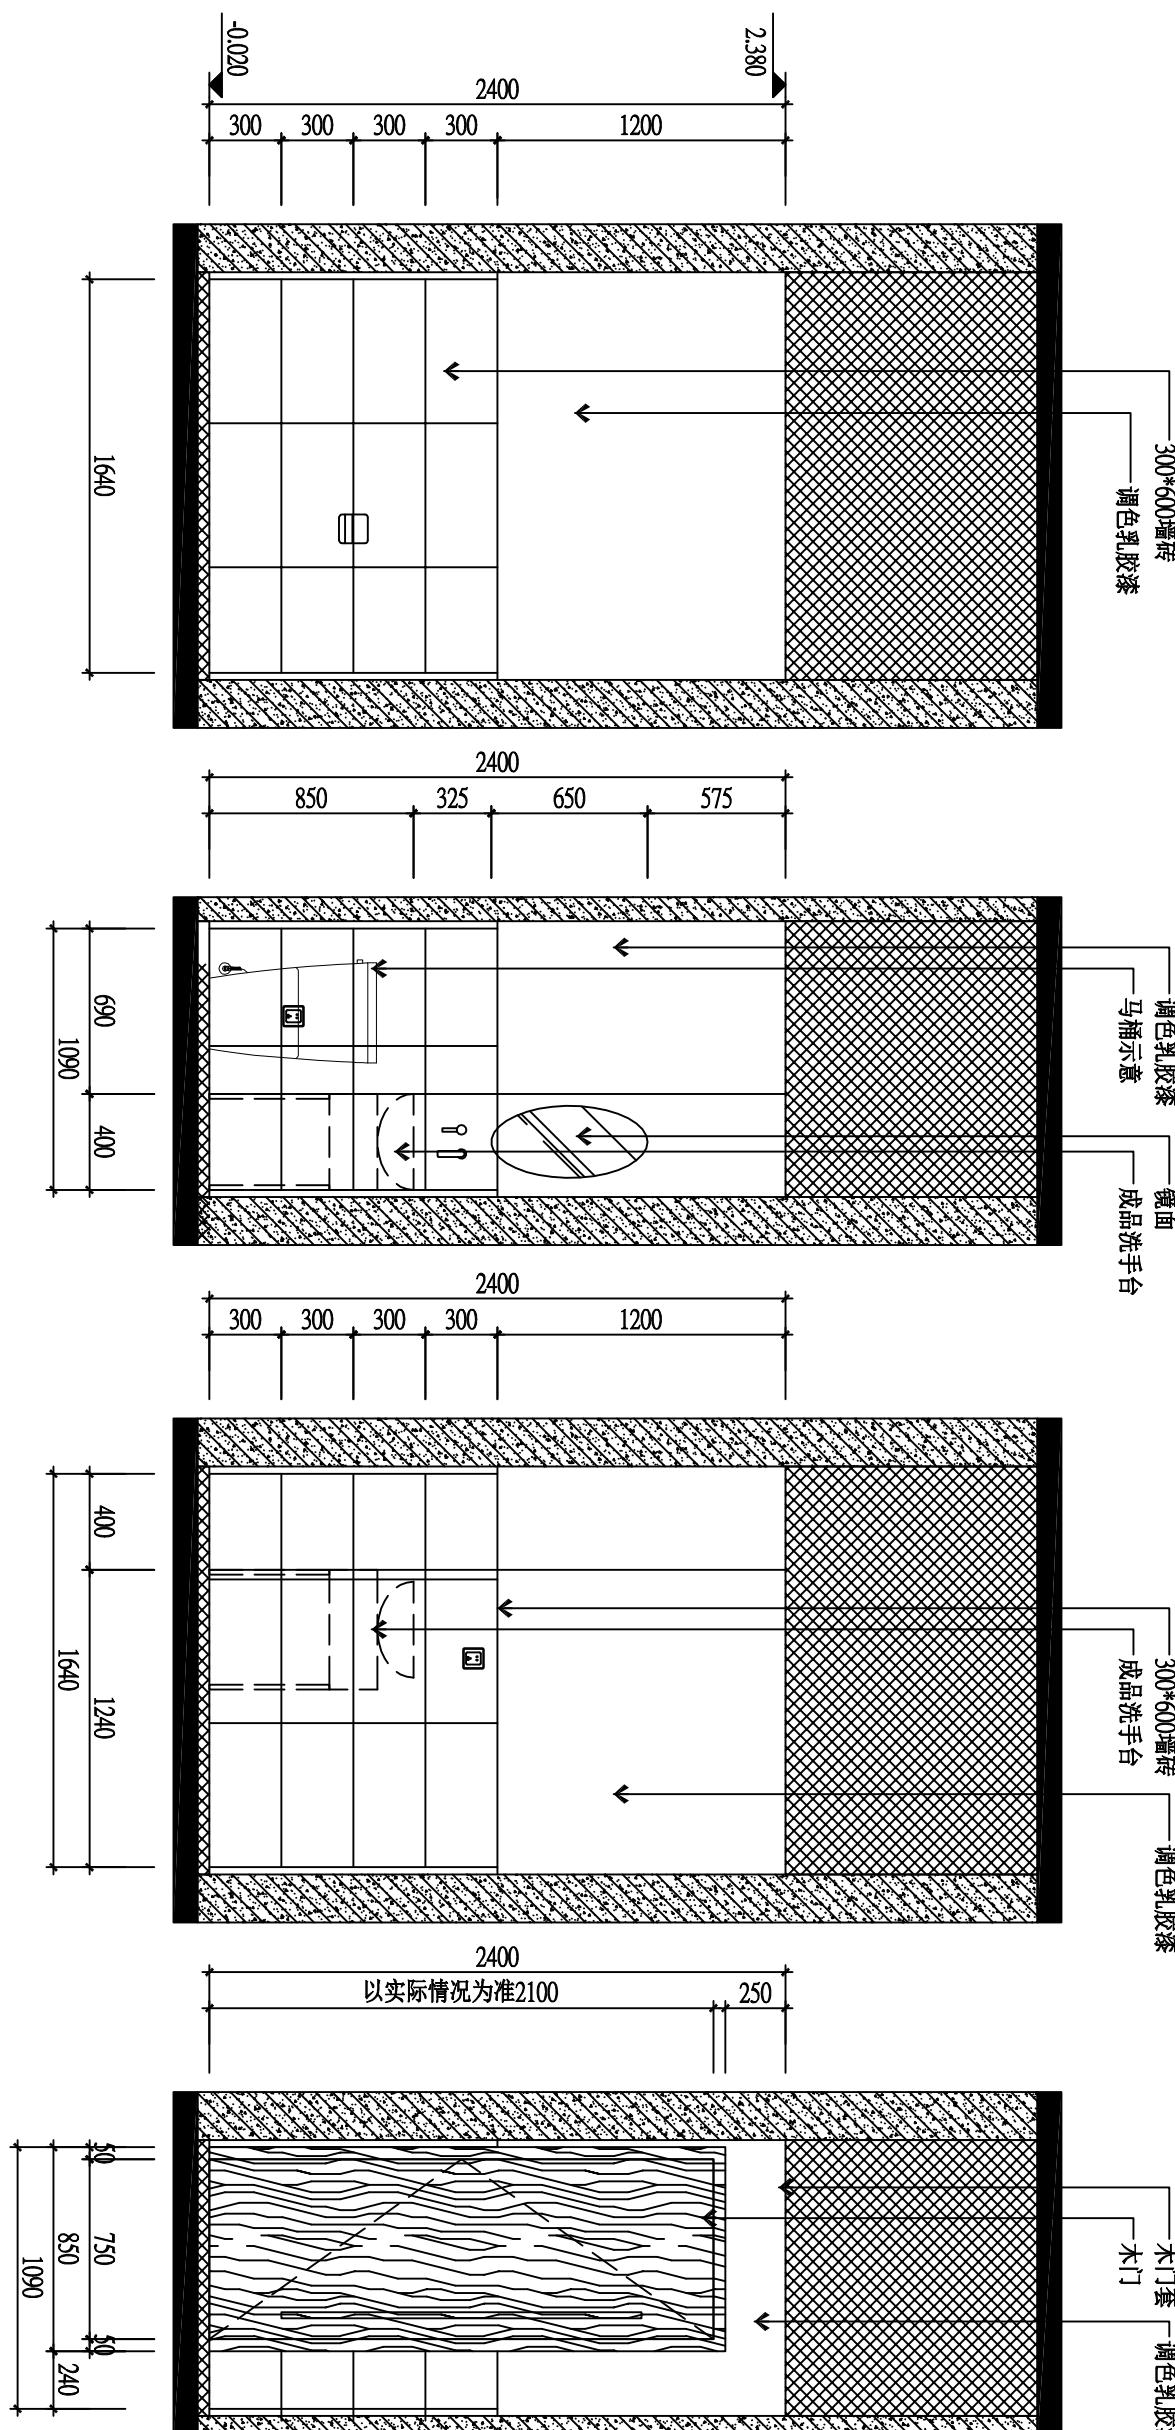

13 1F客卫立面图
FP46 SCALE:1:30

14 1F客卫立面图
FP46 SCALE:1:30

15 1F客卫立面图
FP46 SCALE:1:30

16 1F客卫立面图
FP46 SCALE:1:30

是
境
設
計

NOTE

□本图未经同意，不得复制图纸及其设计任一部分。


□有图尺寸标注须在实际工地上复核及量度。

□请勿按比例量度图纸，应采用已标明的尺寸。

□本图纸必须和规格说明、合同条款及其他有关图纸，并使用，如发现图纸内容有不符之处，必须立刻通知设计师。

业 主	CLIENT
项 目 名 称	PROJECT
总 负 责	PRINCIPAL
设 计	DESIGNER
绘 图	DRAWN BY
校 对	COLLATE
审 核	APPROVE
比 例	SCALE 1: 30
日 期	DATE 2020.07
图 名	DRAWING TITLE

2F立面布置图
图 号
SHEET NO
2F.E-01

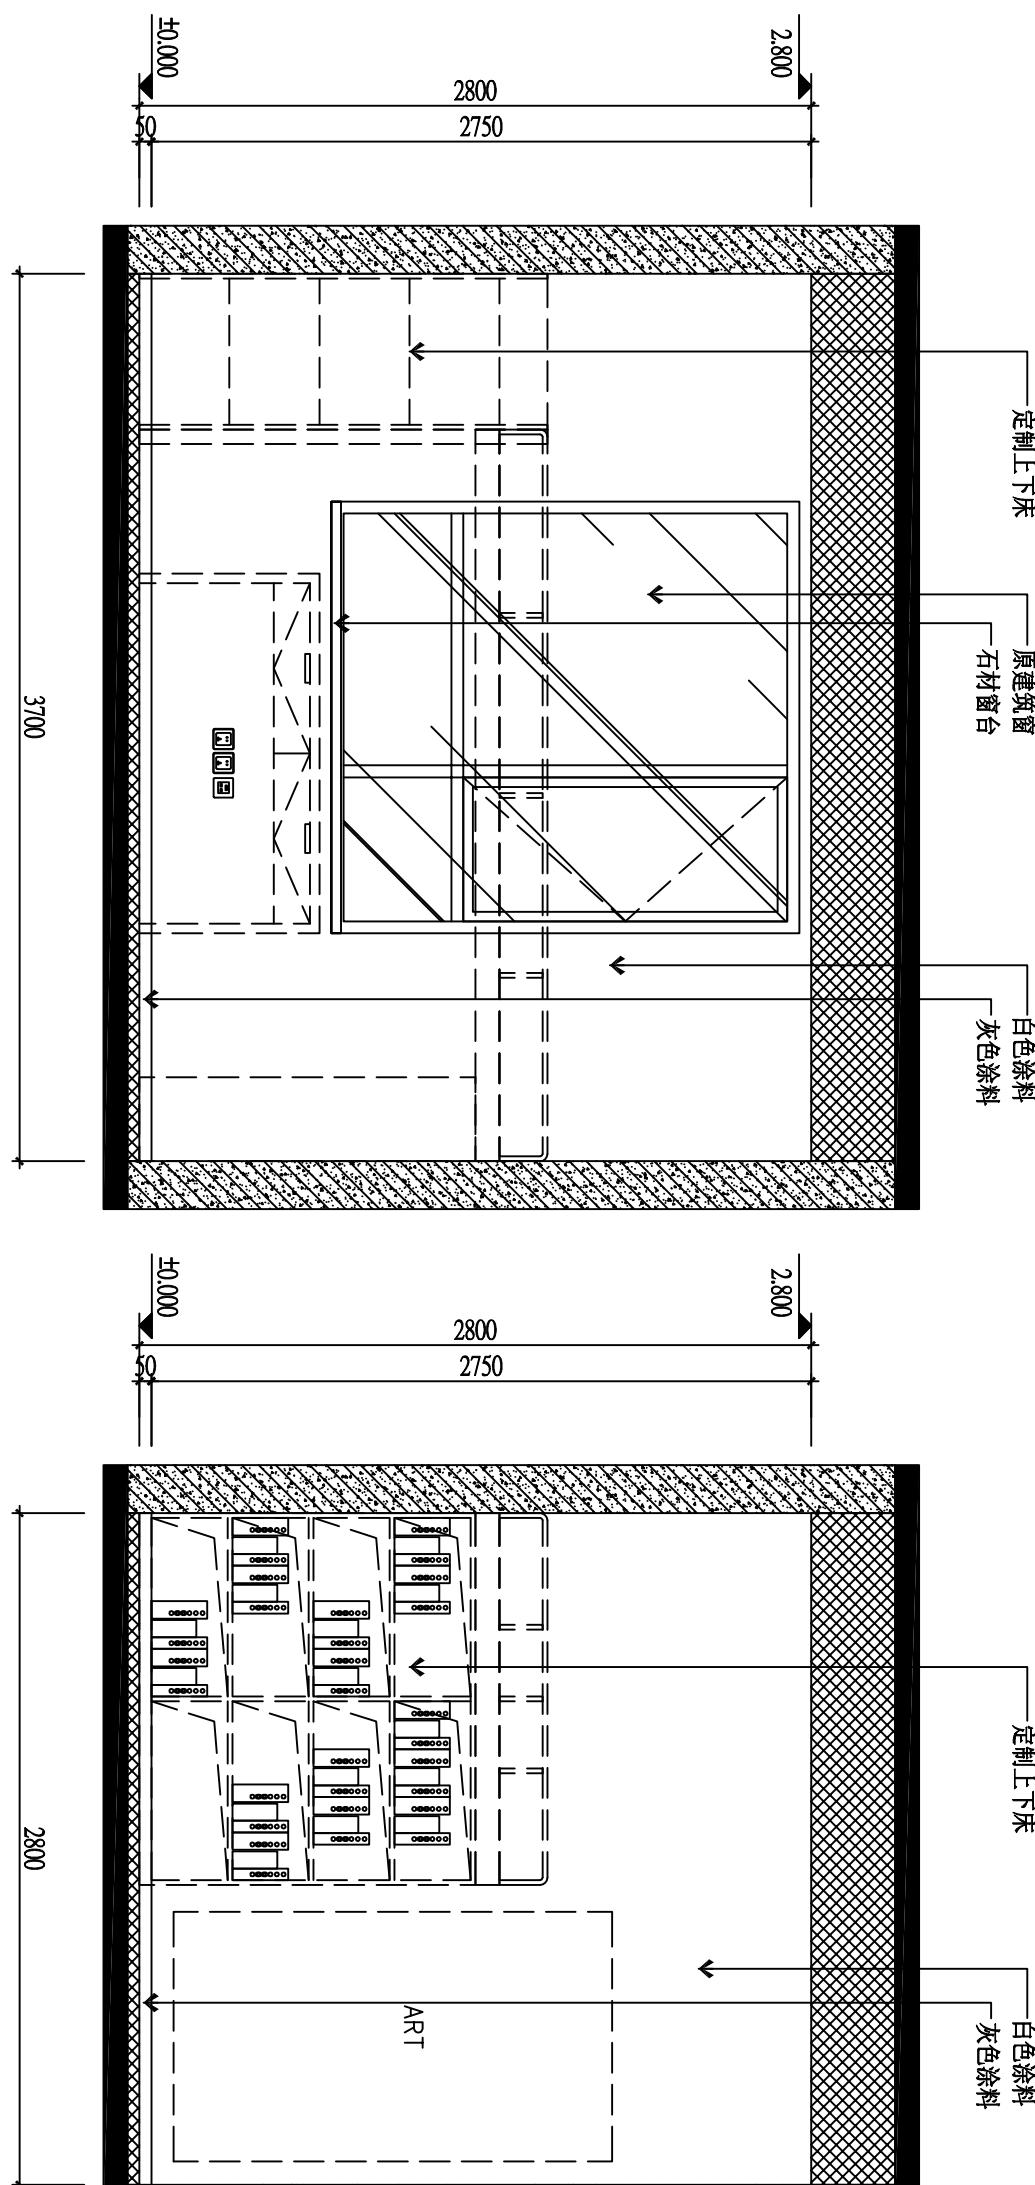


是境
设计

备 注
NOTE
□本图未经同意，不得复制图纸及其设计任一部分。
□有图尺寸标注须在实际工地上复核及量度。
□请勿按比例量度图纸，应采用已标明的尺寸。

□本图纸必须和规格说明、合同条款及其他有关图纸，并使用，如发现图纸内容有不符之处，必须立刻通知设计师。

业 主	CLIENT
项目名称 PROJECT	
总 负 责	龙湖椿山
PRINCIPAL	
设 计	
DESIGNER	
绘 图	
DRAWN BY	
校 对	
COLLATE	
审 核	
APPROVE	
比 例	定制上下床
SCALE	1: 30
日 期	2020.07
DATE	
图 名	DRAWING TITLE
SHEET NO	2F.F-02

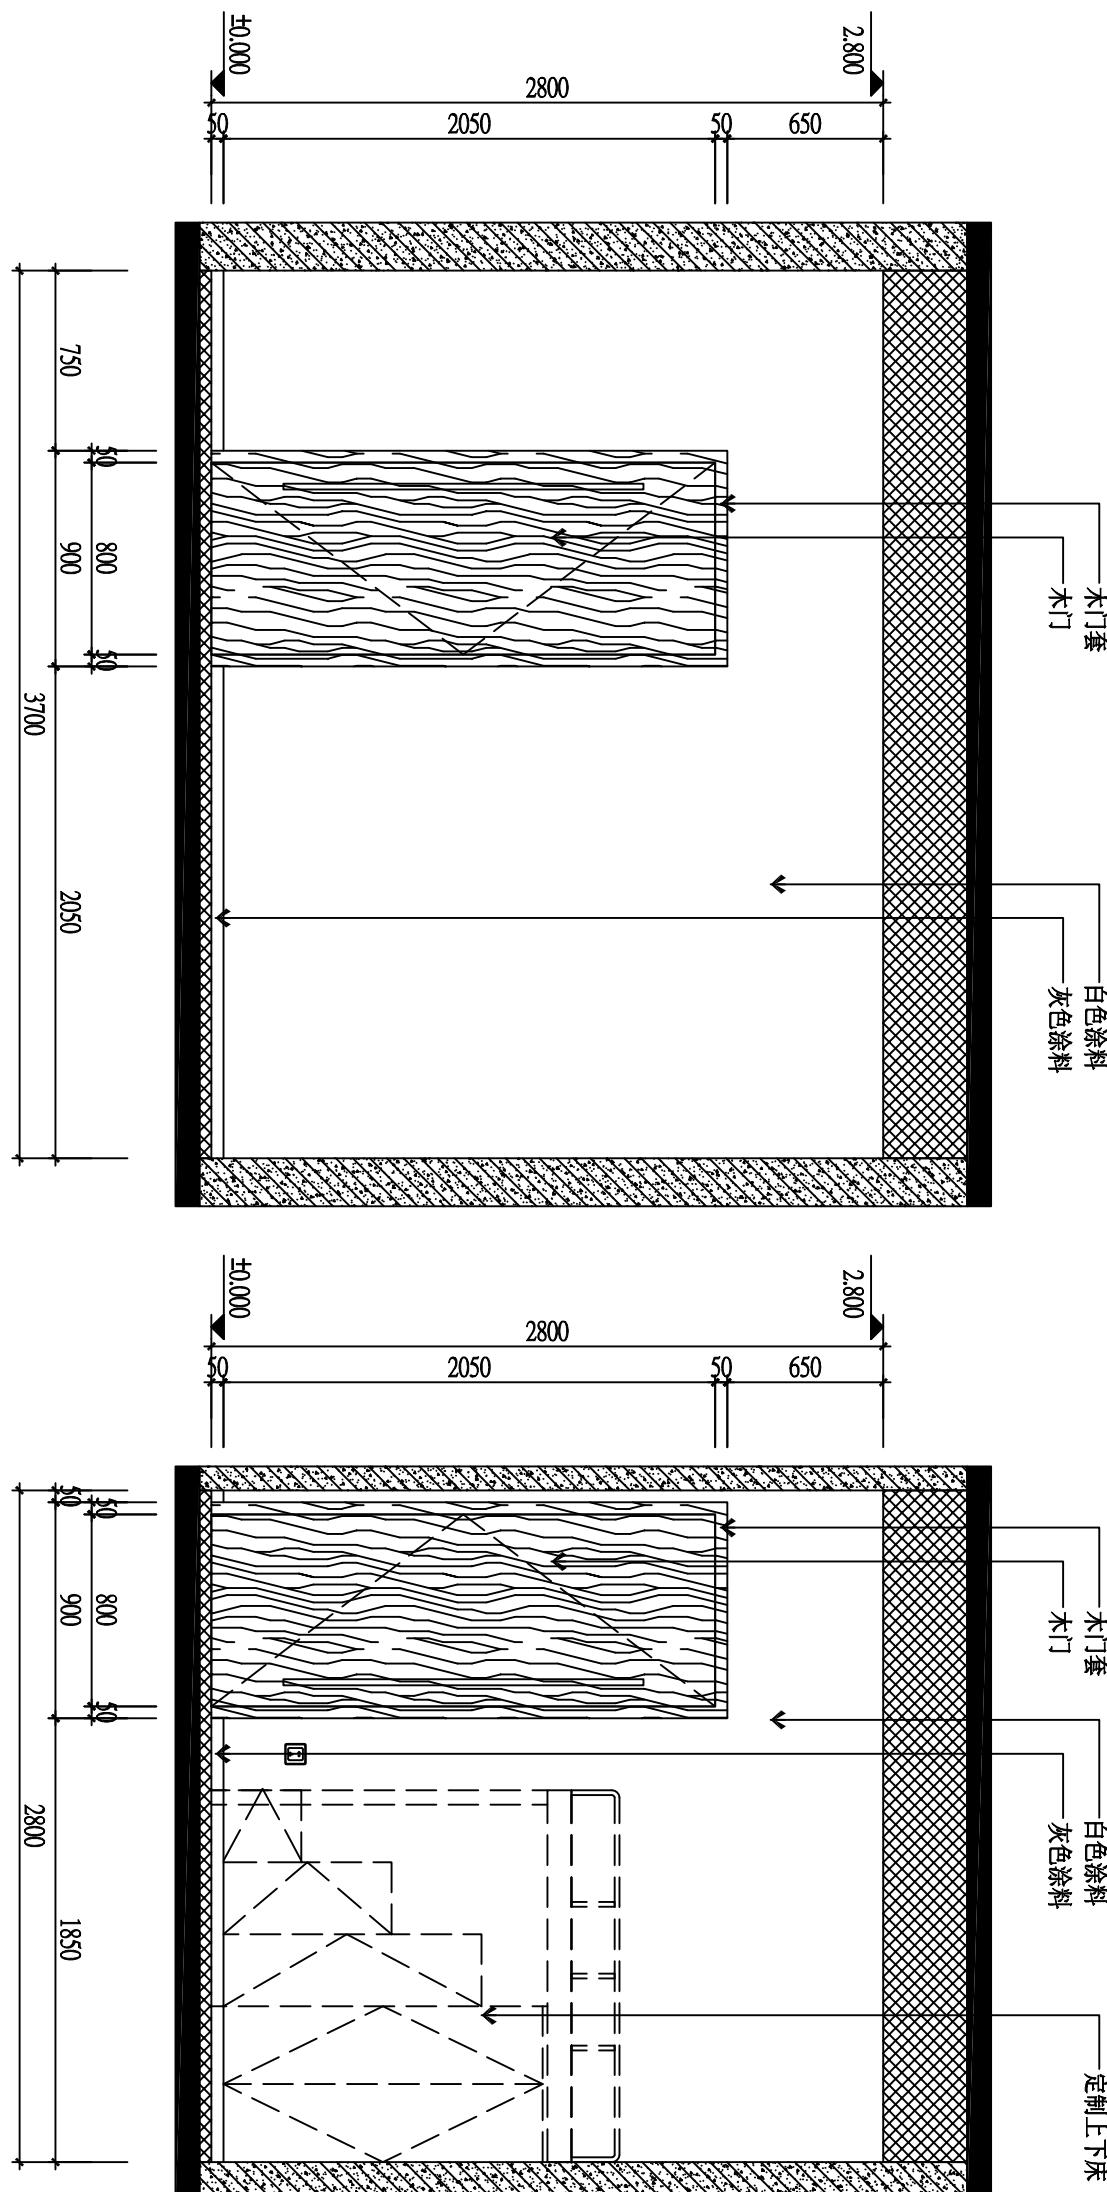

是境
设计

备 注
NOTE

□本图未经同意，不得复制图纸及其设计任何部分。
□有图纸尺寸标注须在实际工地上复核及量度。
□请勿按比例量度图纸，应采用已标明的尺寸。

□本图纸必须和规格说明、合同条款及其他有关图纸一并使用。如发现图纸内容有不符之处，必须立刻通知设计师。

业 主

CLIENT

项 目 名 称
PROJECT

总 负 责

PRINCIPAL

设 计

DESIGNER

绘 图

DRAWN BY

校 对

COLLATE

审 核

APPROVE

比 例

SCALE

1: 30

日 期

DATE

2020.07


图 名

DRAWING TITLE

2F立面布置图

图 号
SHEET NO

2F.F-03

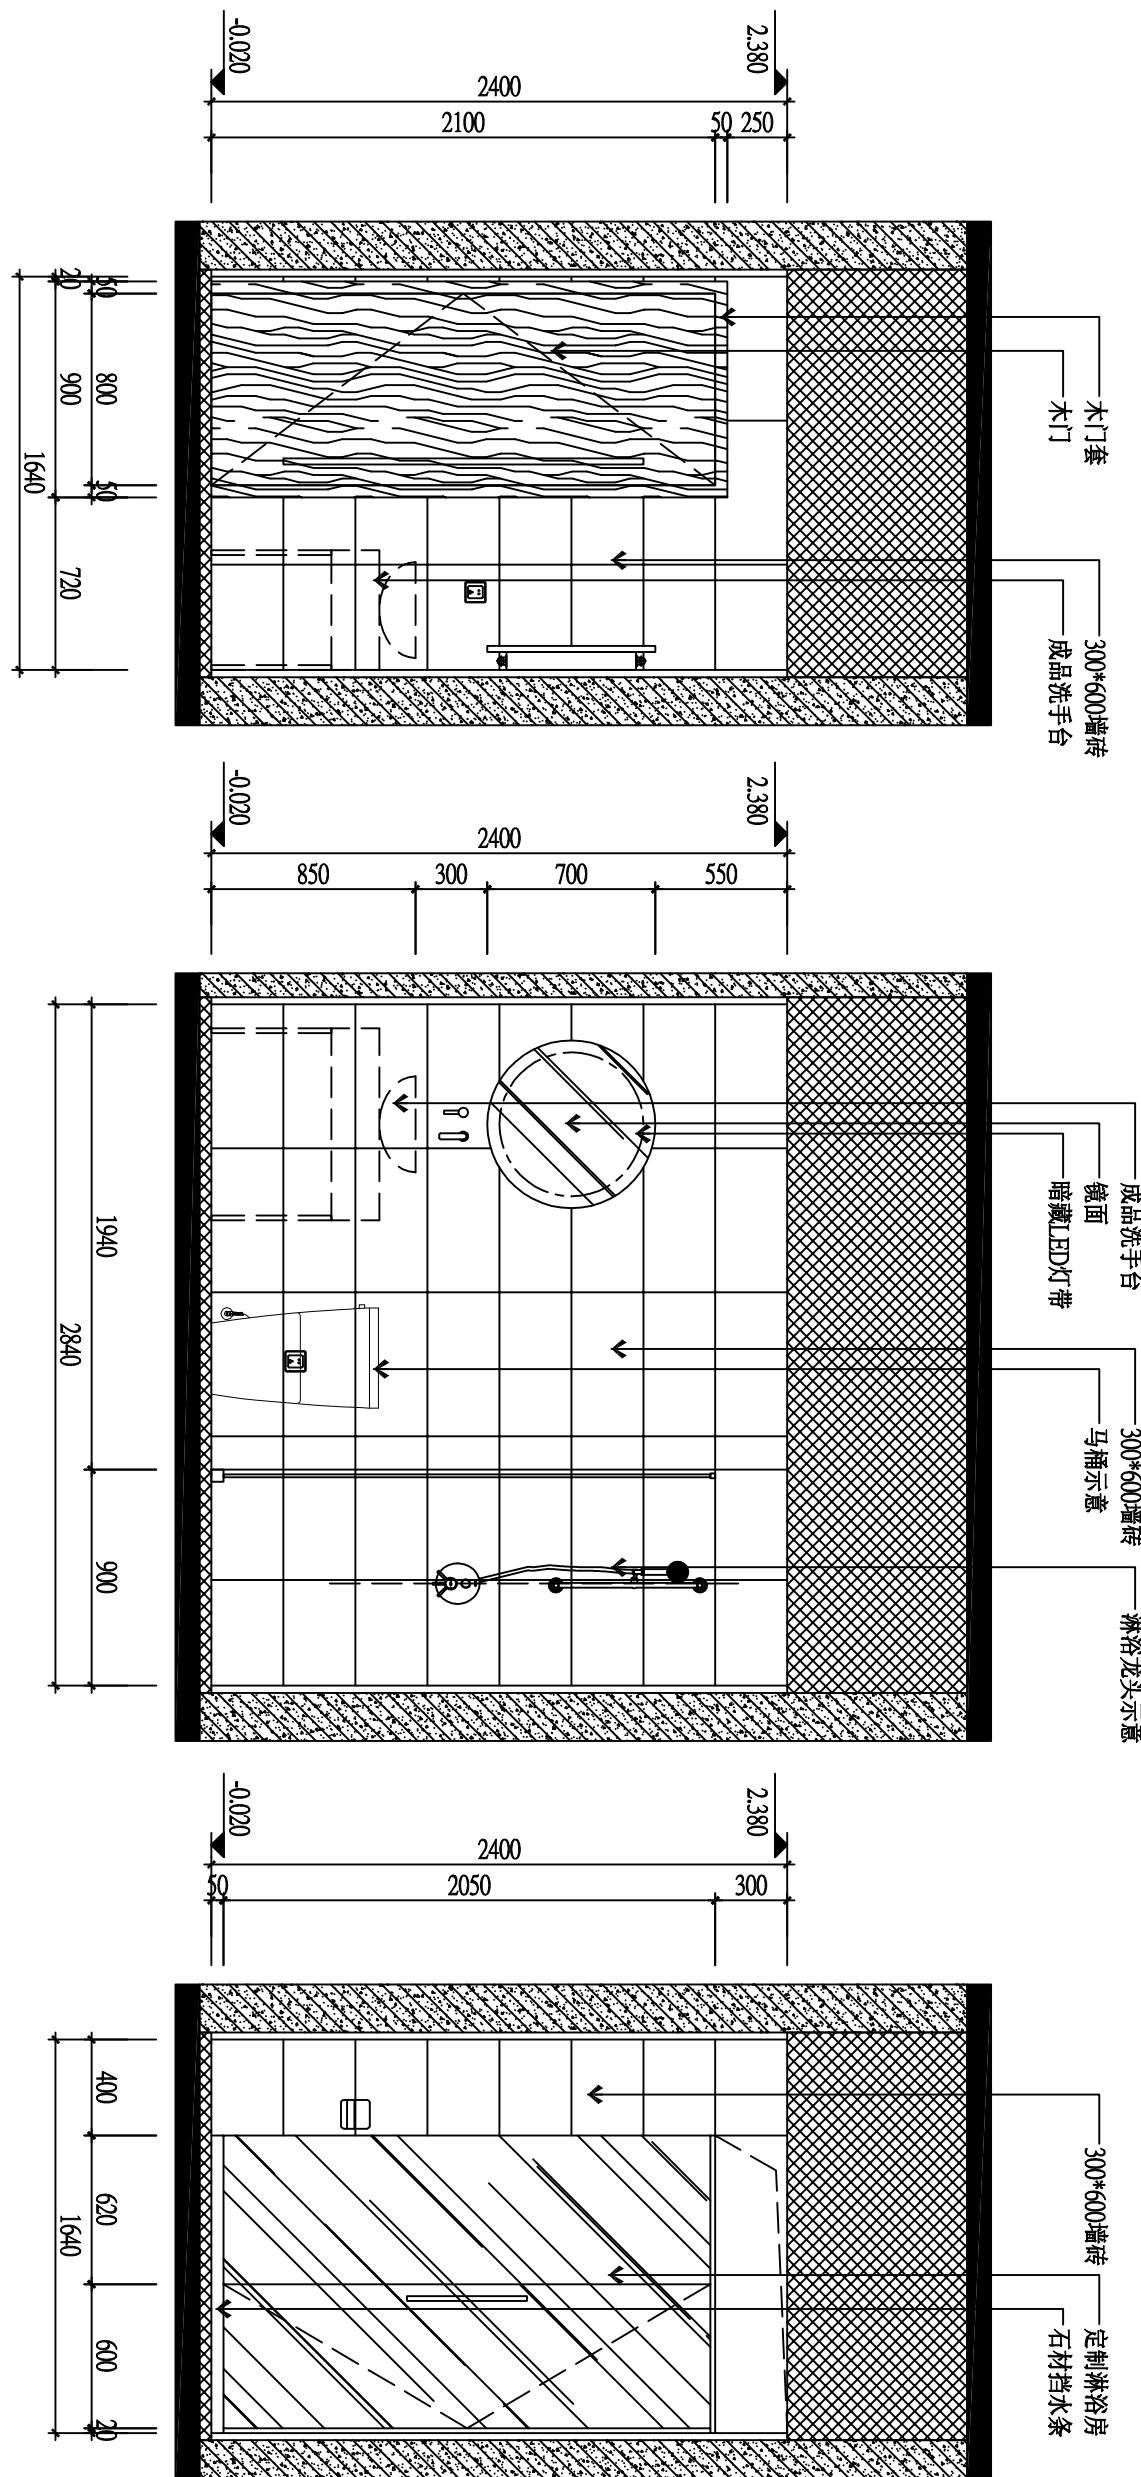

05 2F卫生间立面图
2FP-05 SCALE:1:30

06 2F卫生间立面图
2FP-06 SCALE:1:30

07 2F卫生间立面图
2FP-06 SCALE:1:30

是 境
設 計

备注

□在未经同意前，不得复制图纸及其设计
任何部份。

- 所有图纸尺寸标注须在实际工地上复核及量度。
- 请勿按比例量度图纸，应采用已标明的尺寸。
- 本图纸必须和规格说明、合同条款及其有关图纸一并使用，如发现图纸内容有不符之处，必须立刻通知设计师。

業主
CLIENT

14

项目名称
PROJECT

P 10

RINC

卷三

三

1

1

1

300*600牆砖
成品洗手台
木門套
木門

成品壳子
— 镜面
— 暗藏LED灯带

足利淋浴房
原建筑窗

畫
砖

The image displays three architectural floor plans stacked vertically, representing different levels of a building. Each plan includes a grid system, room dimensions, and specific features indicated by arrows and symbols.

Top Plan: This plan shows a rectangular room divided into a 7x4 grid of smaller rooms. The total width is 2400 mm, and the height is 2.380 m. The top edge has a dimension of -0.020. The right side features a vertical hatched pattern. A horizontal arrow points left from the center of the room.

Middle Plan: This plan shows a room with a total width of 2400 mm and a height of 2.380 m. The top edge has a dimension of -0.020. The right side features a vertical hatched pattern. The floor contains several hatching patterns: diagonal lines in the top section, a grid pattern in the center, and wavy lines at the bottom. Arrows point left from the center and bottom sections.

Bottom Plan: This plan shows a room with a total width of 2400 mm and a height of 2.380 m. The top edge has a dimension of -0.020. The right side features a vertical hatched pattern. The floor contains a grid pattern in the top section and wavy lines at the bottom. Arrows point left from both sections.

The figure consists of three separate vertical bar charts, each with a y-axis ranging from 0 to 1000. The first chart has values 900, 2840, and 1940. The second chart has values 480, 1310, and 400. The third chart has values 600, 1340, 700, and 740.

Category	Value 1	Value 2	Value 3	
Chart 1	900	2840	1940	
Chart 2	480	1310	400	
Chart 3	600	1340	700	740

08
2F-P-06
2F卫生间立面图
SCALE:1/30

09
2F-P06
2F卫生间立面图
SCALE:1/30

10
2F-06
2F卫生间立面图
SCALE:1:300

是境設計

备 注


□在未经同意前，不得复制图纸及其设计任何部份。

- 所有图纸尺寸标注须在实际工地上复核及量度。
- 请勿按比例量度图纸，应采用已标明的尺寸。
- 本图纸必须和规格说明、合同条款及其他有关图纸一并使用，如发现图纸内容有不符之处，必须立刻通知设计院。

業主
CLIENT


项目名称
PROJECT
龙湖椿山

300*600墙砖
定制淋浴房
石材挡水条

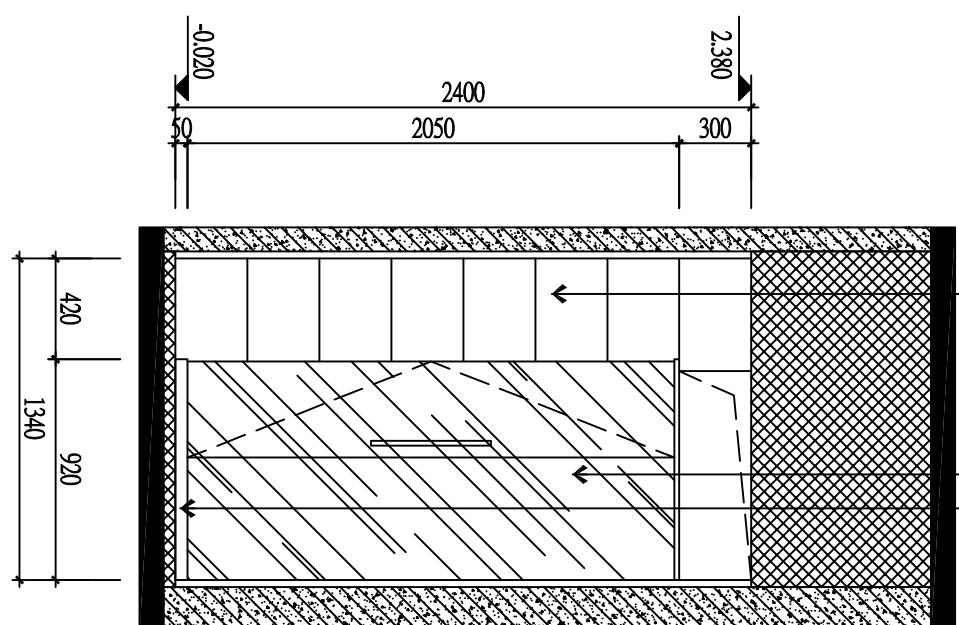

11
2FP-06
2F卫生间立面图
SCALE:1/30

12
2F卫生间立面图
SCALE:1:300

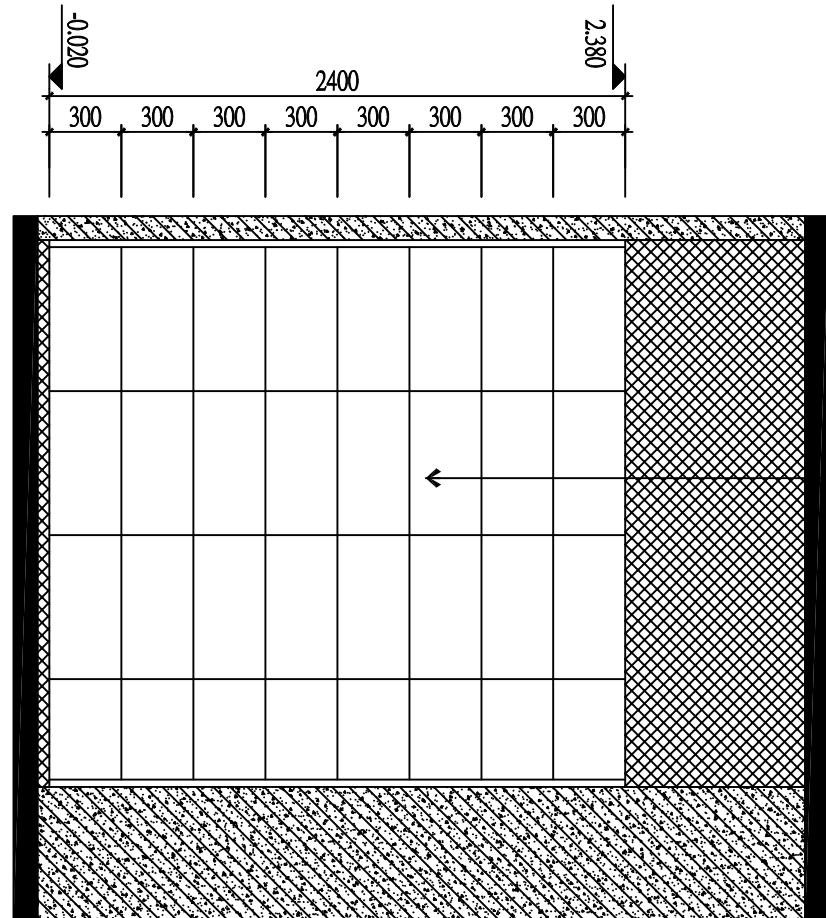

11
2FP-06
2F卫生间立面图
SCALE:1/30

12
2F卫生间立面图
SCALE:1:300

是境設計

备注
NOTE

□本图未经同意，不得复制图纸及其设计任何部分。
□有图纸尺寸标注须在实际工地复核及量度。

□勿按比例量度图纸，应采用已标明的尺寸。

□本图纸必须和规格说明、合同条款及其他有关图纸一并使用。如发现图纸内容有不符之处，必须立刻通知设计师。

业 主
CLIENT

项 目 名 称
PROJECT
龙湖椿山

总 负 责
PRINCIPAL

设 计
DESIGNER

绘 图
DRAWN BY

校 对
COLLATE

审 核
APPROVE

比 例
SCALE


日 期
DATE

图 名
DRAWING TITLE

图 号
SHEET NO

3F立面布置图

3F.E-01

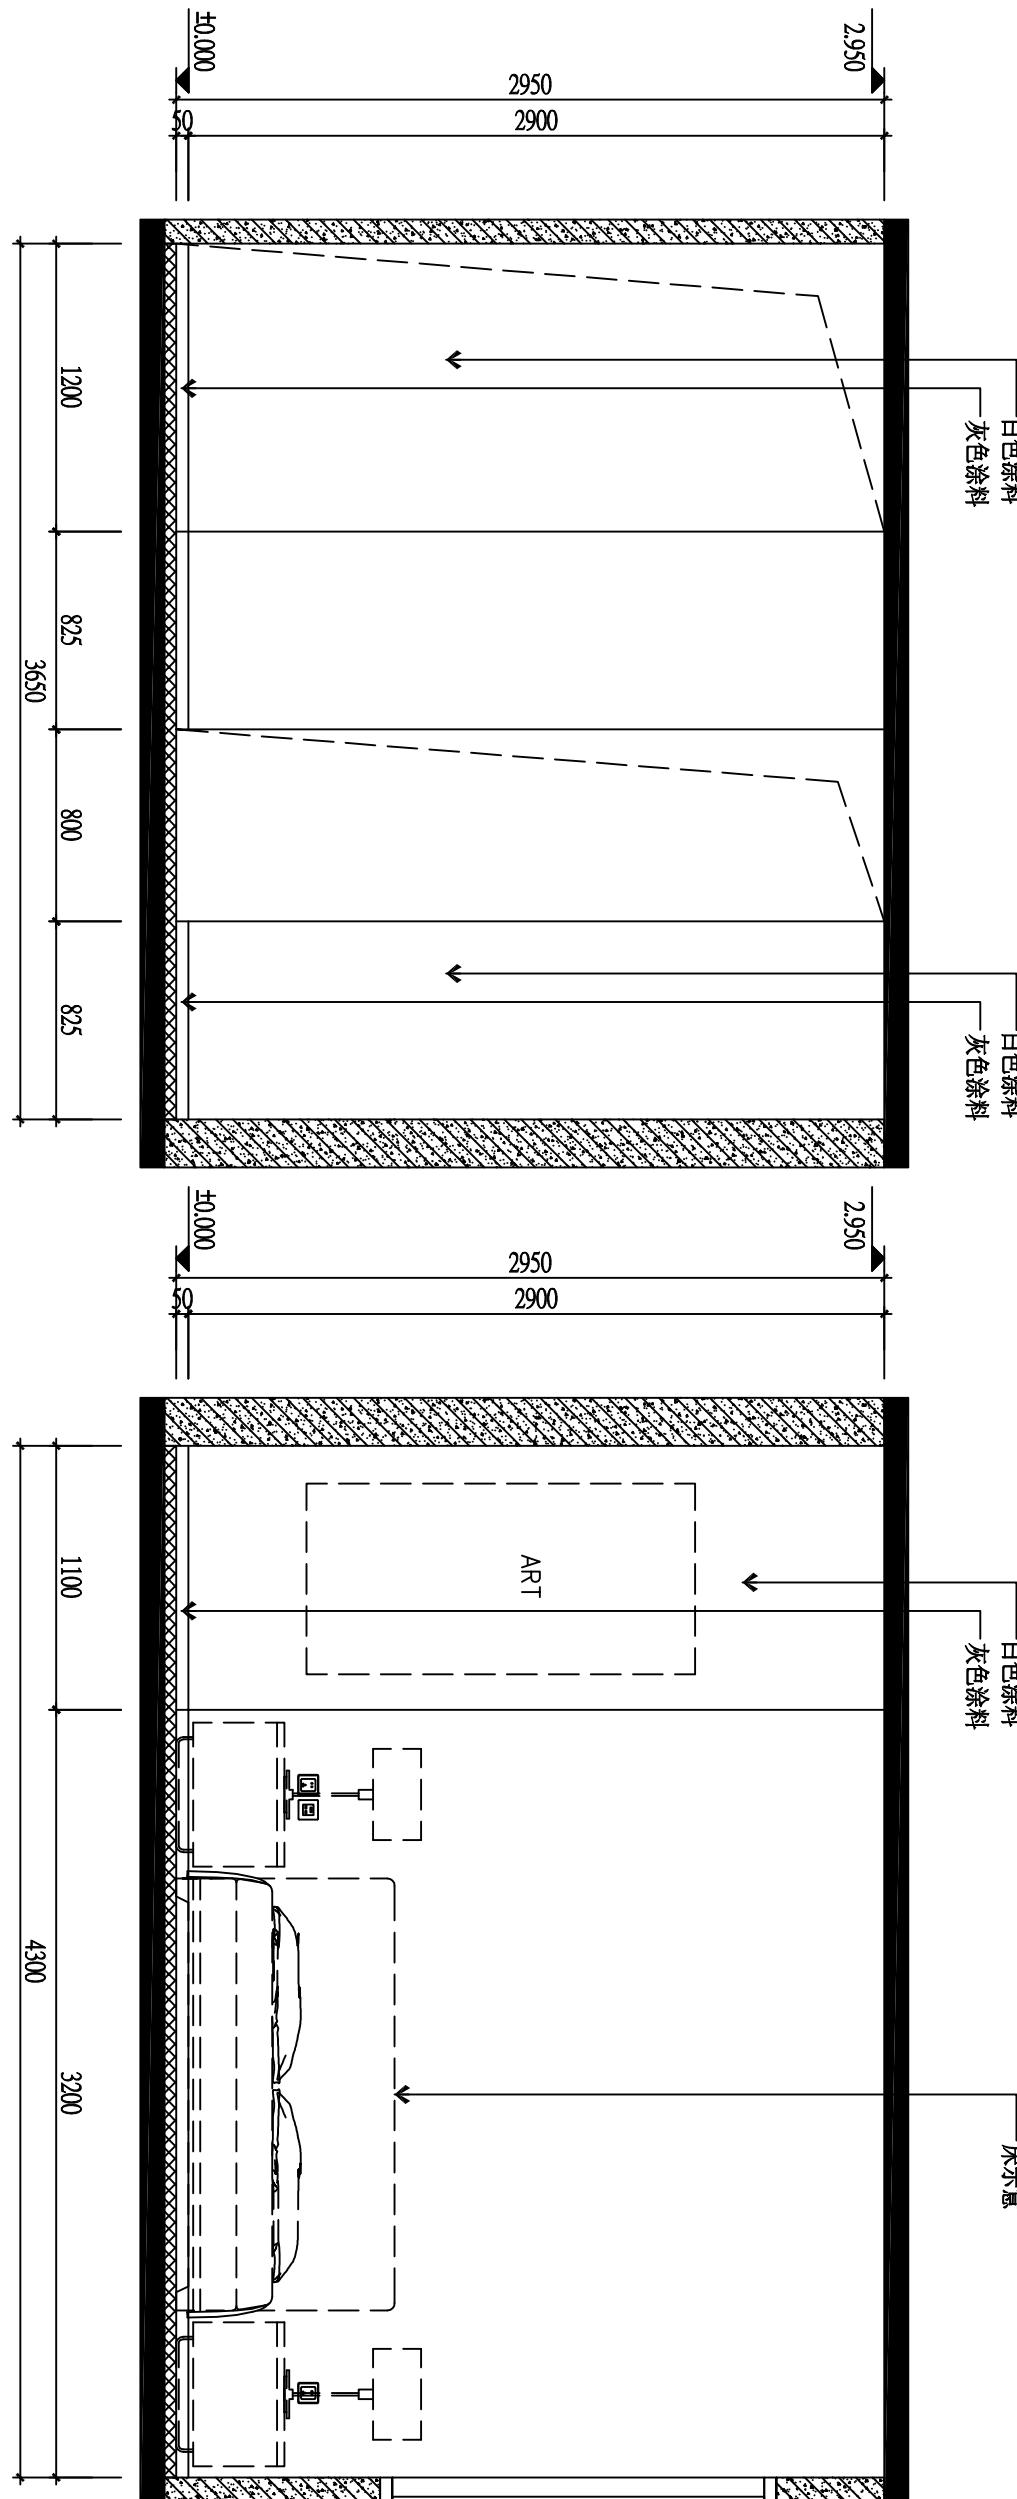

01 3F主入口立面图
3FP06 SCALE:1:30

02 3F主卧立面图
3FP06 SCALE:1:30

是境
设计

备
注
NOTE

□本图未经同意，不得复制图纸及其设计任一部分。
□有图纸尺寸标注须在实际工地复核及量度。

□勿按比例量度图纸，应采用已标明的尺寸。

□本图纸必须和招标说明、合同条款及其他有关图纸，并使用，如发现图纸内容有不符之处，必须立刻通知设计师。

项 目 名 称	业 主
PROJEC	CLIENT
总 负 责	项 目 名 称
PRINCIPAL	龙湖椿山
设 计	项 目 编 号
DESIGNER	03
绘 图	图 号
DRAWN BY	3F.E-02
校 对	图 名
COLLATE	3F 立面布置图
审 核	图 号
APPROVE	04
比 例	设计人
SCALE	刘洋
DATE	审核人
2020.07	王伟

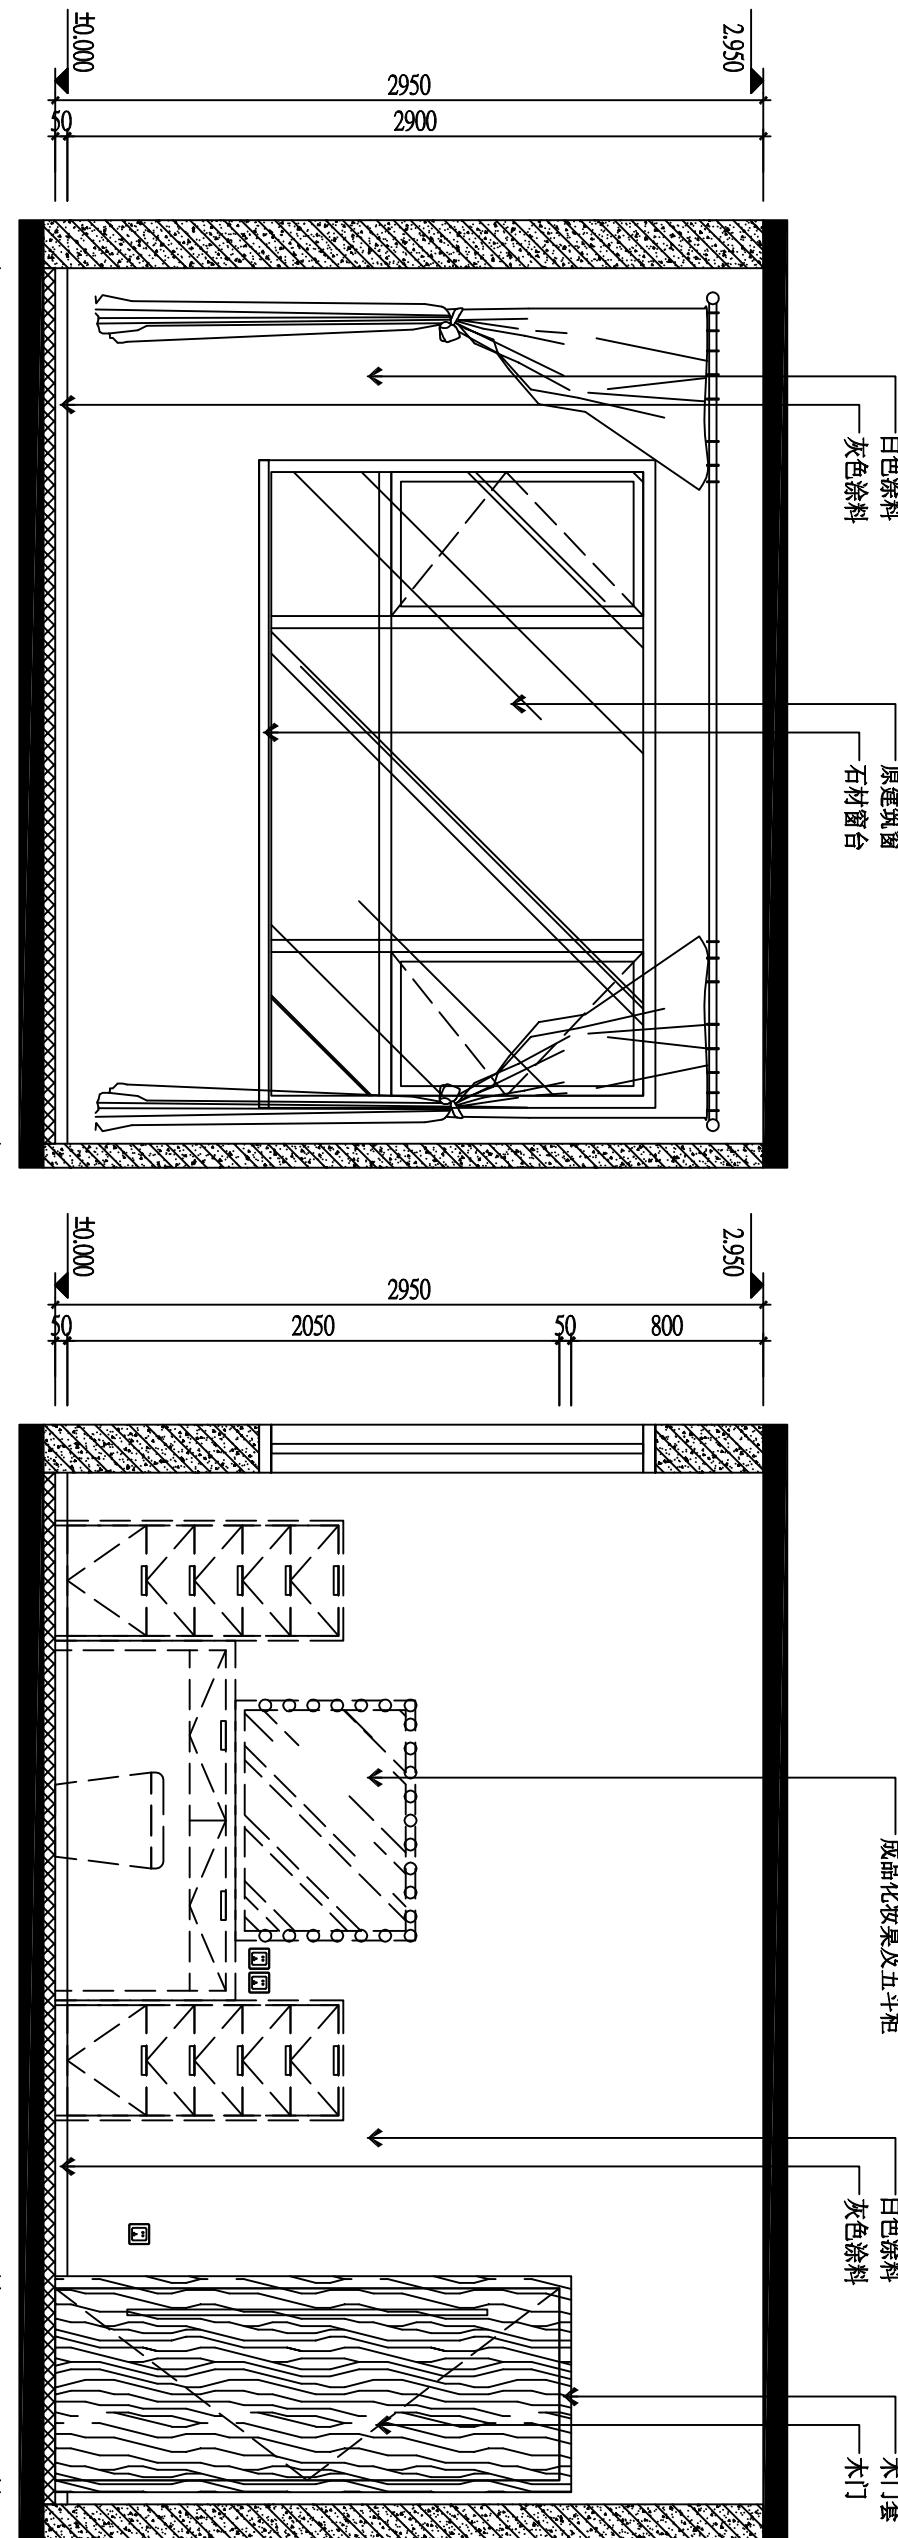


图 名	3F 立面布置图
DRAWING TITLE	
SHEET NO	

03 3F主卧立面图
SCALE:1:30

04 3F主卧立面图
SCALE:1:30

是境
设计

备 注
NOTE

- 本图未经同意，不得复制图纸及其设计任何部分。
- 有图纸尺寸标注须在实际工地上复核及量度。
- 请勿按比例量度图纸，应采用已标明的尺寸。
- 本图纸必须和规格说明、合同条款及其他有关图纸一并使用。如发现图纸内容有不符之处，必须立刻通知设计师。

业 主

CLIENT

项目名称
PROJECT

龙湖椿山

总 负 责
PRINCIPAL

设 计
DESIGNER

绘 图
DRAWN BY

校 对
COLLATE

审 核
APPROVE

比 例
SCALE

1: 30

日 期
DATE


2020.07

图 名
DRAWING TITLE

3F立面布置图

图 号
SHEET NO

3F.E-03

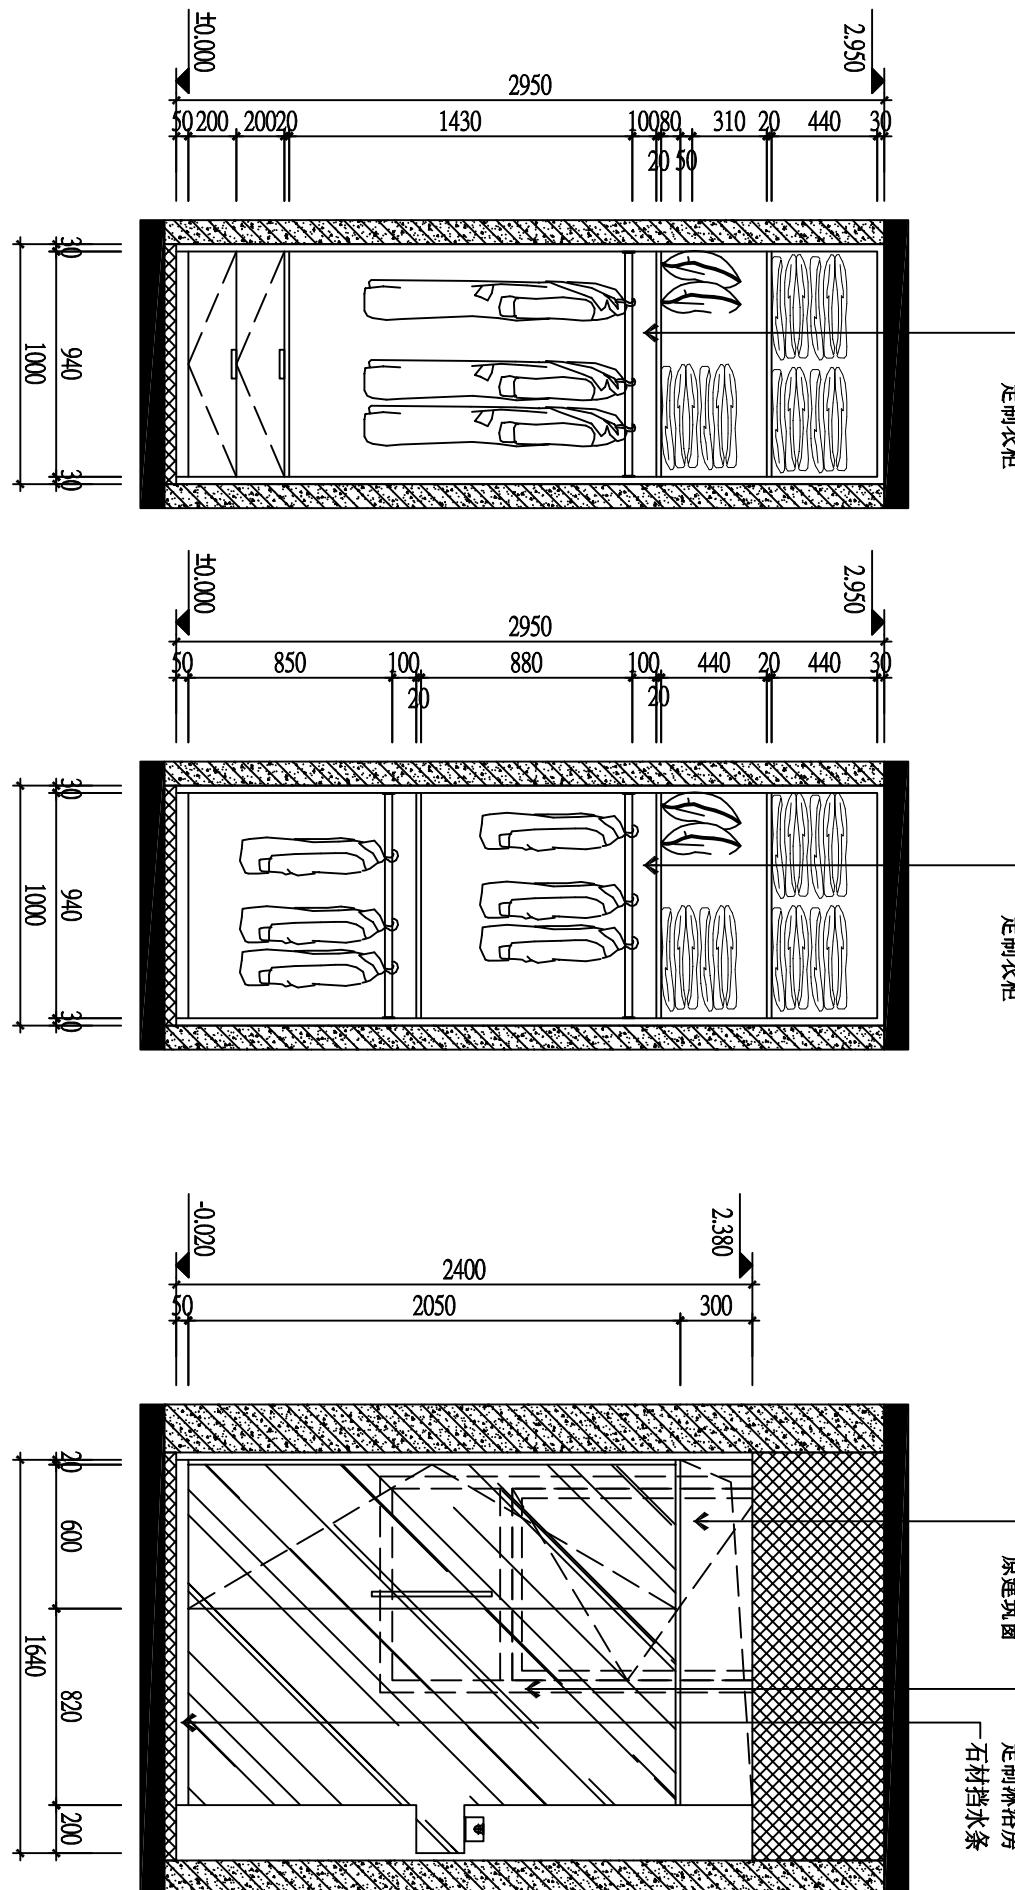

05 3F衣帽间立面图
SCALE:1/30

06 3F衣帽间立面图
SCALE:1/30

07 3F主卫立面图
SCALE:1/30

是 境
設 計

备注
NOTE

□本图未经同意，不得复制图纸及其设计任一部分。
□有图纸尺寸标注须在实际工地上复核及量度。

□勿按比例量度图纸，应用已标明的尺寸。

□本图纸必须和规格说明、合同条款及其他有关图纸一并使用。如发现图纸内容有不符之处，必须立刻通知设计师。

业主
CLIENT

项目名称
PROJECT
龙湖椿山

总负责人
PRINCIPAL

设计
DESIGNER

绘图
DRAWN BY

校对
COLLATE

审核
APPROVE

比例
SCALE

例 1: 30


日期
DATE

2020.07

图名
DRAWING TITLE

3F立面布置图

图号
SHEET NO

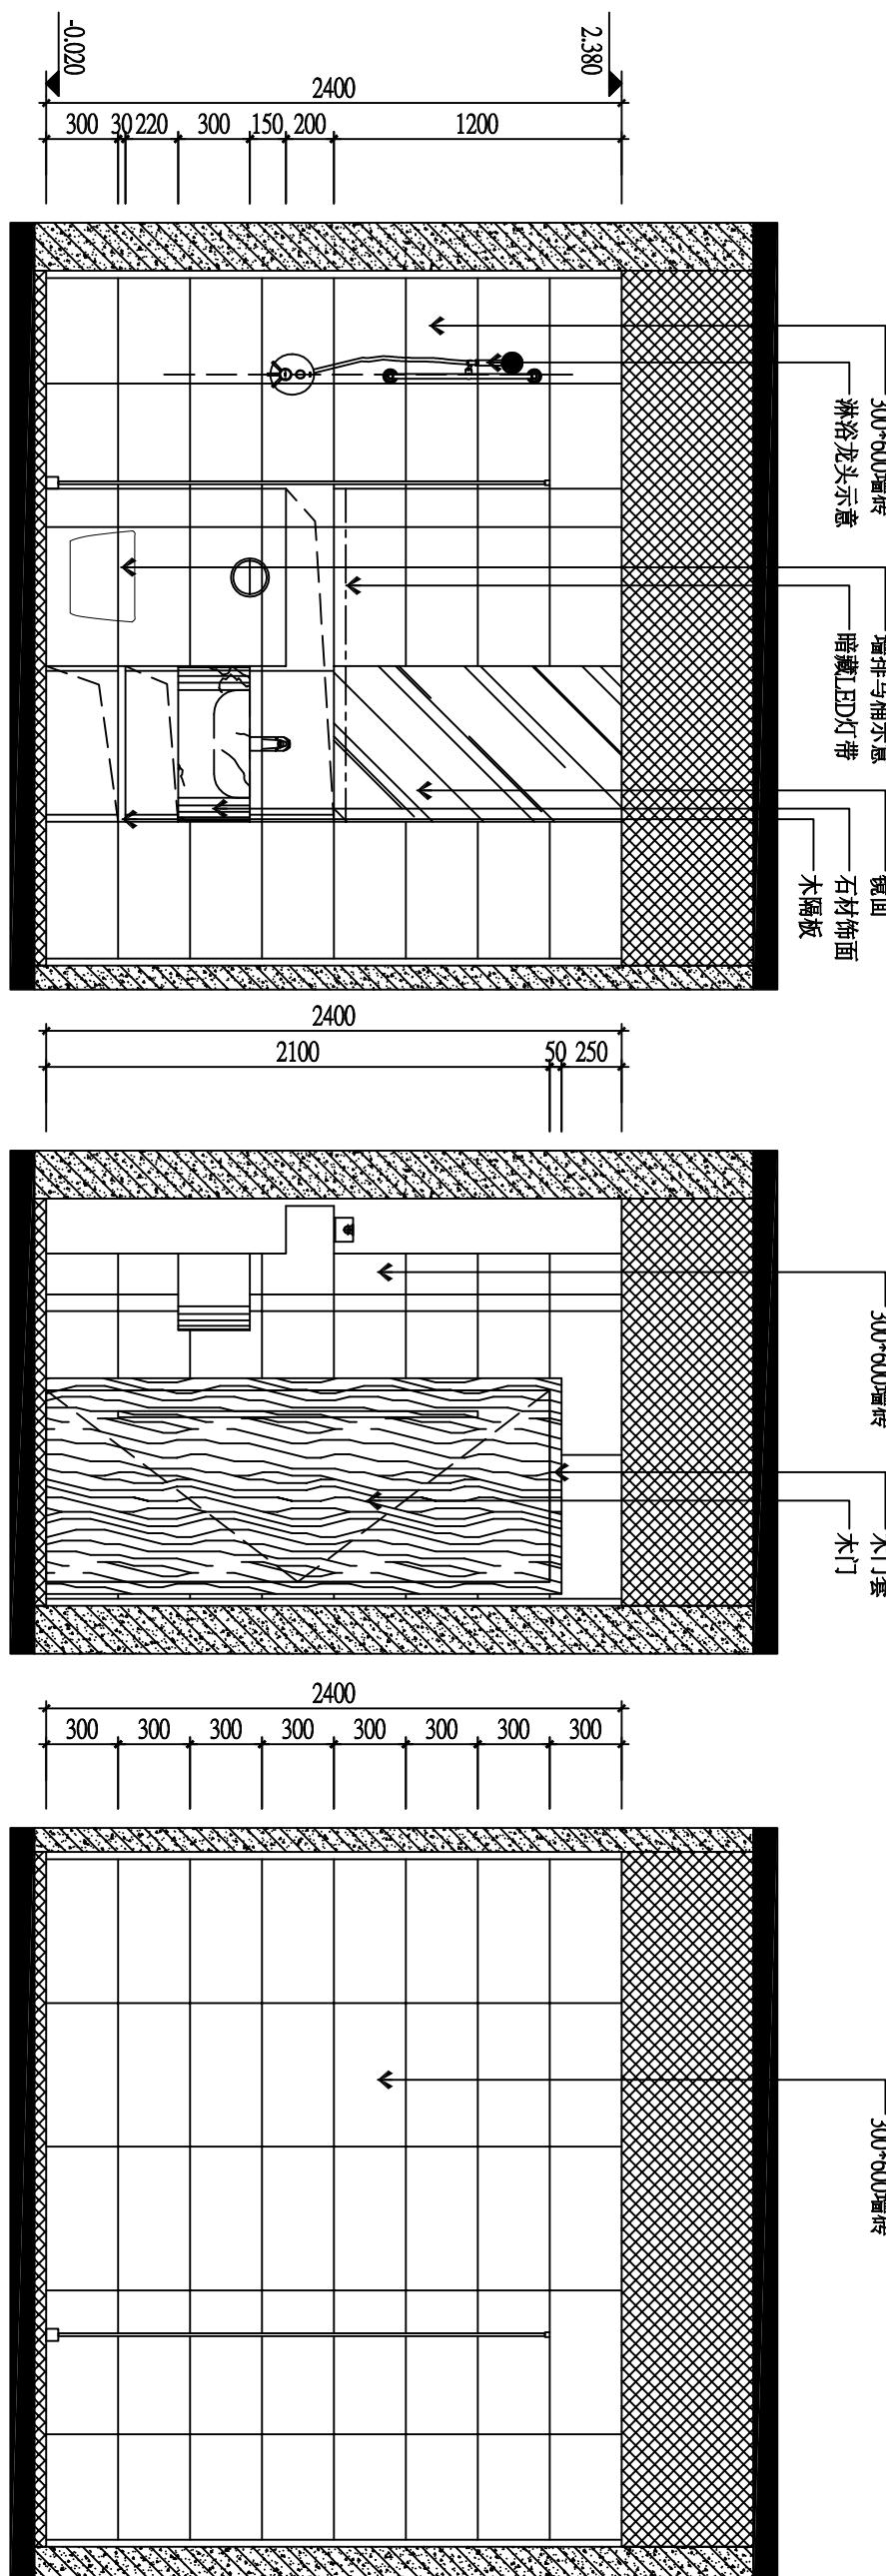

08 3F主卫立面图
3FP-06 SCALE:1:30

09 3F主卫立面图
3FP-06 SCALE:1:30

10 3F主卫立面图
3FP-06 SCALE:1:30

是境
设计

备注
NOTE

□本图未经同意，不得复制图纸及其设计任一部分。
□有图纸尺寸标注须在实际工地上复核及量度。

□勿按比例量度图纸，应用已标明的尺寸。

□本图纸必须和规格说明、合同条款及其有关图纸，并使用，如发现图纸内容有不符之处，必须立刻通知设计师。

业主
CLIENT

项目名称
PROJECT
龙湖椿山

总负责
PRINCIPAL

设计
DESIGNER

绘图
DRAWN BY

校对
COLLATE


审核
APPROVE

比例
SCALE

日期
DATE

图名
DRAWING TITLE

图号
SHEET NO

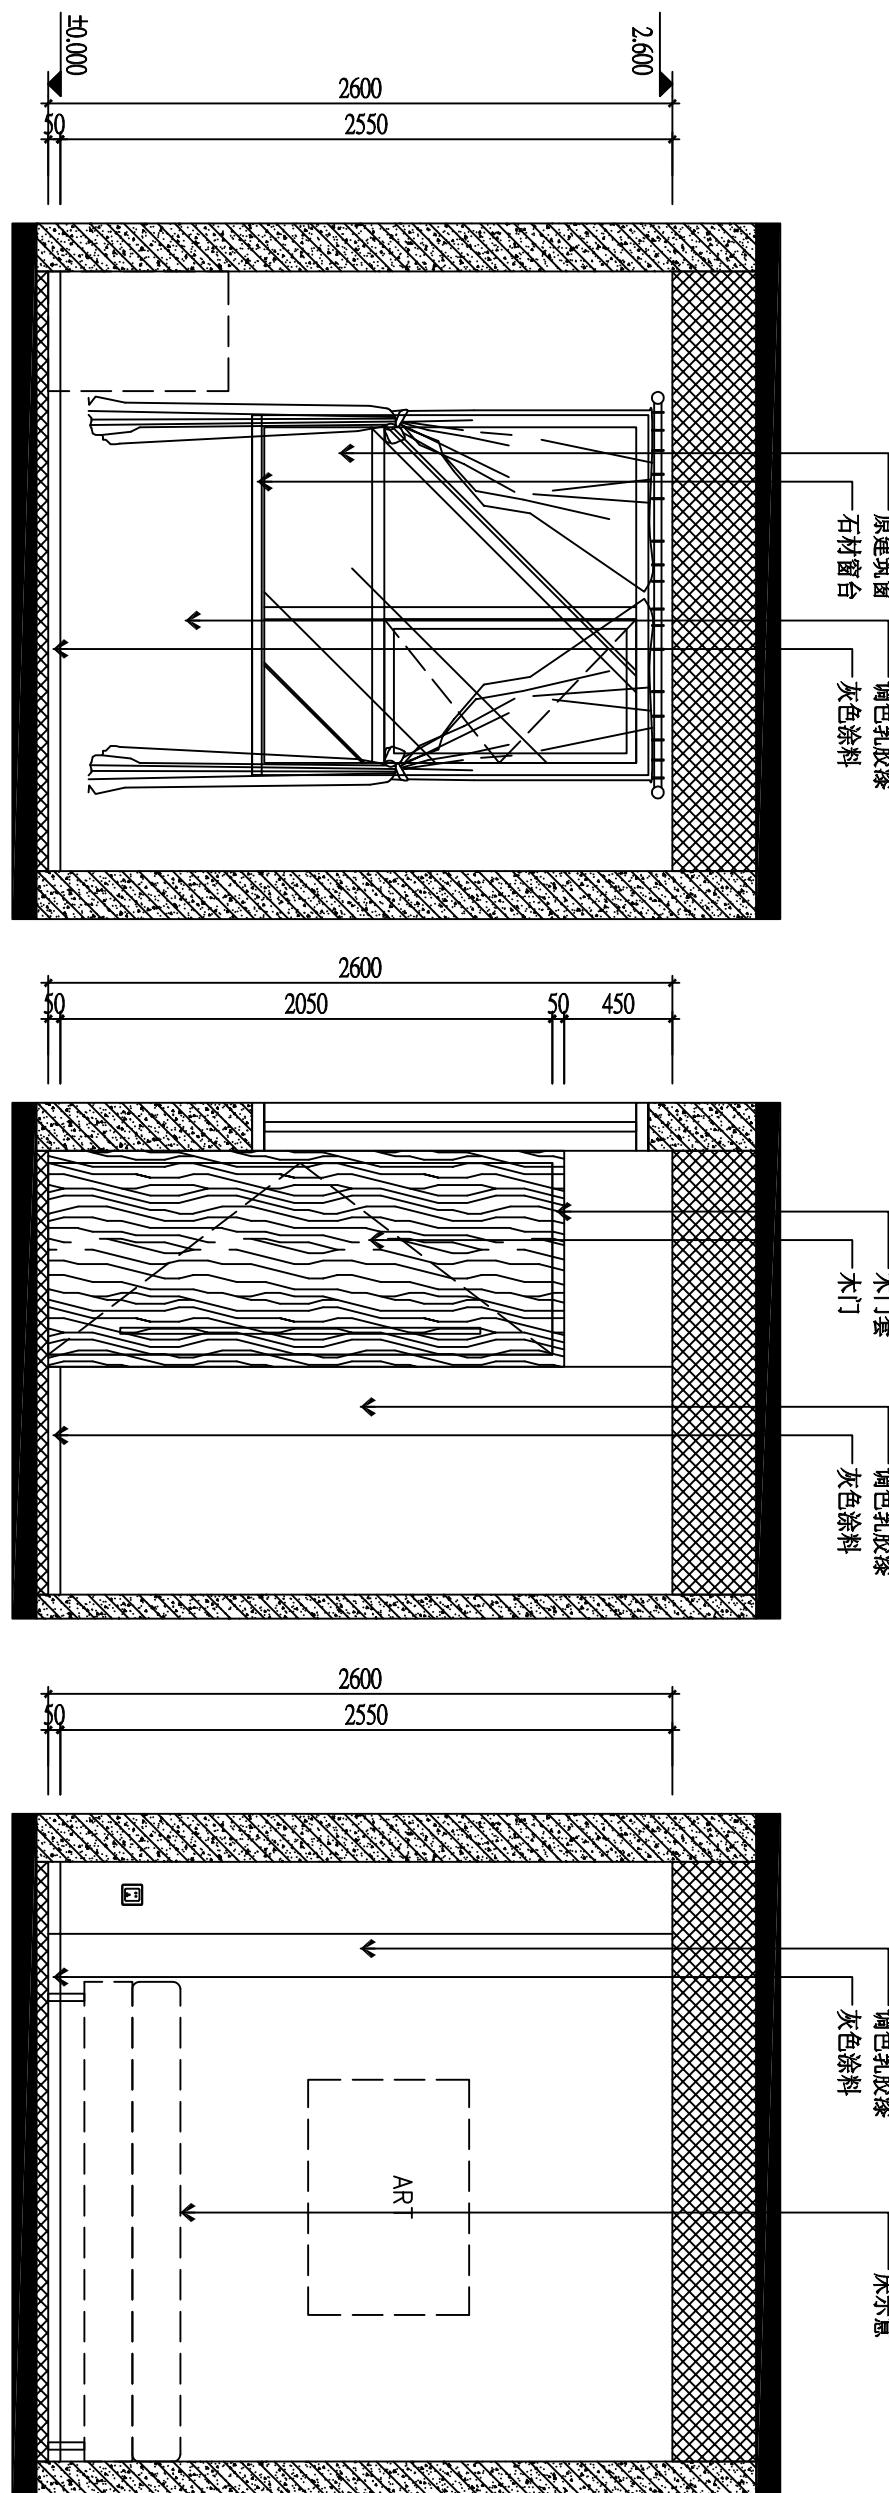

是境
设计

备 注
NOTE

□本图未经同意，不得复制图纸及其设计任何部分。

□有图尺寸标注须在实际工地上复核及量度。

□请勿比例量度图纸，应采用已标明的尺寸。

□本图纸必须和规格说明、合同条款及其有关图纸，并使用，如发现图纸内容有不符之处，必须立刻通知设计师。

业 主
CLIENT

项 目 名 称
PROJECT

总 负 责
PRINCIPAL

设 计
DESIGNER

绘 图
DRAWN BY

校 对
COLLATE


审 核
APPROVE

比 例
SCALE

日 期
DATE

图 名
DRAWING TITLE

图 号
SHEET NO

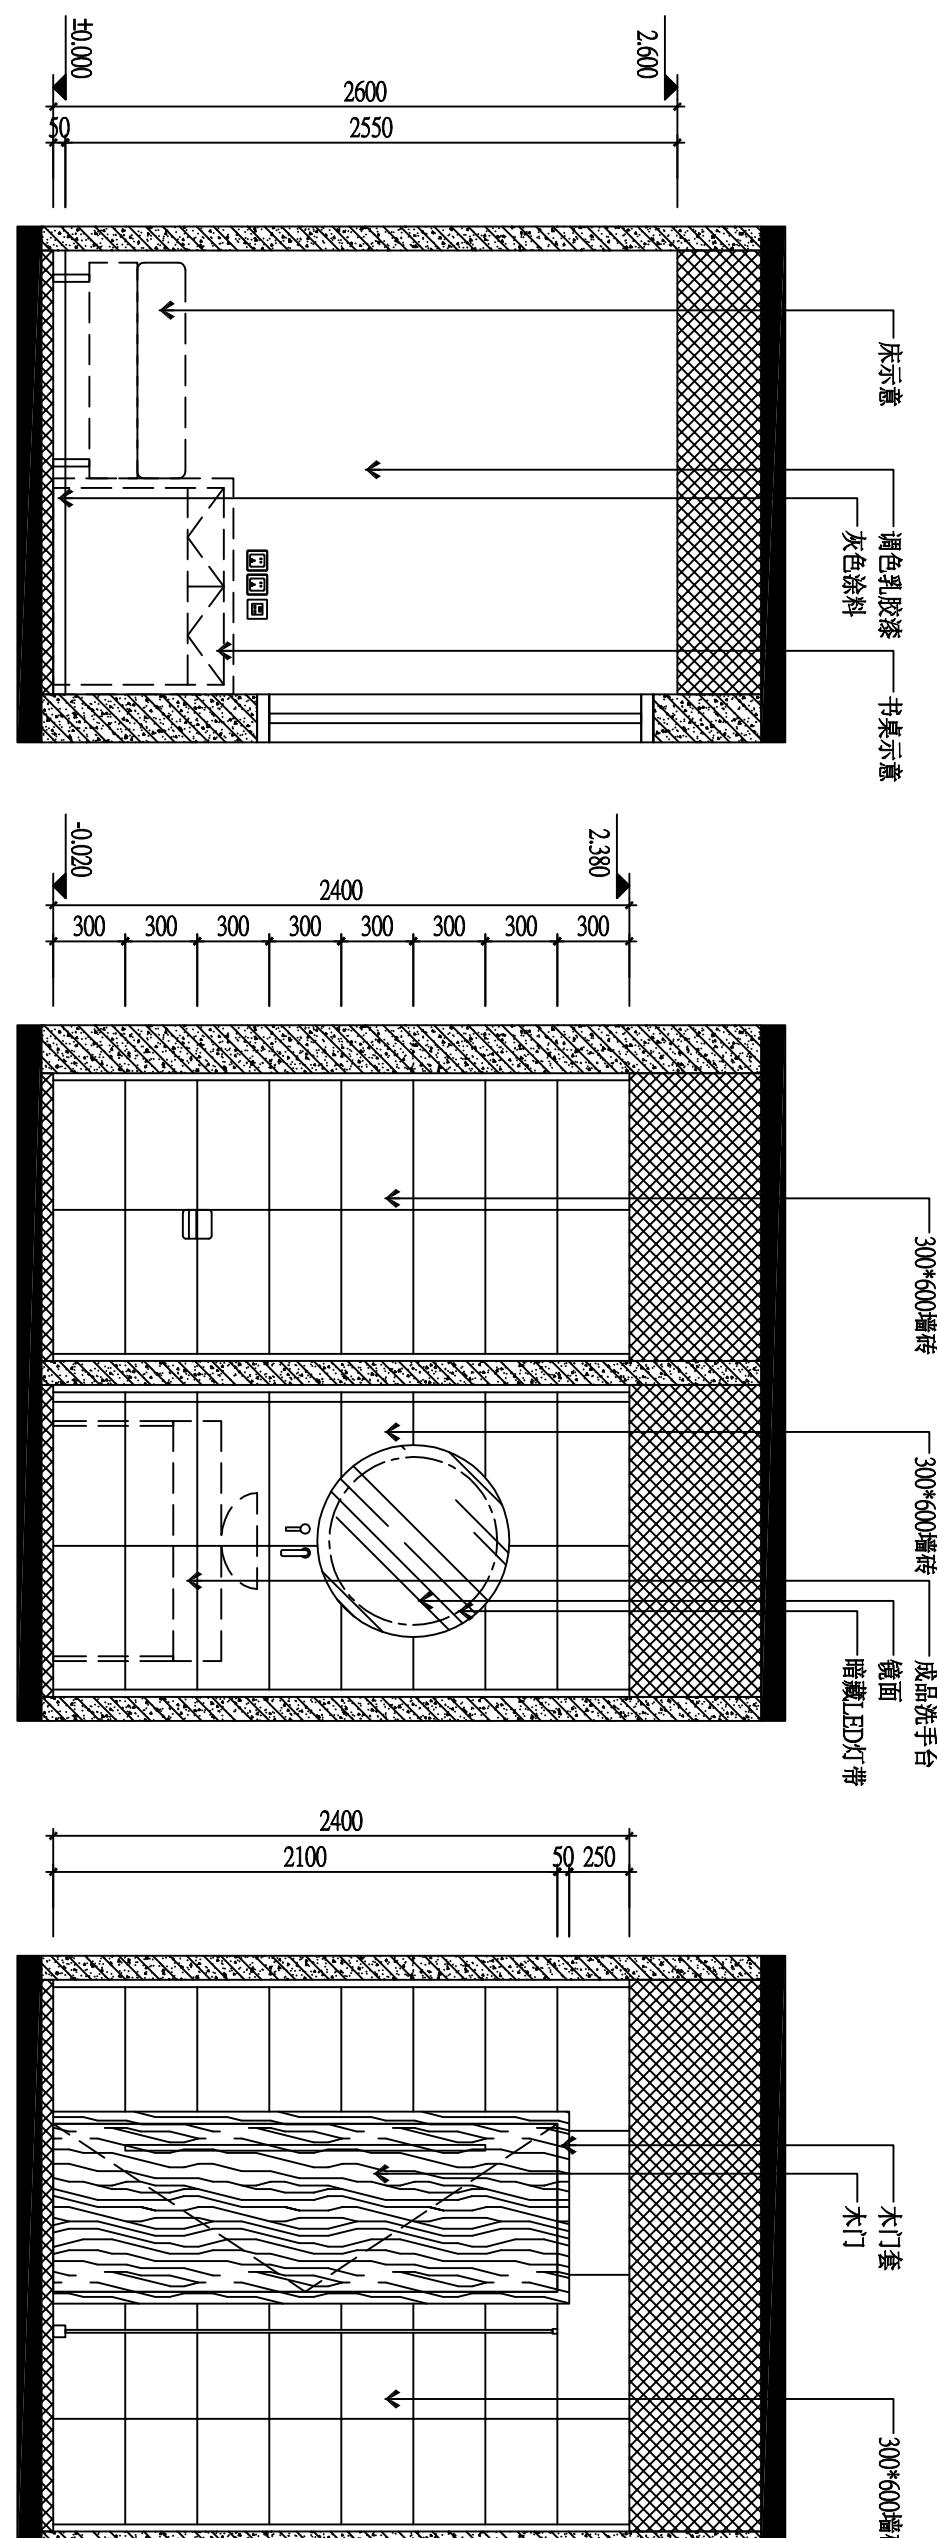

14 3F卧室内立面图
SCALE:1:50
JFPK

15 3F卫生间立面图
SCALE:1:30
JFPK

16 3F卫生间立面图
SCALE:1:30
JFPK

是 境
設 計

3F.E-06

备 注
NOTE

- 本图未经同意，不得复制图纸及其设计任何部分。
- 有图纸尺寸标注须在实际工地上复核及量度。
- 请勿按比例量度图纸，应采用已标明的尺寸。
- 本图纸必须和规格说明、合同条款及其有关图纸，并使用，如发现图纸内容有不符之处，必须立刻通知设计师。

业 主

CLIENT

项 目 名 称
PROJECT

龙湖椿山

总 负 责
PRINCIPAL

设计
DESIGNER

绘 图
DRAWN BY

校 对
COLLATE

审 核
APPROVE

比 例
SCALE

1: 30

日 期
DATE


2020.07

图 名
DRAWING TITLE

3F立面布置图

图 号
SHEET NO

3F.E-07

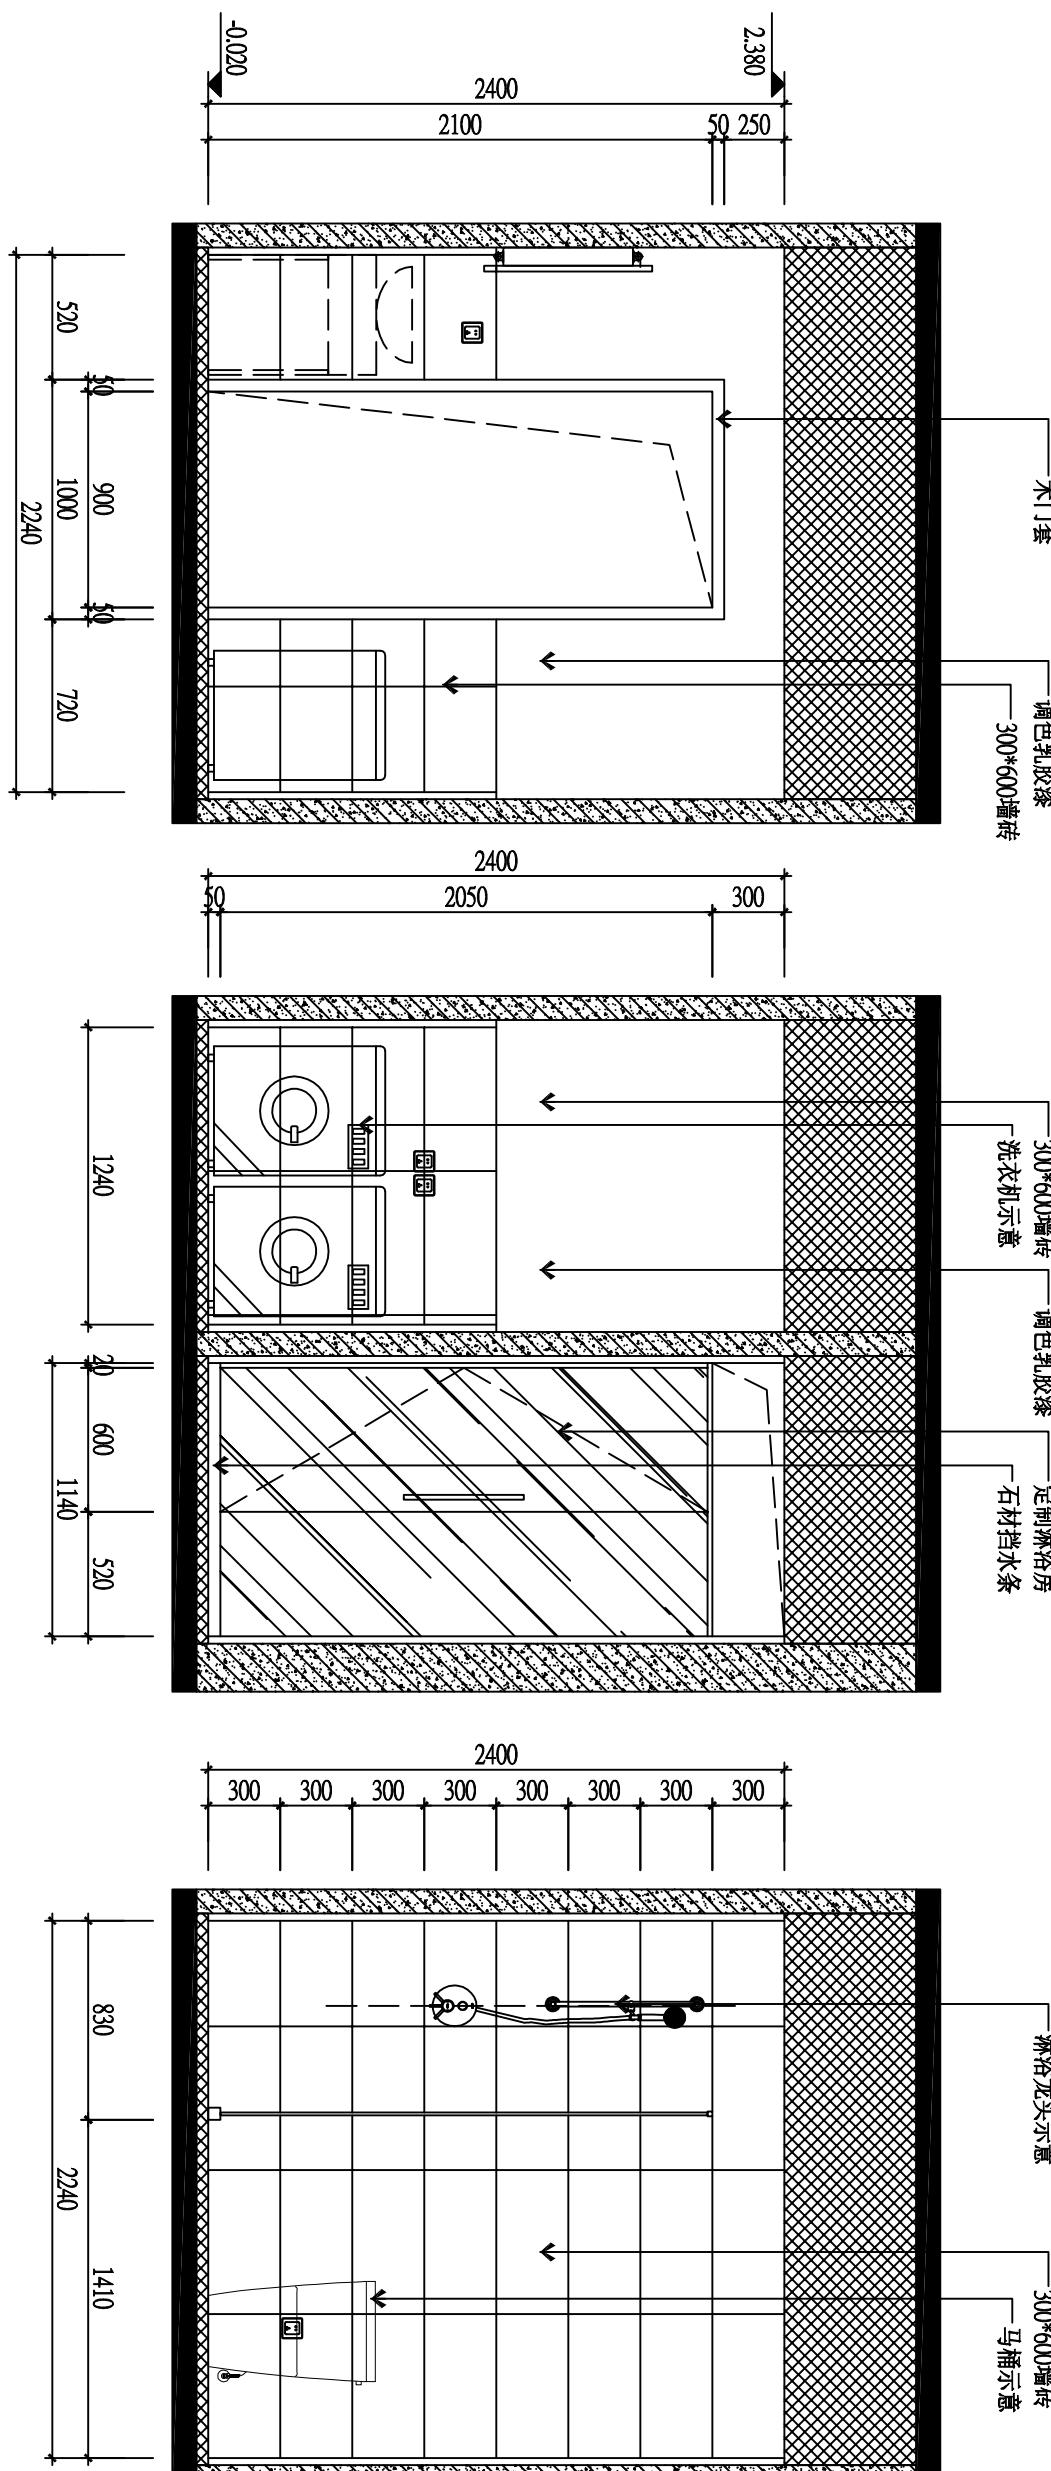

17 3F卫生间立面图
SCALE:1:30
JRP-06

18 3F卫生间立面图
SCALE:1:30
JRP-06

19 3F卫生间立面图
SCALE:1:30
JRP-06

是 境
設 計

备
注
NOTE

□本图未经同意，不得复制图纸及其设计任一部分。
□有图纸尺寸标注须在实际工地复核及量度。

□勿按比例量度图纸，应采用已标明的尺寸。

□本图纸必须和规格说明、合同条款及其他有关图纸，并使用，如发现图纸内容有不符之处，必须立刻通知设计师。

业
主
CLIENT

项
目
名
称
PROJECT
龙湖椿山

总
负
责
人
PRINCIPAL

设
计
师
DESIGNER

绘
图
DRAWM BY

校
对
COLLATE




审
核
APPROVE

比
例
SCALE

日
期
DATE

图
名
DRAWING TITLE

图
号
SHEET NO

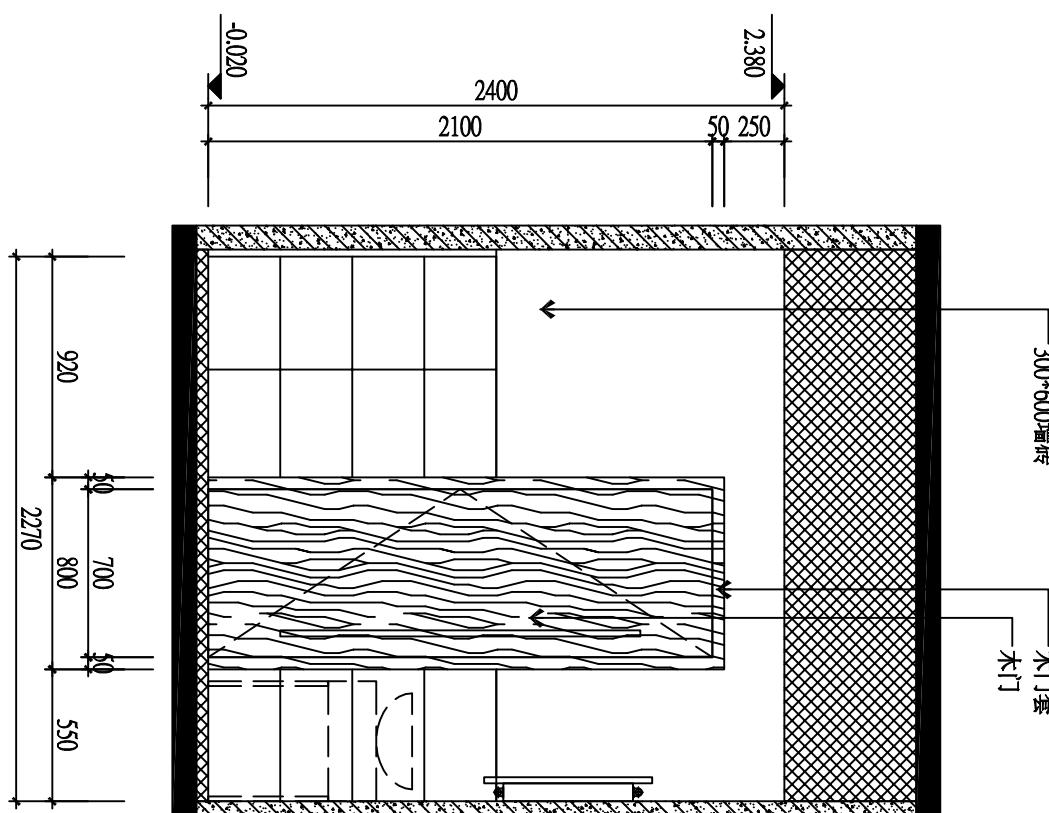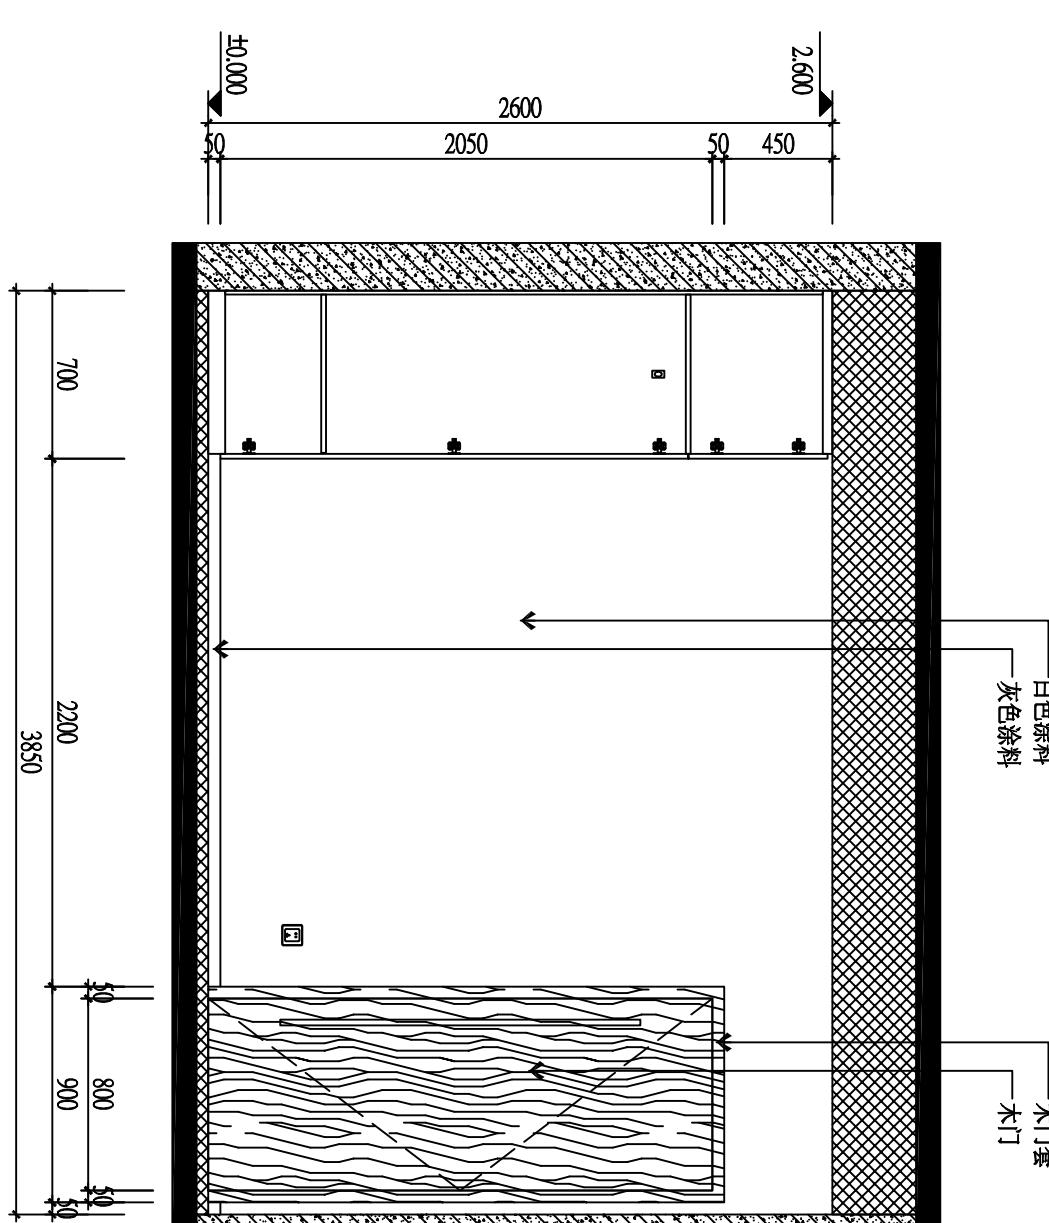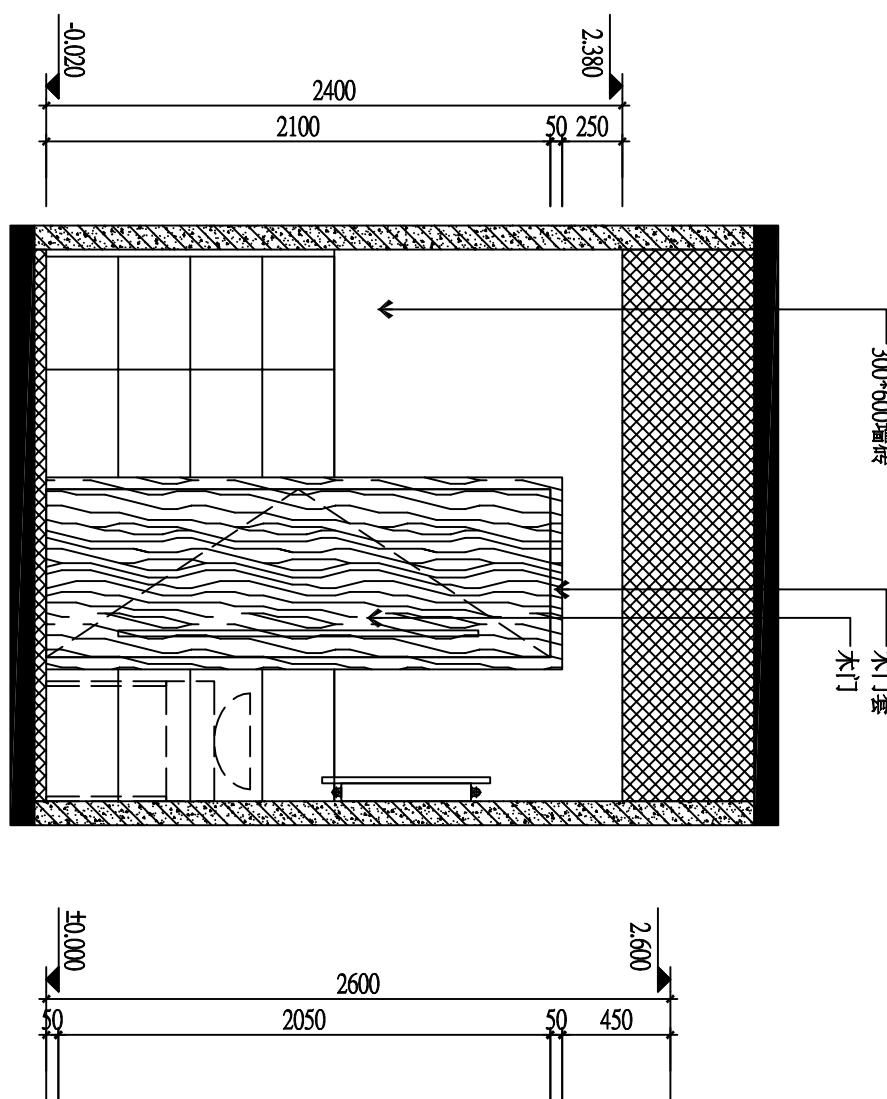

20 3F卫生间立面图
3FP-06 SCALE:1/30

21 3F卧室立面图
3FP-06 SCALE:1/30

是
境
設
計

3F.E-08

备注
NOTE

□本图未经同意，不得复制图纸及其设计任何部分。

□有图尺寸标注须在实际工地上复核及量度。

□勿按比例量度图纸，应采用已标明的尺寸。

□本图纸必须和规格说明、合同条款及其他有关图纸一并使用。如发现图纸内容有不符之处，必须立刻通知设计师。


业 主	CLIENT
项 目 名 称	PROJECT
总 负 责	龙湖椿山
PRINCIPAL	
设 计	
DESIGNER	
绘 图	
DRAWN BY	
校 对	
COLLATE	
审 核	
APPROVE	
比 例	1: 30
SCALE	
日 期	2020.07
DATE	

图 名
DRAWING TITLE

3F立面布置图

图 号
SHEET NO

3F.E-09

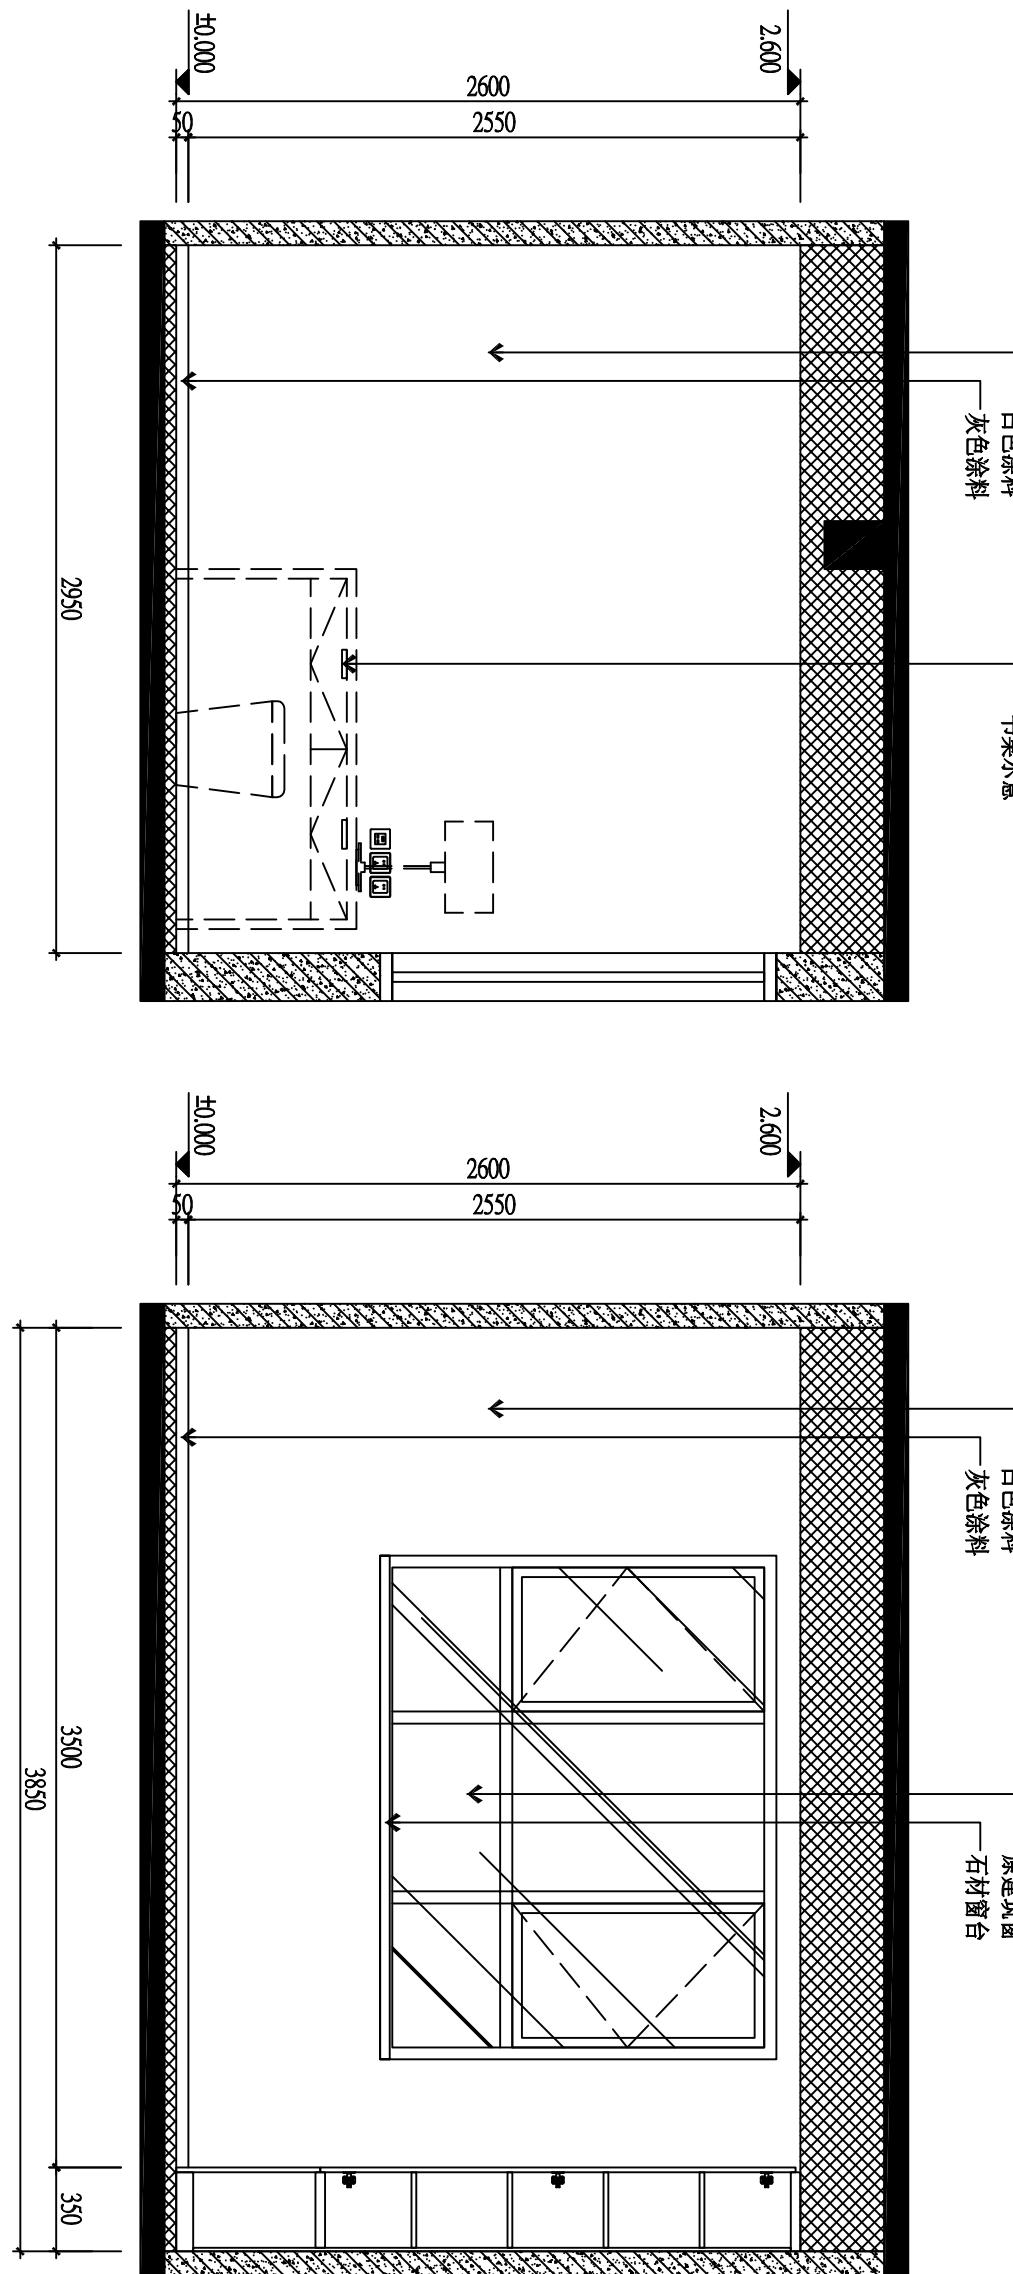

22 3F卧室立面图
SCALE:1:30

23 3F卧室立面图
SCALE:1:30

是境
设计

备注
NOTE

□本图未经同意，不得复制图纸及其设计任何部分。
□有图纸尺寸标注须在实际工地上复核及量度。


□勿按比例量度图纸，应采用已标明的尺寸。

□本图纸必须和规格说明、合同条款及其他有关图纸一并使用。如发现图纸内容有不符之处，必须立刻通知设计师。

业 主	CLIENT
项 目 名 称	PROJECT
总 负 责 人	龙湖椿山
设 计 师	PRINCIPAL DESIGNER
绘 图	DRAWN BY
校 对	COLLATE
审 核	APPROVE
比 例	SCALE
日 期	DATE
图 名	DRAWING TITLE

3F立面布置图
SHEET NO

3F.E-10

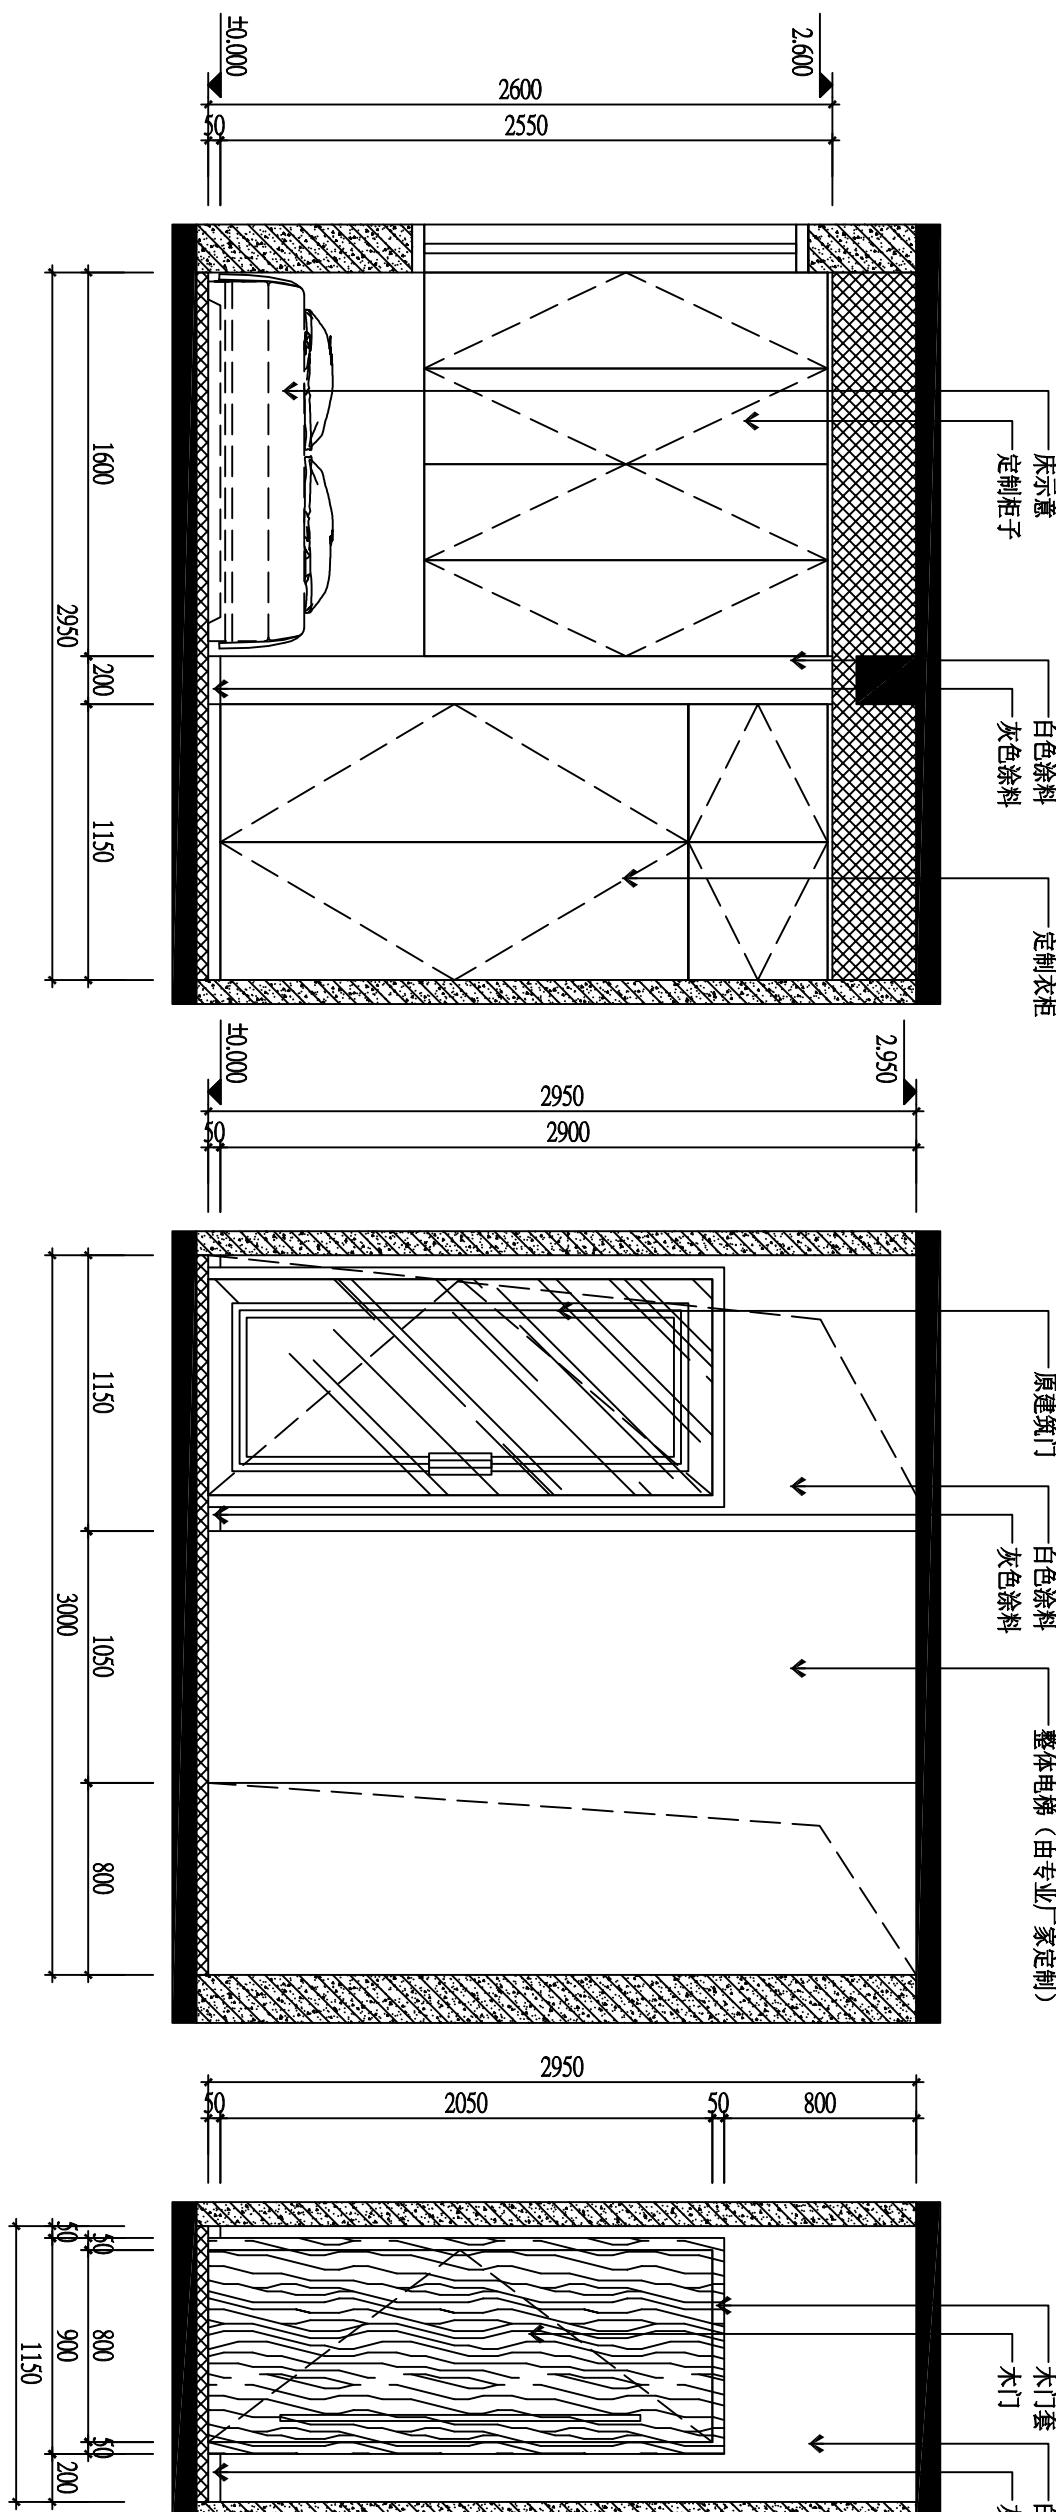

24 3F卧室立面图
3F-E6 SCALE:1:30

25 3F公共区域立面图
3F-E6 SCALE:1:30

26 3F公共区域立面图
3F-E6 SCALE:1:30


是境
设计

备注

□在未经同意前，不得复制图纸及其设计任何部份。

- 所有图纸尺寸标注须在实际工地上复核及量度。
- 请勿按比例量度图纸，应采用已标明的尺寸。
- 本图纸必须和规格说明、合同条款及其有关图纸一并使用，如发现图纸内容有不符之处，必须立刻通知设计院。

业 主
CLIENT

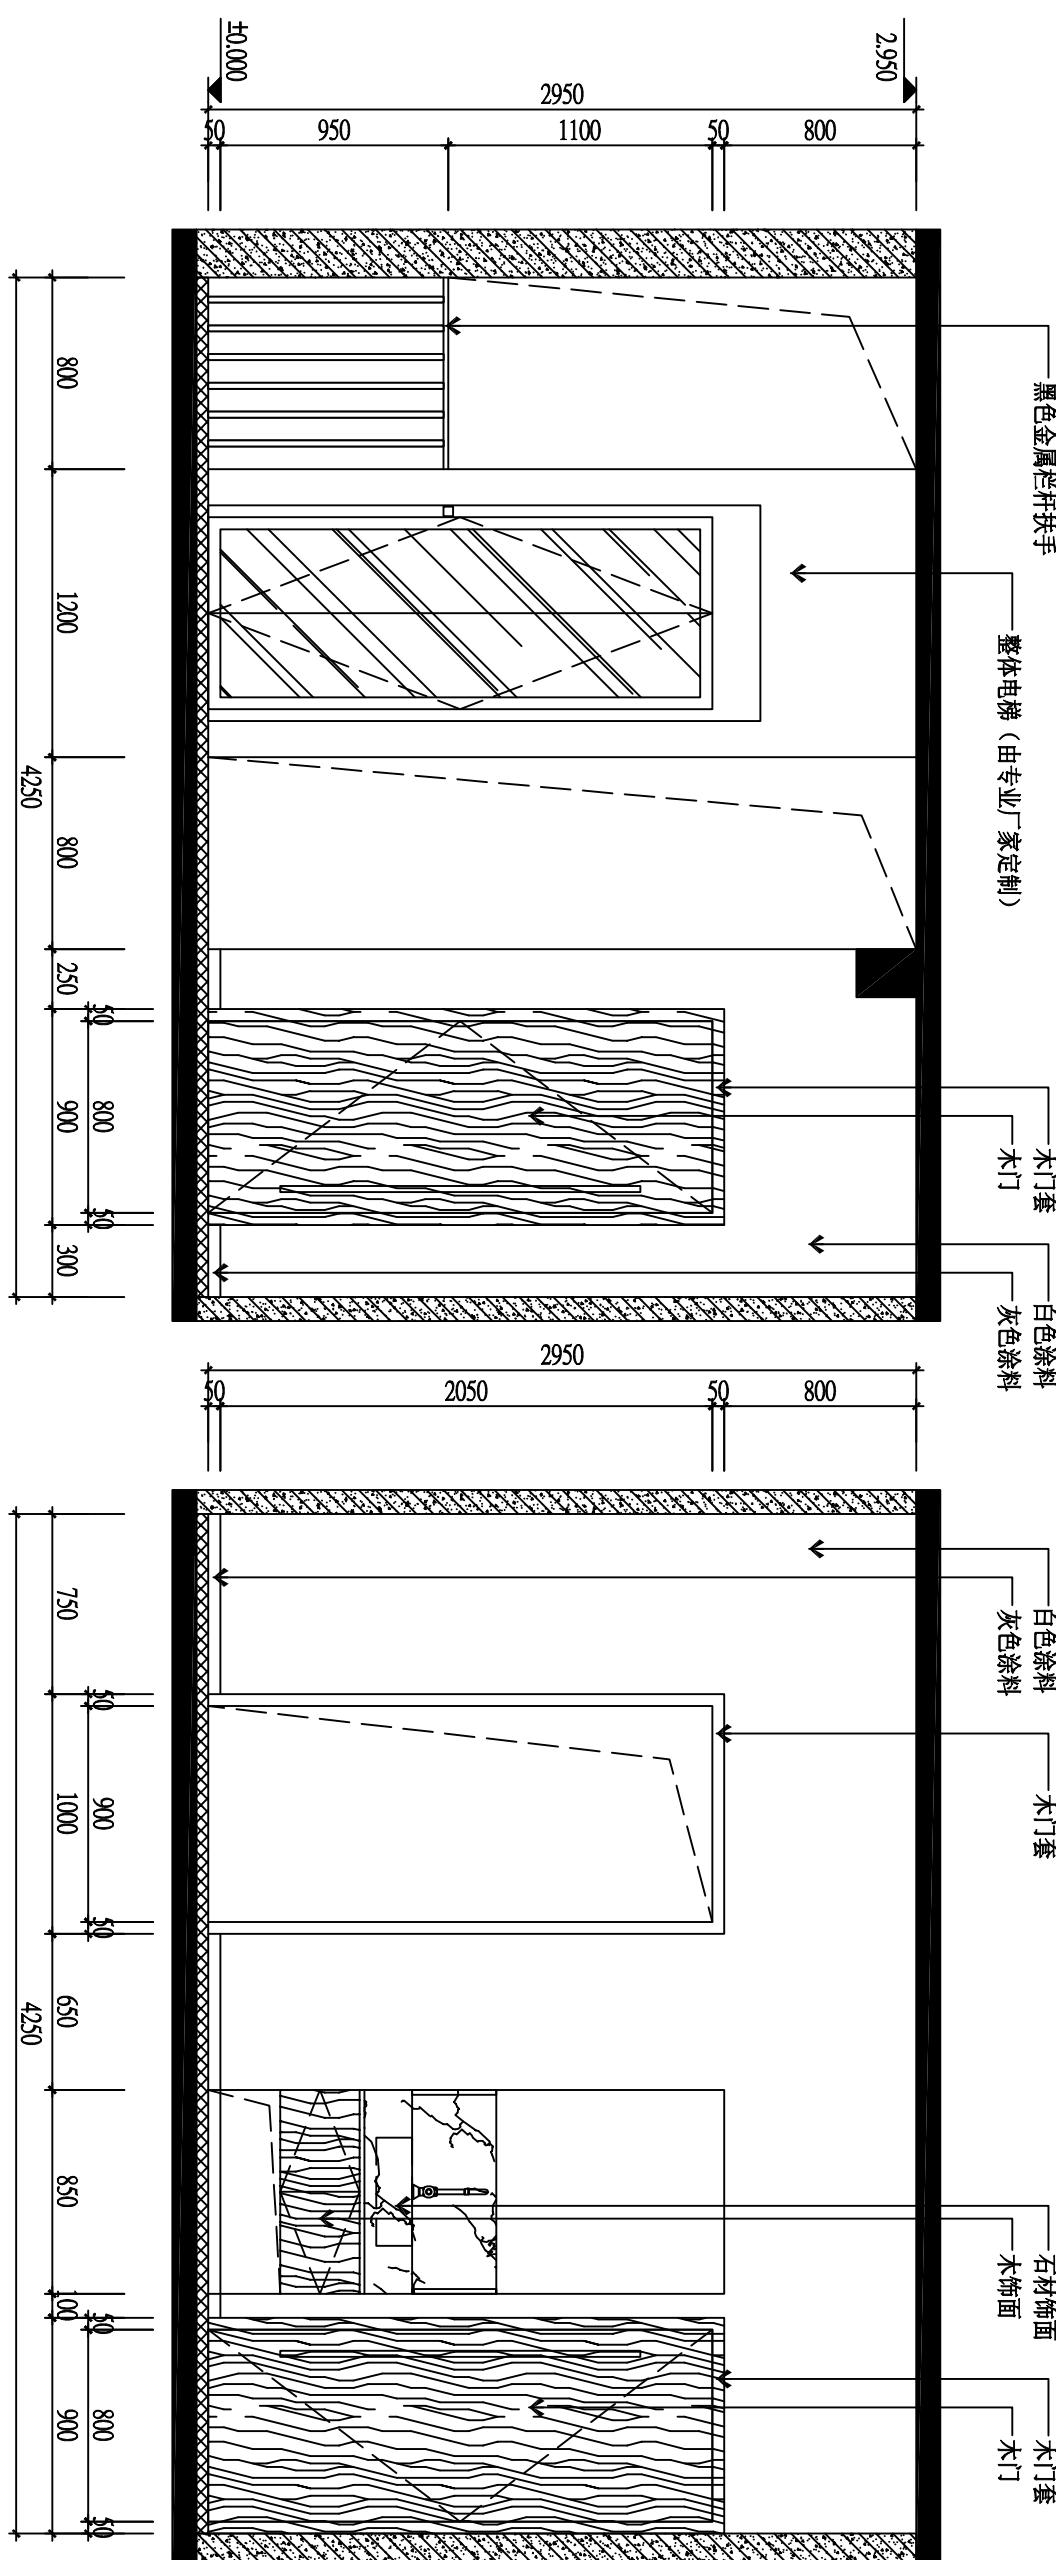

27 3F公共区域立面图
3FP46 SCALE:1:300

28
3F公共区域立面图
SCALE:1:300